


符 號	說 明	備 註
s	開關燈切	
⊕	餐吊燈	燈具自備
⊗	15CM LED 崁燈	4000K
==●==	T5 燈管	3000K
==✖==	LED燈條	3000K
⊗	5.5CM 櫃內燈	N
⊕	9 CM 投射燈	4000K
Ⓢ	偵煙感知器	延伸*4

尺寸依現場實際狀況為準

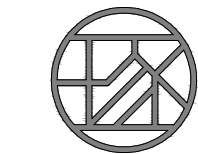



琢越空間設計

DRAW INTERIOR DESIGN 台中市臺灣大道二段285號31F

本圖內容	燈具配置圖	設計	Alison	比例	1 / 50	日期	
案名	大通大美7A6	繪圖	Alison	單位	CM/公分	114.12.3	圖號 005

符 號	說 明	備 註
s	開關燈切	
⊕	餐吊燈	燈具自備
⊗	15CM LED 嵌燈	4000K
==●==	T5 燈管	3000K
==✱==	LED燈條	3000K
⊗	5.5CM 櫃內燈	N
⊕	9 CM 投射燈	4000K
Ⓢ	偵煙感知器	延伸*4

尺寸依現場實際狀況為準

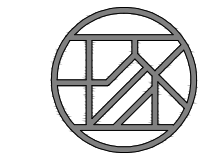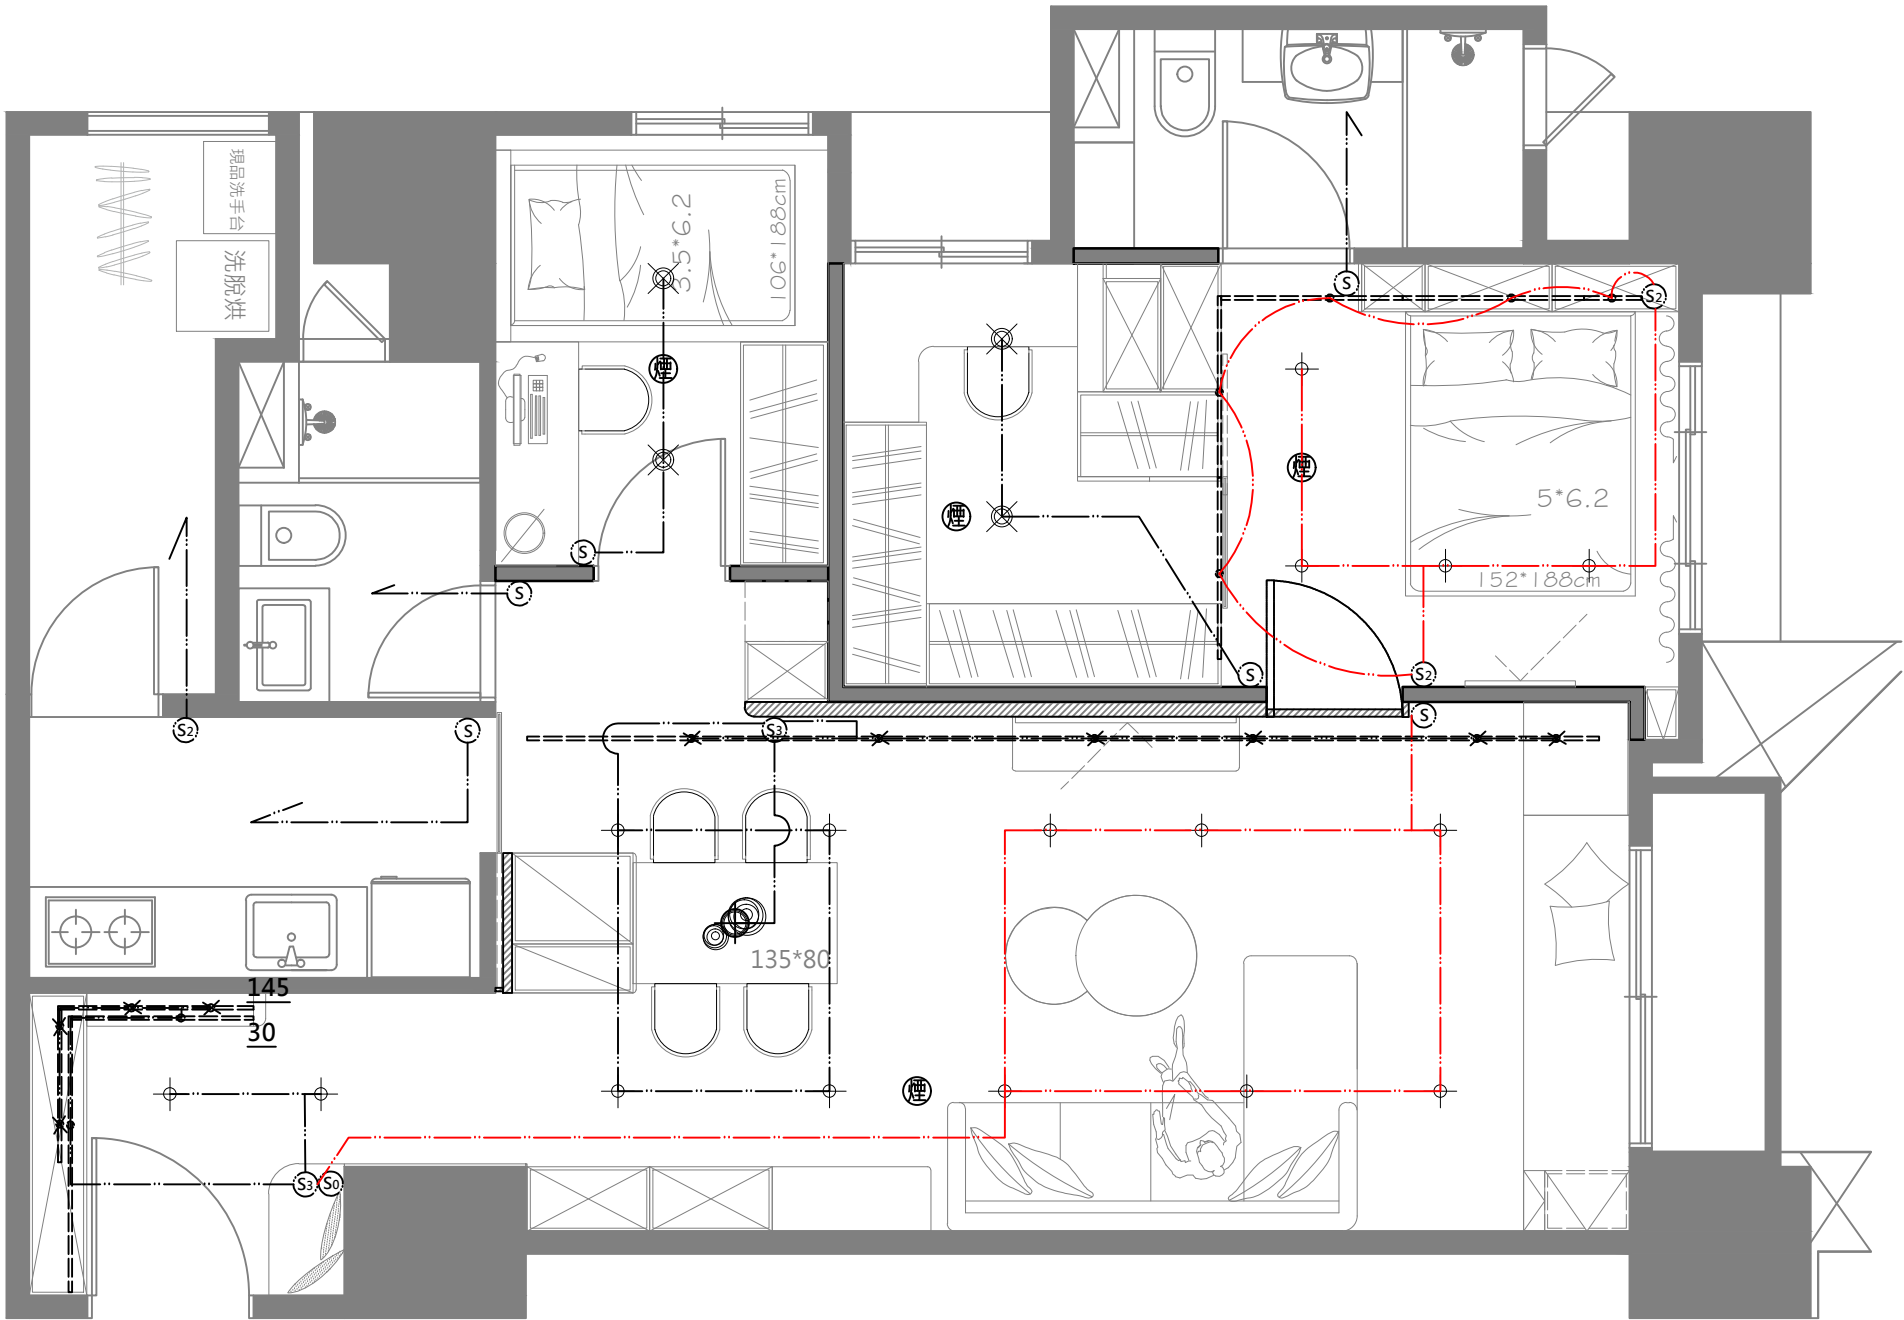

DRAW INTERIOR DESIGN

琢越空間設計

台中市臺灣大道二段285號31F

本圖內容

燈具迴路圖

案名

大通大美7A6

設計

Alison

比例

1 / 50

日期

114.12.3

圖號

005

繪圖



Alison

單位

CM/公分

符 號	說 明	備 註
⓪	電源插座	
Ⓣ	電視專線	
Ⓒ	網路專線	
ⓉⓔⓁ	電話專線	
Ⓜ	專用插座	
對	對講機	原位嵌入
Ⓜ	原有插座	
Ⓜ	選樣面板	業主自備

尺寸依現場實際狀況為準

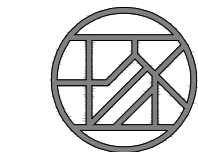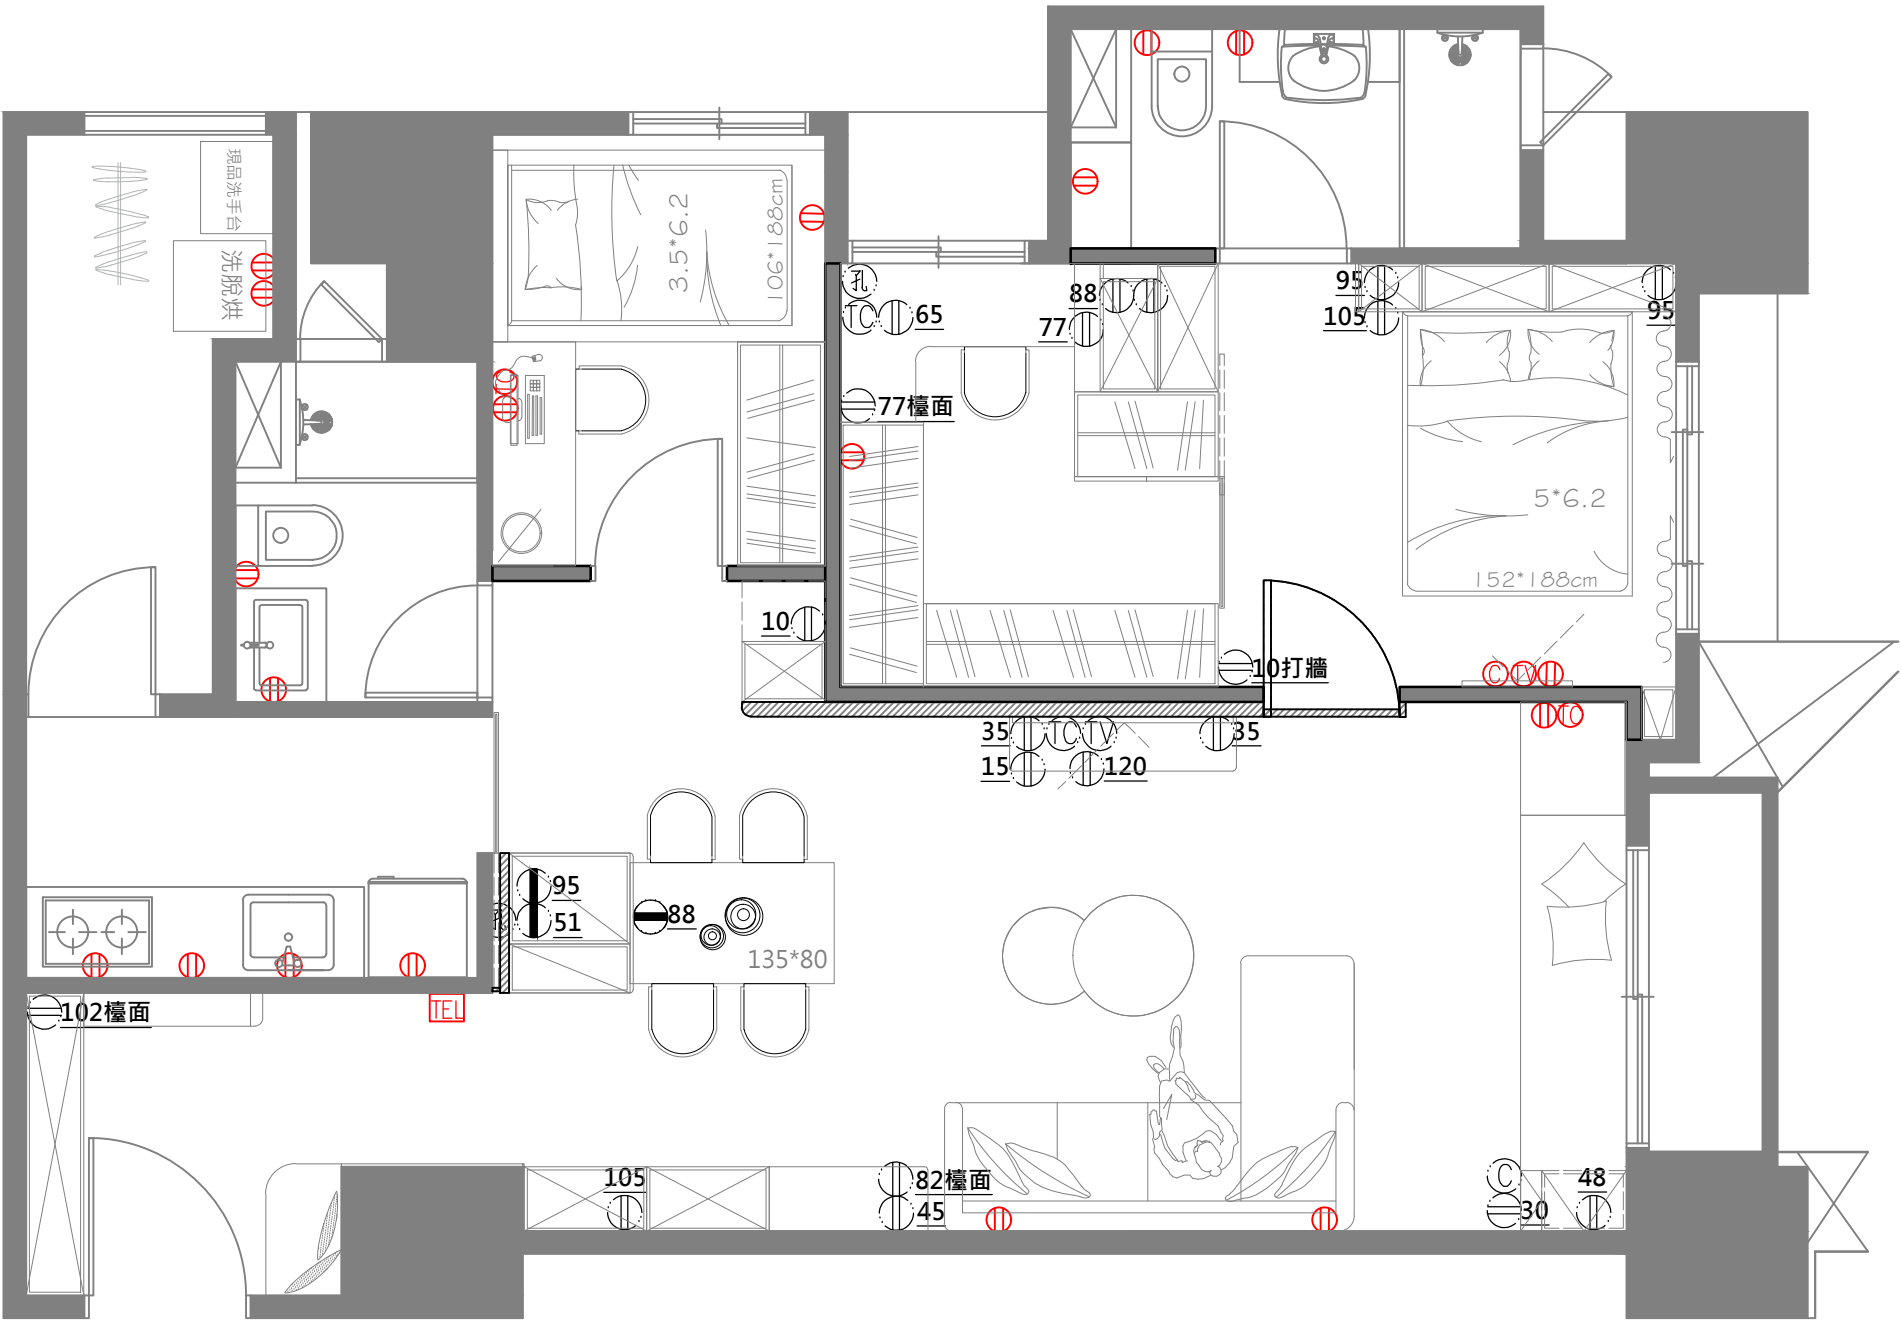

DRAW INTERIOR DESIGN

琢越空間設計

台中市臺灣大道二段285號31F

本圖內容

弱電配置圖

案名

大通大美7A6

設計

Alison

比例

1 / 50

日期

115.4.23

圖號

006

繪圖

Alison

單位

CM/公分