
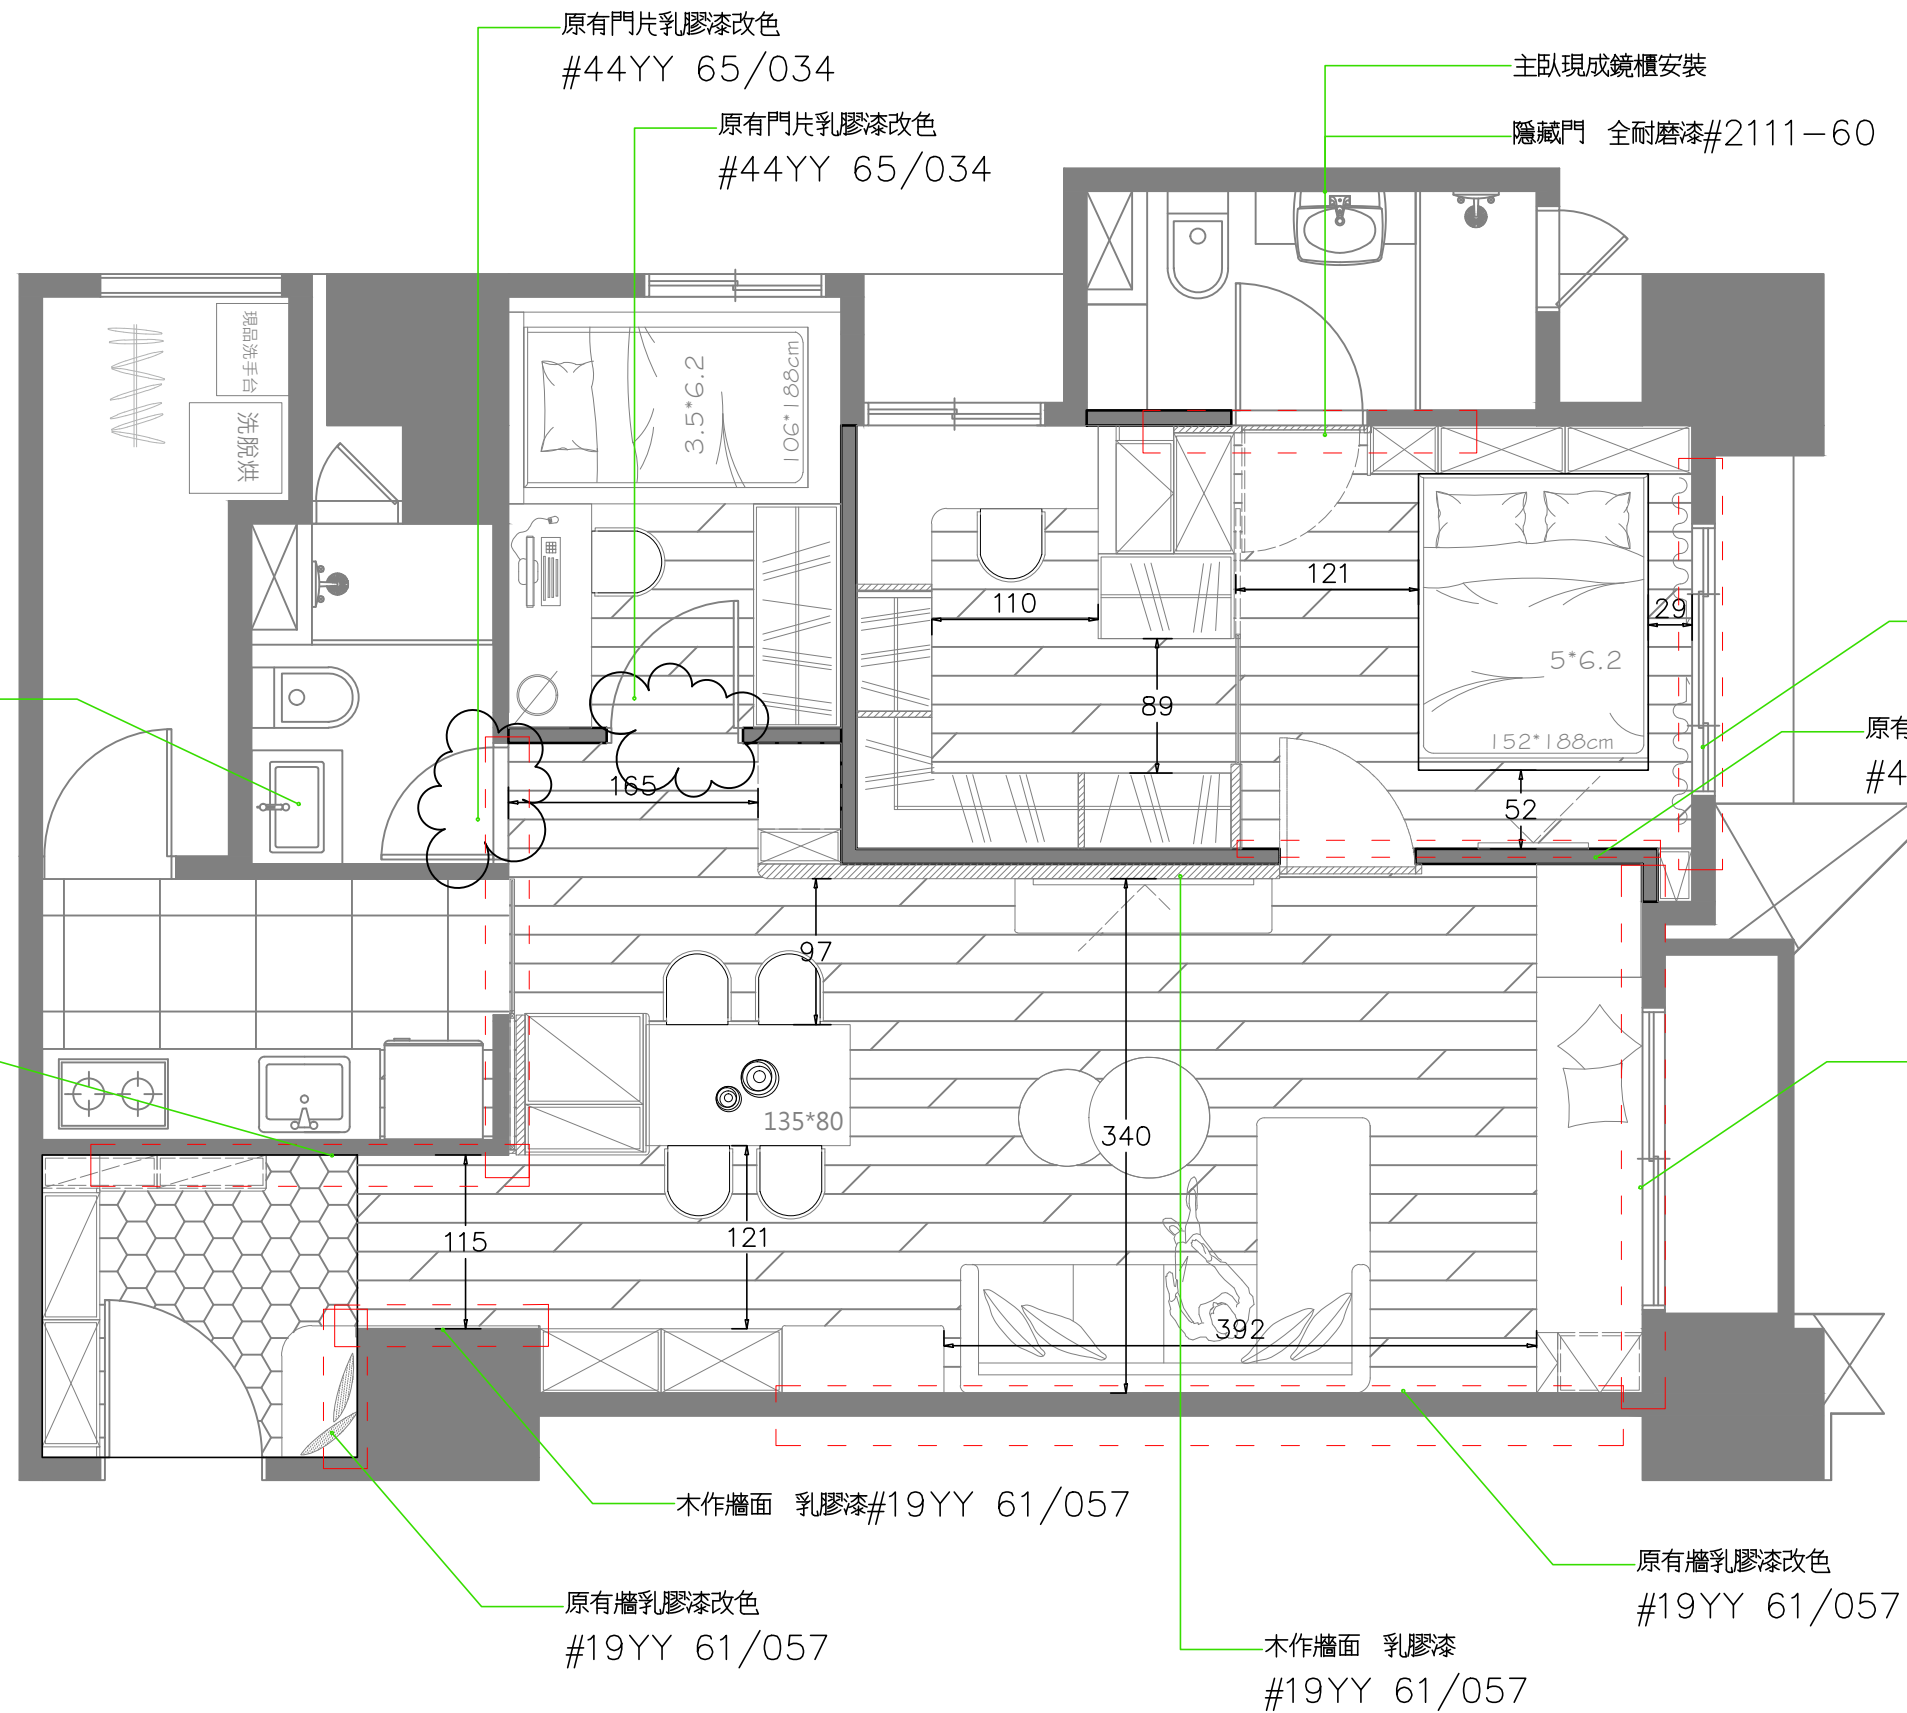




琢越空間設計

DRAW INTERIOR DESIGN 台中市臺灣大道二段285號31F

本圖內容	平面配置圖	設計	Alison	比例	1 / 50	日期		圖號	
案名	大通大美7A6	繪圖	Alison	單位	CM/公分	114.12.3		001	

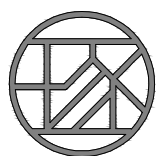

本圖內容	鋪面圖	設計	Alison	比例	1 / 50	日期	
案名	大通大美7A6	繪圖	Alison	單位	CM/公分	114.12.3	圖號 002

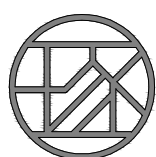
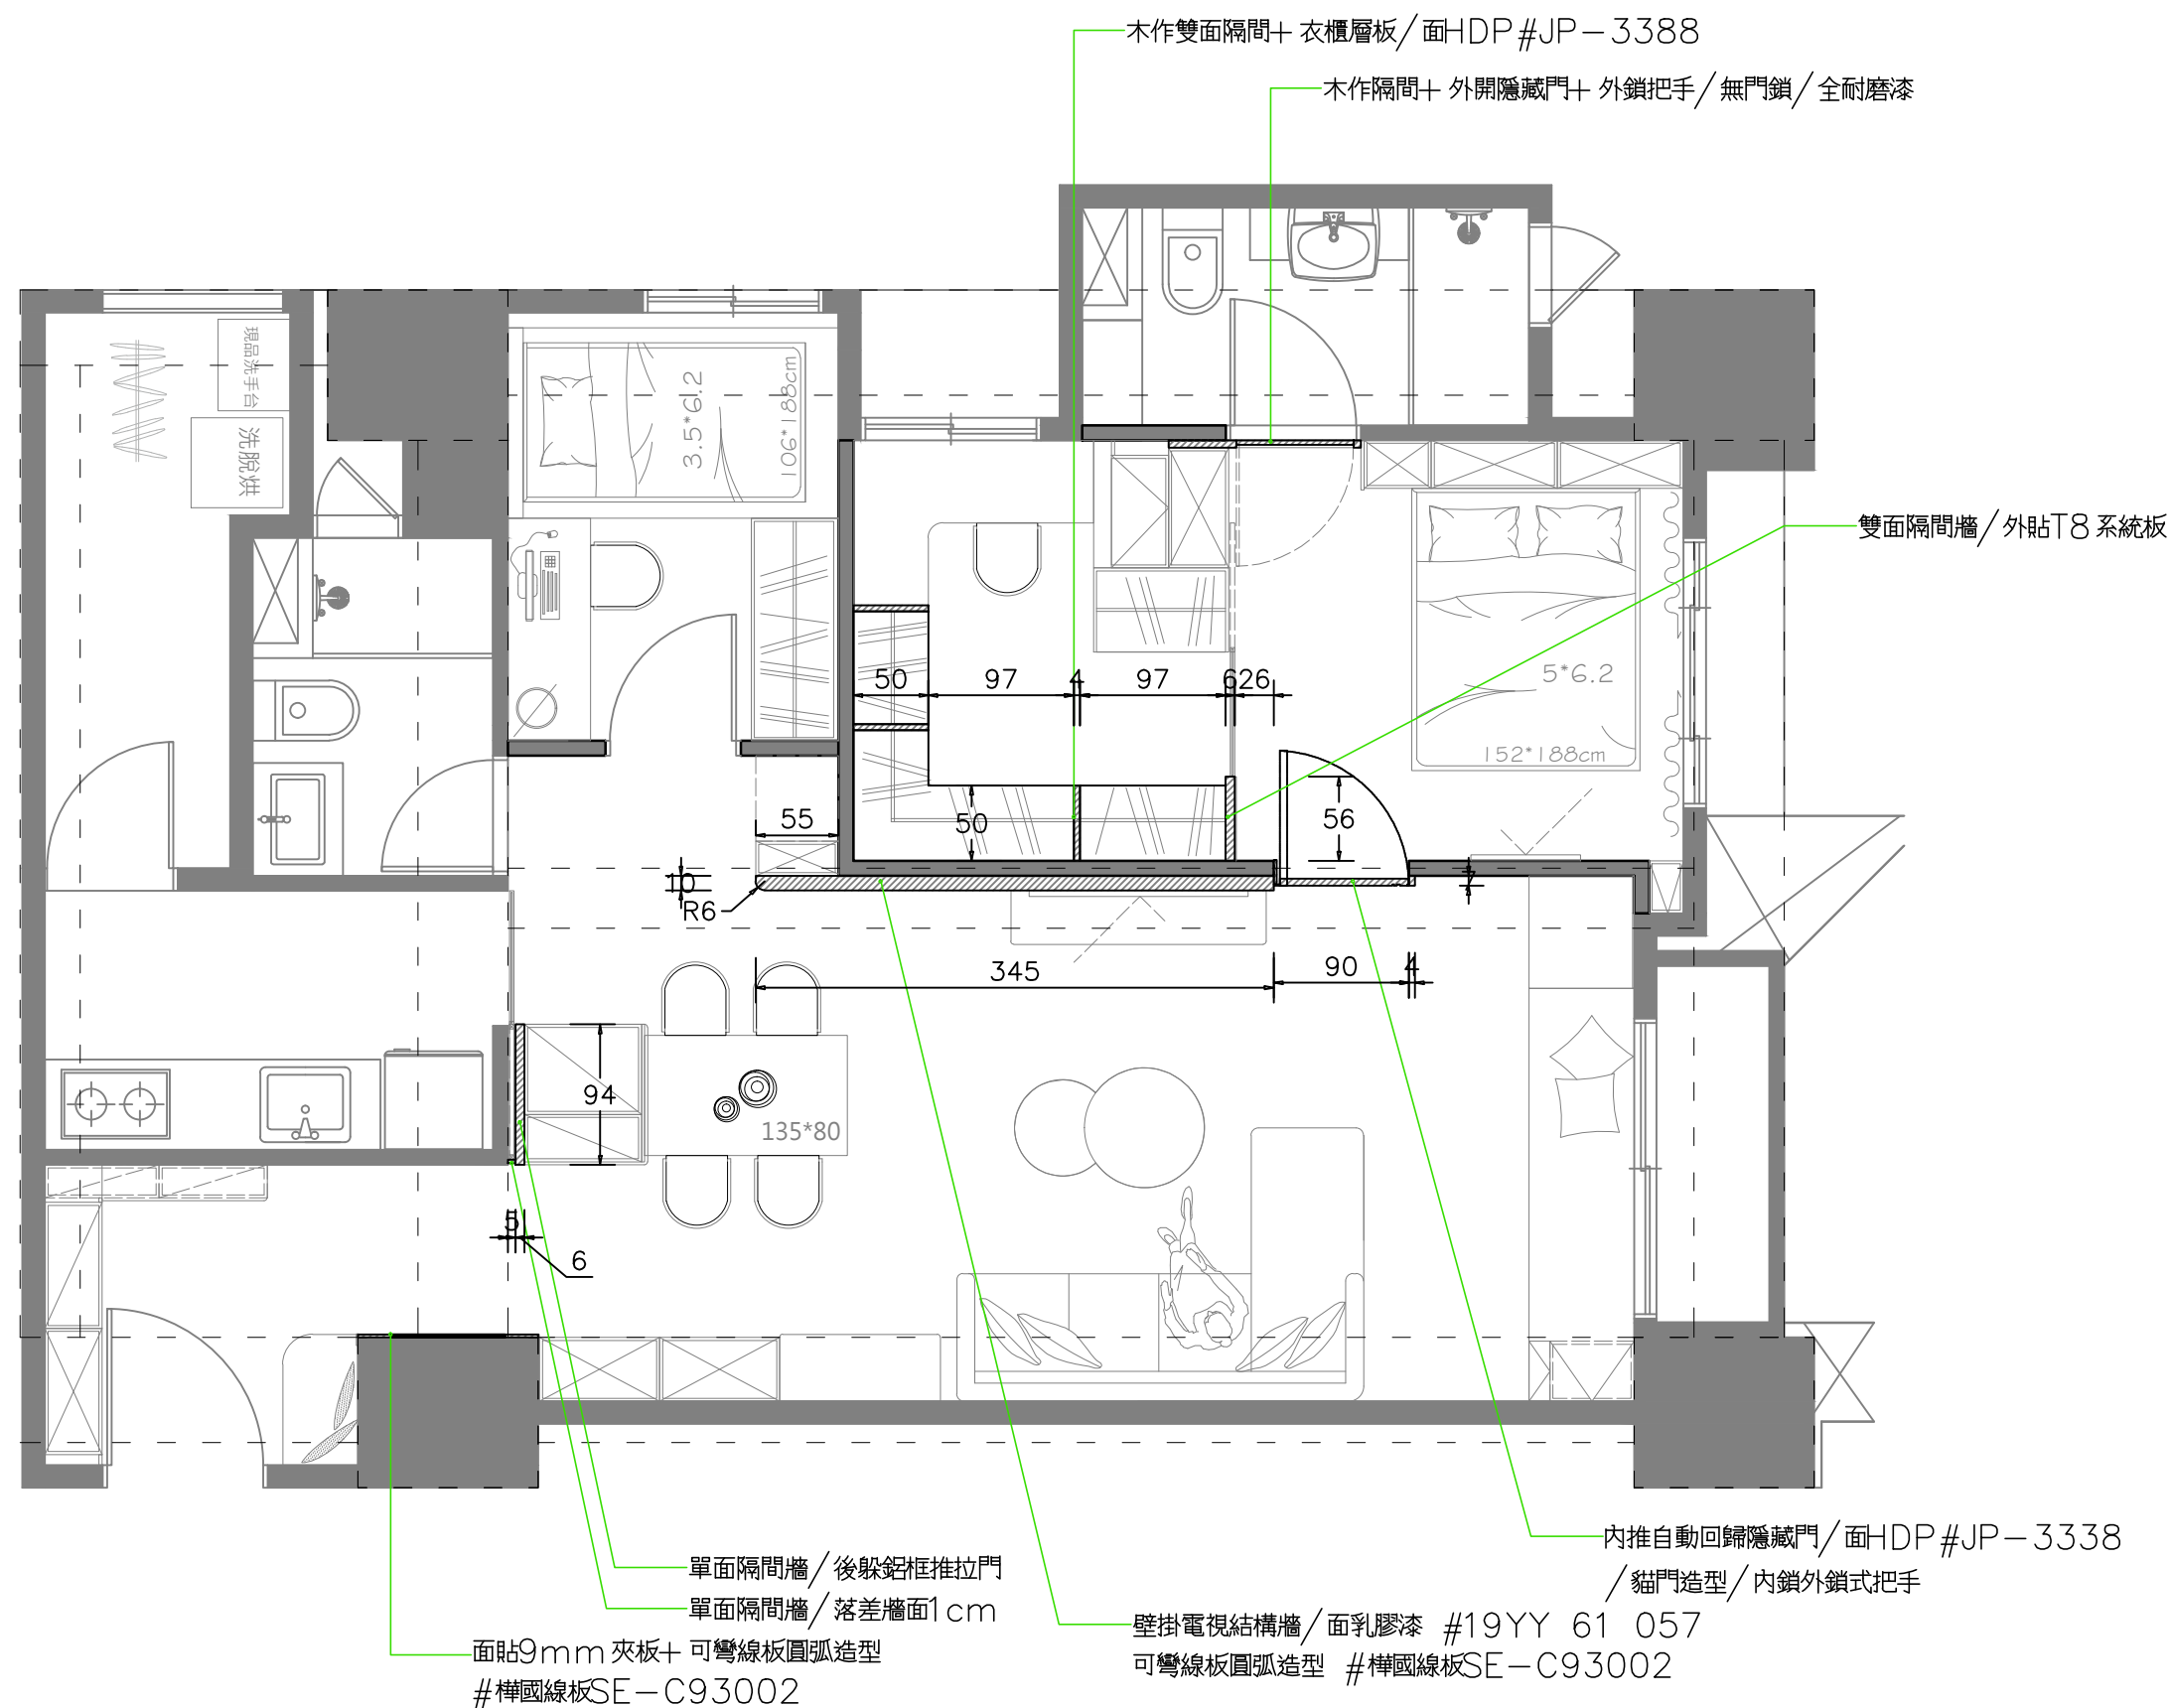


DRAW INTERIOR DESIGN

琢越空間設計

台中市臺灣大道二段285號31F

本圖內容	木作隔間圖	設計	Alison	比例	1 / 50	日期		圖號	
案名	大通大美7A6	繪圖	Alison	單位	CM/公分	114.12.3		003	

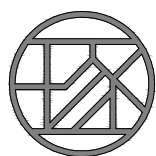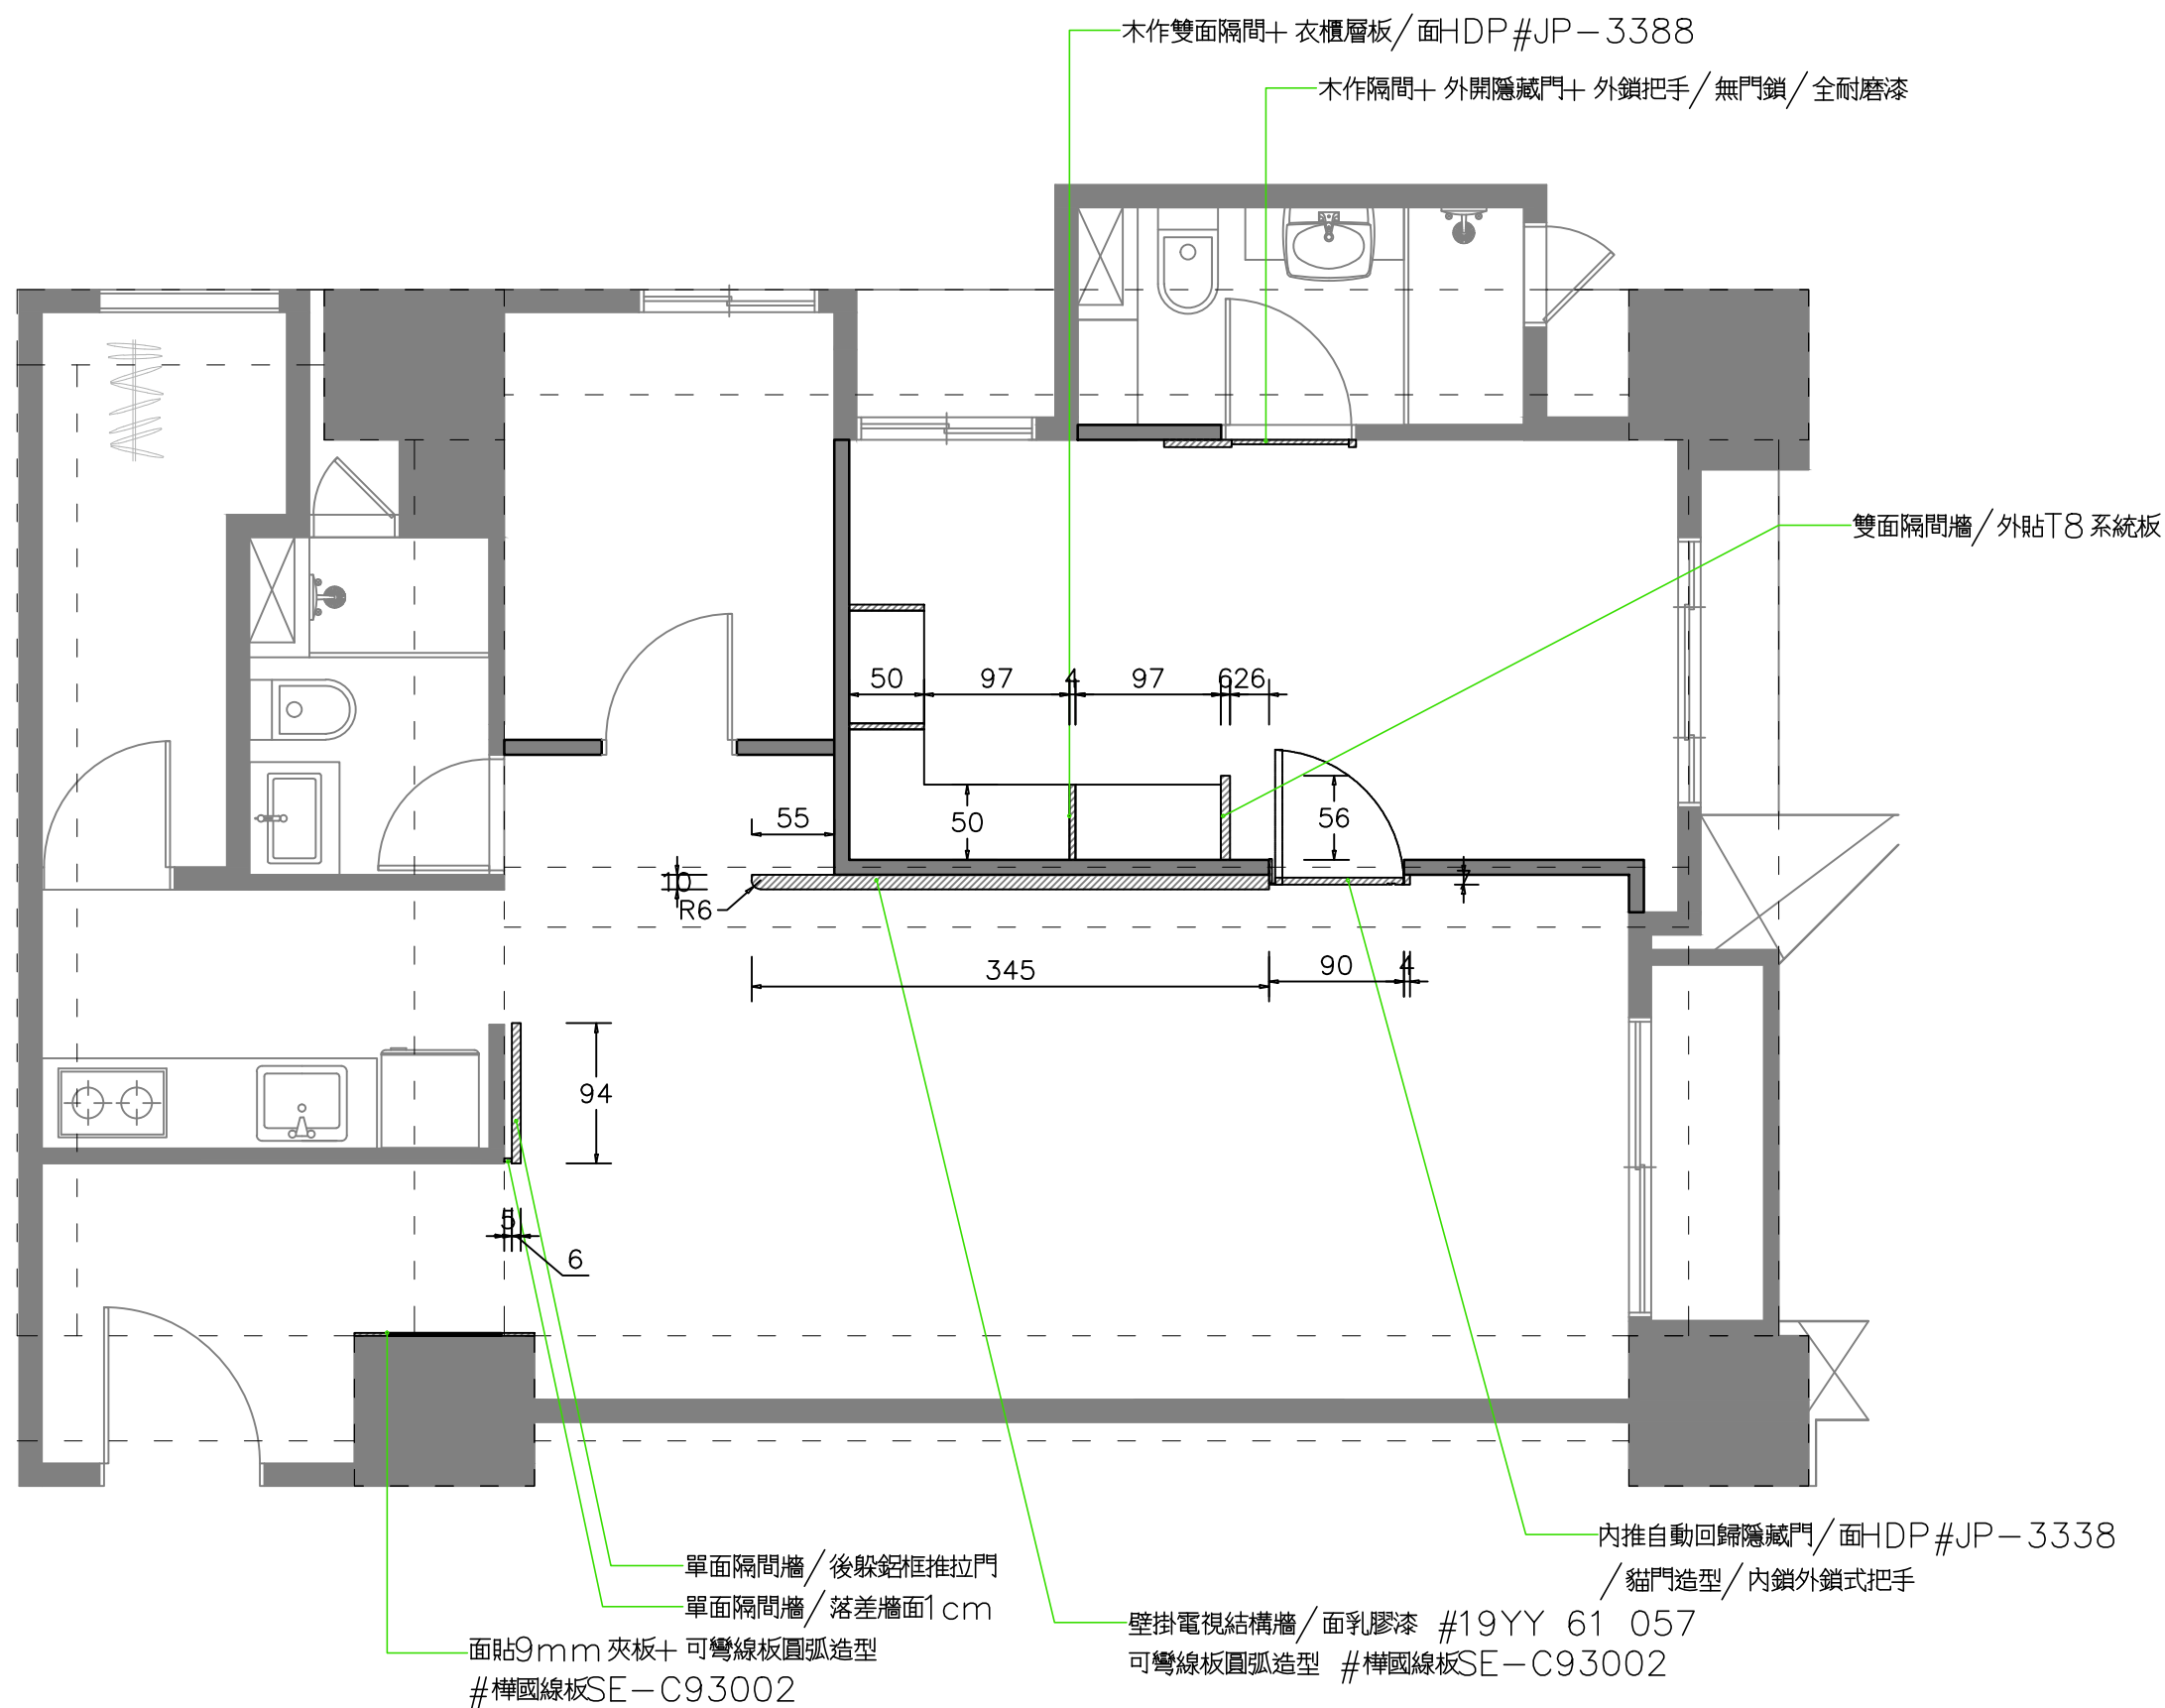

DRAW INTERIOR DESIGN

琢越空間設計

台中市臺灣大道二段285號31F

本圖內容

木作隔間圖

案名

大通大美7A6

設計

Alison

比例

1 / 50

日期

114.12.3

圖號

003



繪圖

Alison

單位

CM/公分

尺寸依現場實際狀況為準

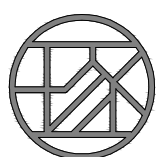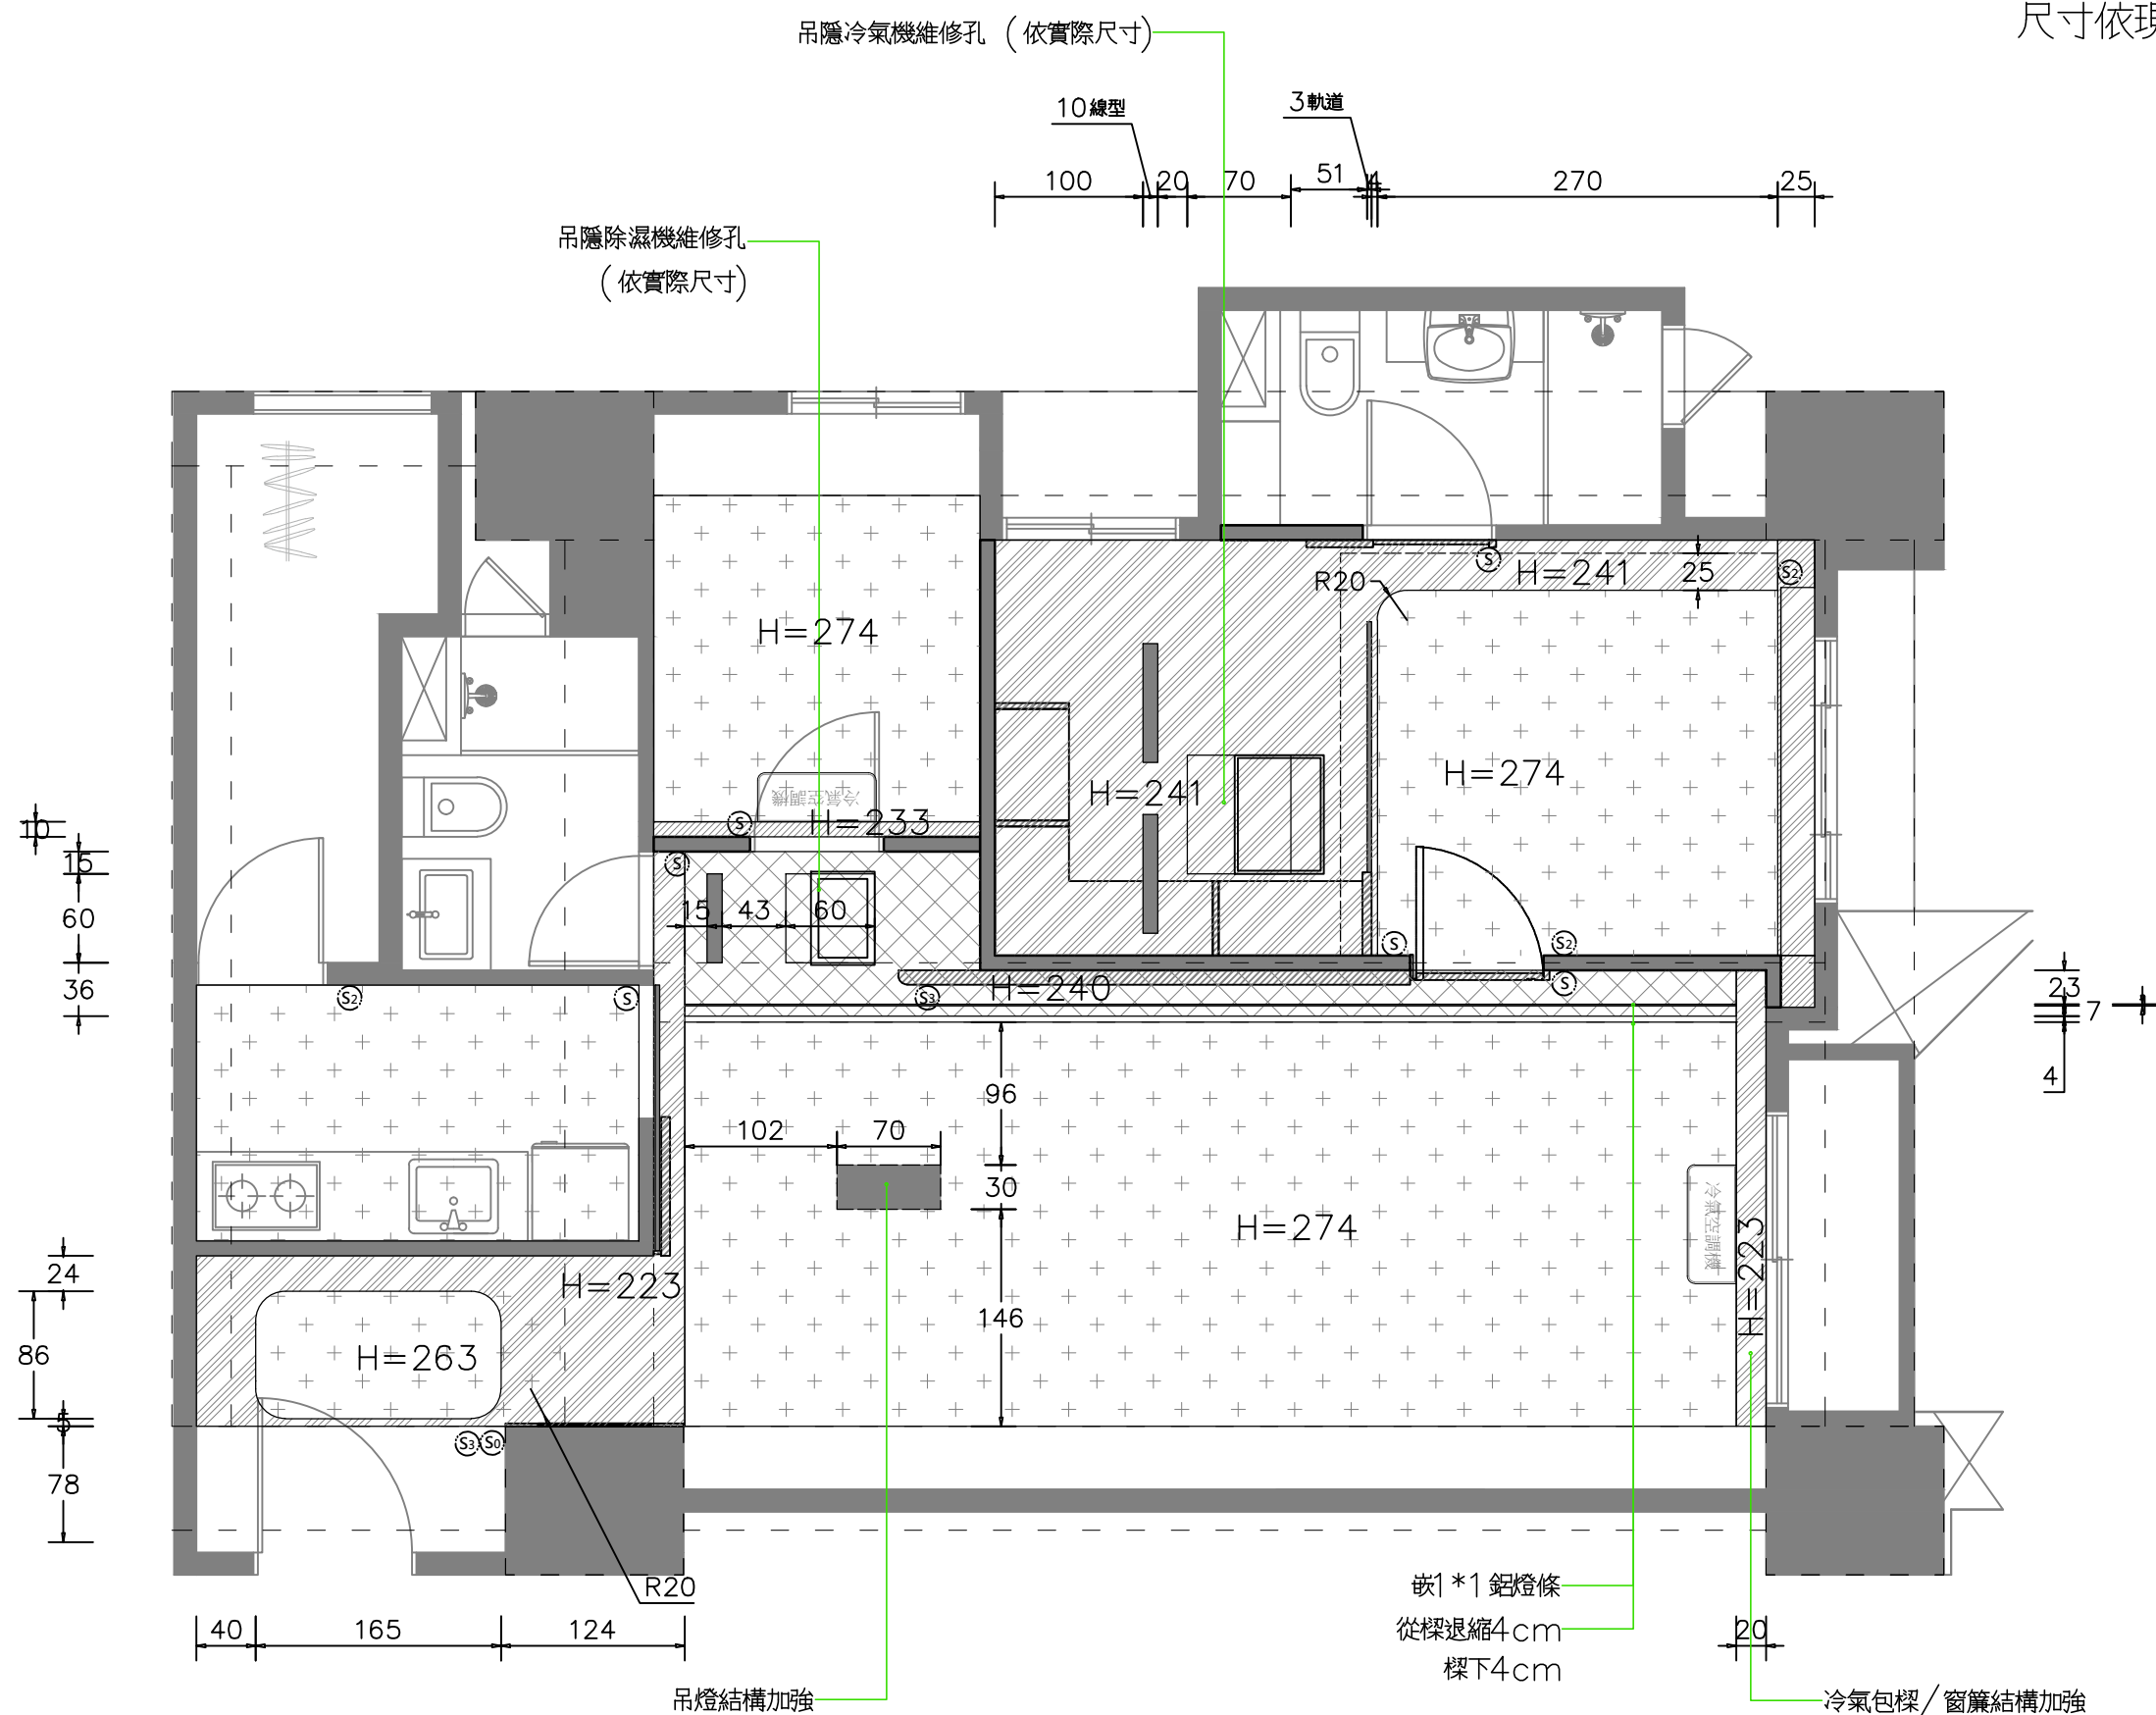

DRAW INTERIOR DESIGN

琢越空間設計

台中市臺灣大道二段285號31F

本圖內容

天花板圖

案名

大通大美7A6

設計

Alison

比例

1 / 50

日期

114.12.3

圖號

004

繪圖



Alison

單位

CM/公分

 出風出風口(側吹/下吹)

 迴風出風口(側吹/下吹)

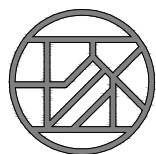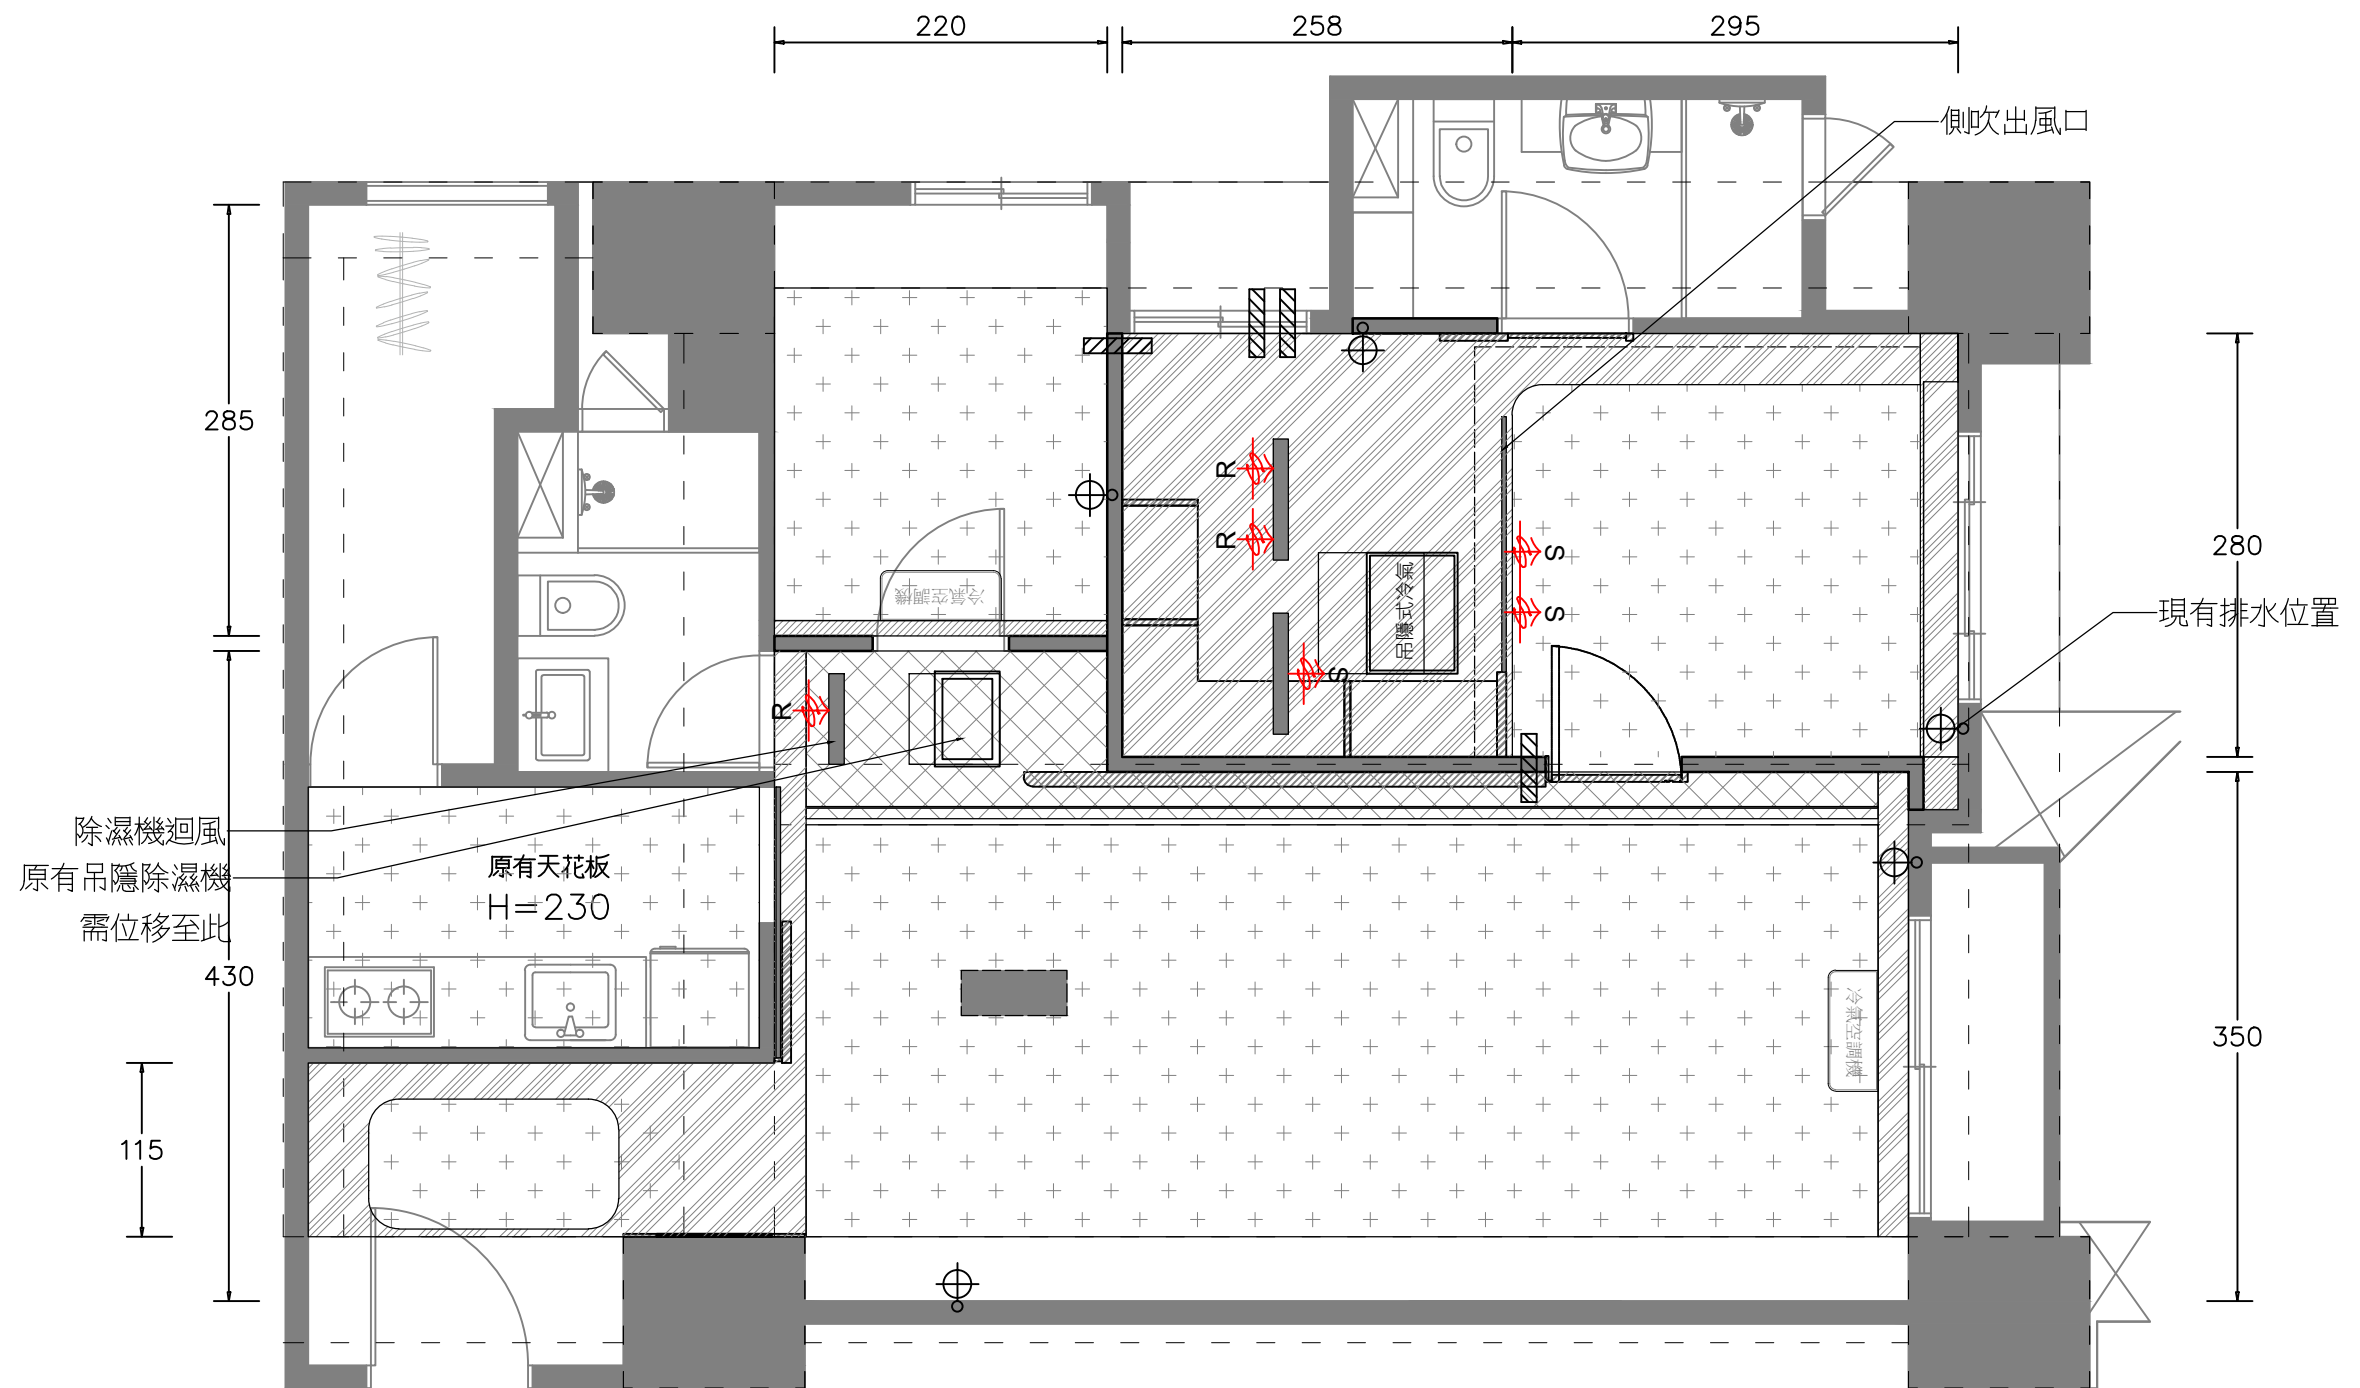

DRAW INTERIOR DESIGN 台中市臺灣大道二段285號31F

琢越空間設計

本圖內容

空調配置圖

設計

Alison

比例

1 / 50

日期

圖號

案名

大通大美7A6

繪圖

Alison

單位


CM/公分

114.12.3

005

符 號	說 明	備 註
s	開關燈切	
⊕	餐吊燈	燈具自備
⊗	15CM LED 嵌燈	自備智慧
==●==	T5 燈管	3000K
==✱==	LED燈條	3000K
⊗	5.5CM 櫃內燈	N
⊕	9 CM 投射燈	自備智慧
Ⓢ	偵煙感知器	延伸*4

尺寸依現場實際狀況為準

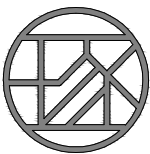



琢越空間設計

DRAW INTERIOR DESIGN 台中市臺灣大道二段285號31F

本圖內容	燈具配置圖	設計	Alison	比例	1 / 50	日期	
案名	大通大美7A6	繪圖	Alison	單位	CM/公分	114.12.3	圖號 006

符 號	說 明	備 註
s	開關燈切	
⊕	餐吊燈	燈具自備
⊗	15CM LED 嵌燈	自備智慧
==●==	T5 燈管	3000K
==✱==	LED燈條	3000K
⊗	5.5CM 櫃內燈	N
⊕	9 CM 投射燈	自備智慧
⊗	偵煙感知器	延伸*4

尺寸依現場實際狀況為準

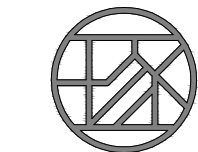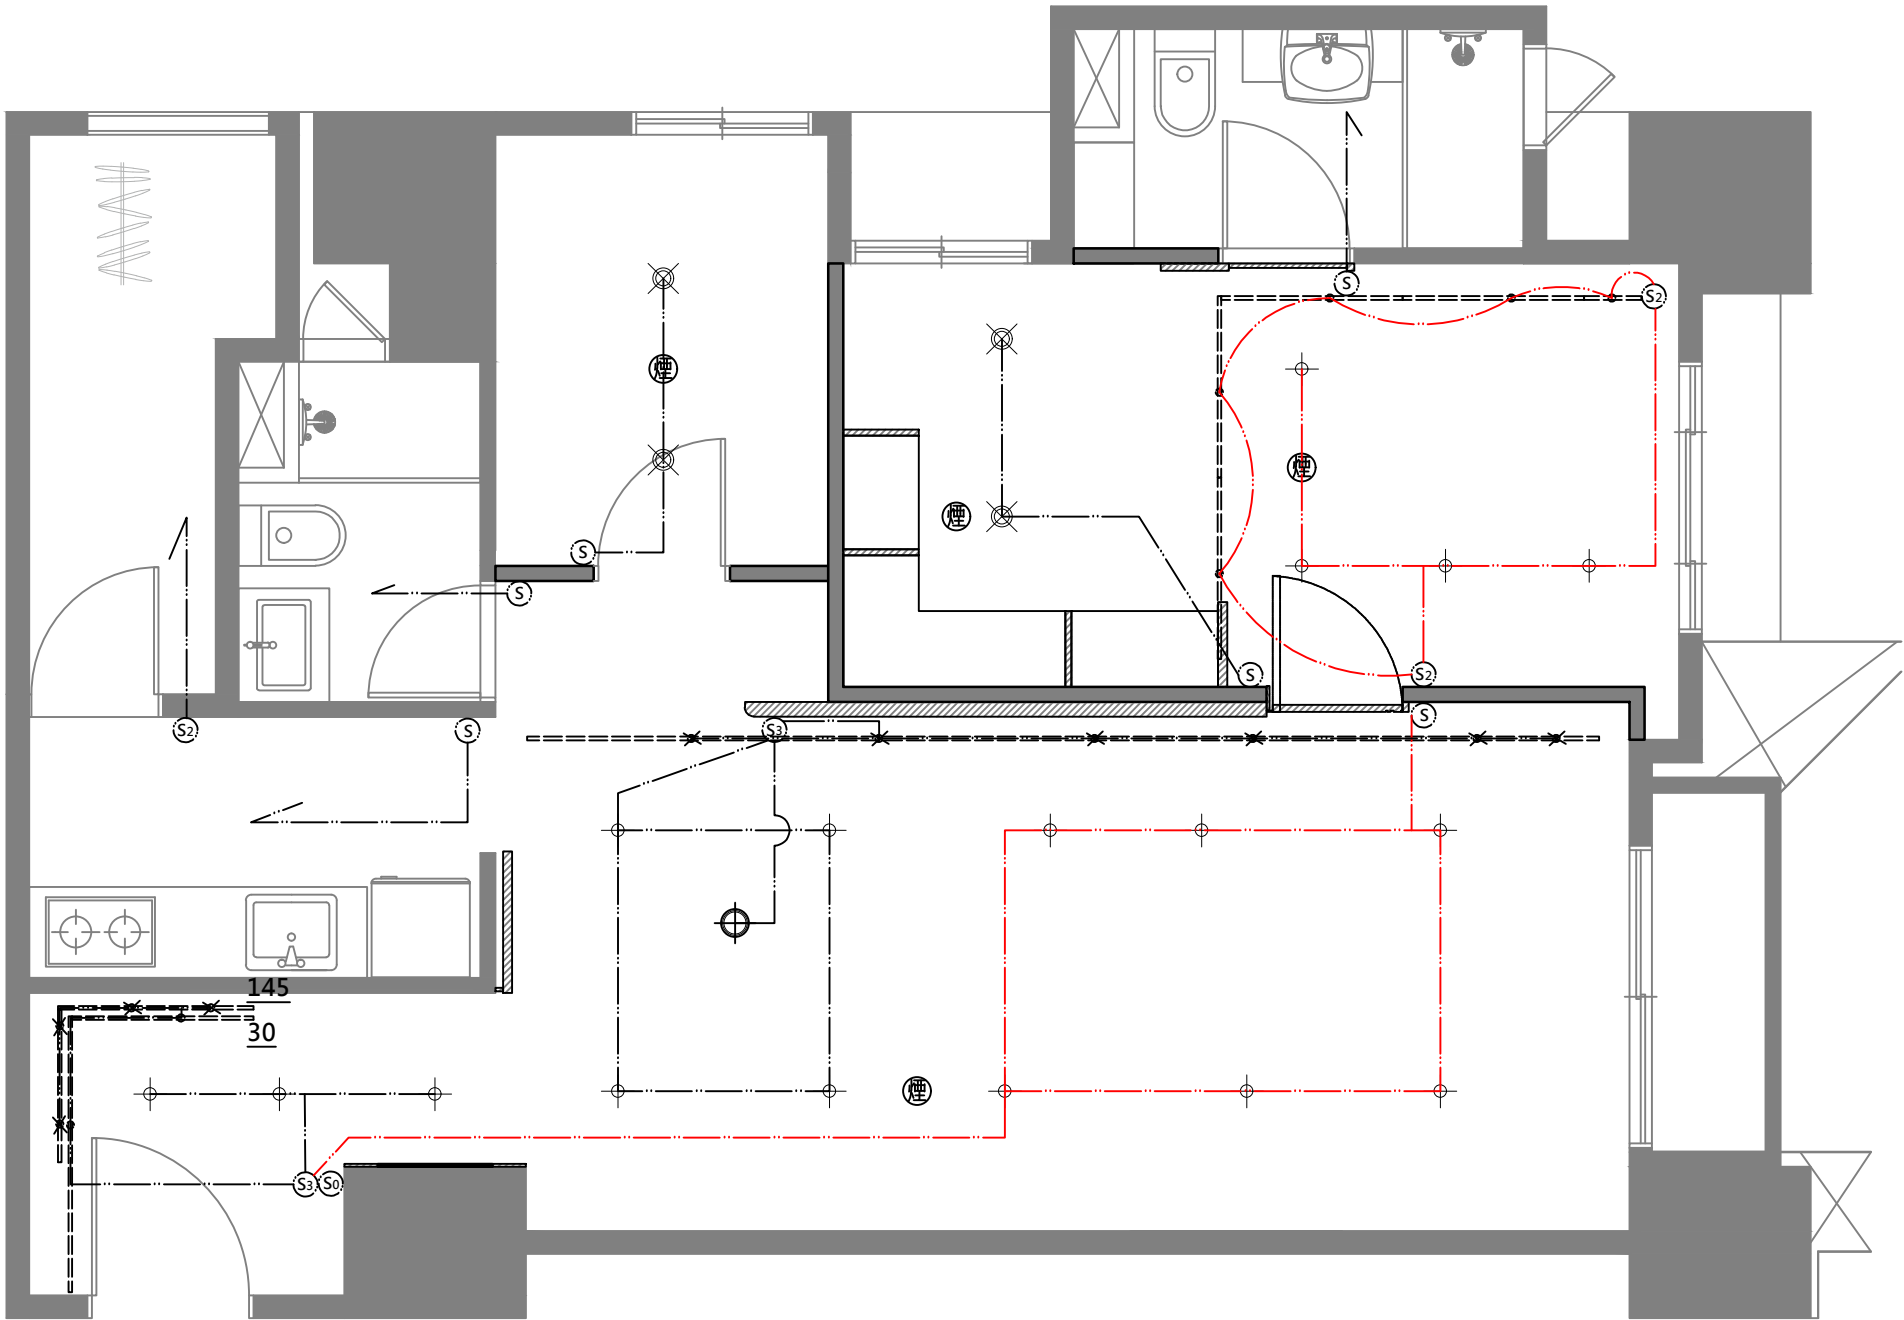

DRAW INTERIOR DESIGN

琢越空間設計

台中市臺灣大道二段285號31F

本圖內容

燈具迴路圖

案名

大通大美7A6

設計

Alison

比例

1 / 50

日期

114.12.3

圖號

007

繪圖

Alison



單位

CM/公分

符 號	說 明	備 註
Ⓛ	電源插座	
ⓉV	電視專線	
Ⓒ	網路專線	
ⓉEL	電話專線	
Ⓛ	專用插座	
對	對講機	原位嵌入
Ⓛ	原有插座	
Ⓛ	選樣面板	業主自備

尺寸依現場實際狀況為準

浴吊櫃修改
新增掃地機器人給排水

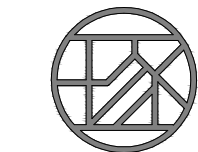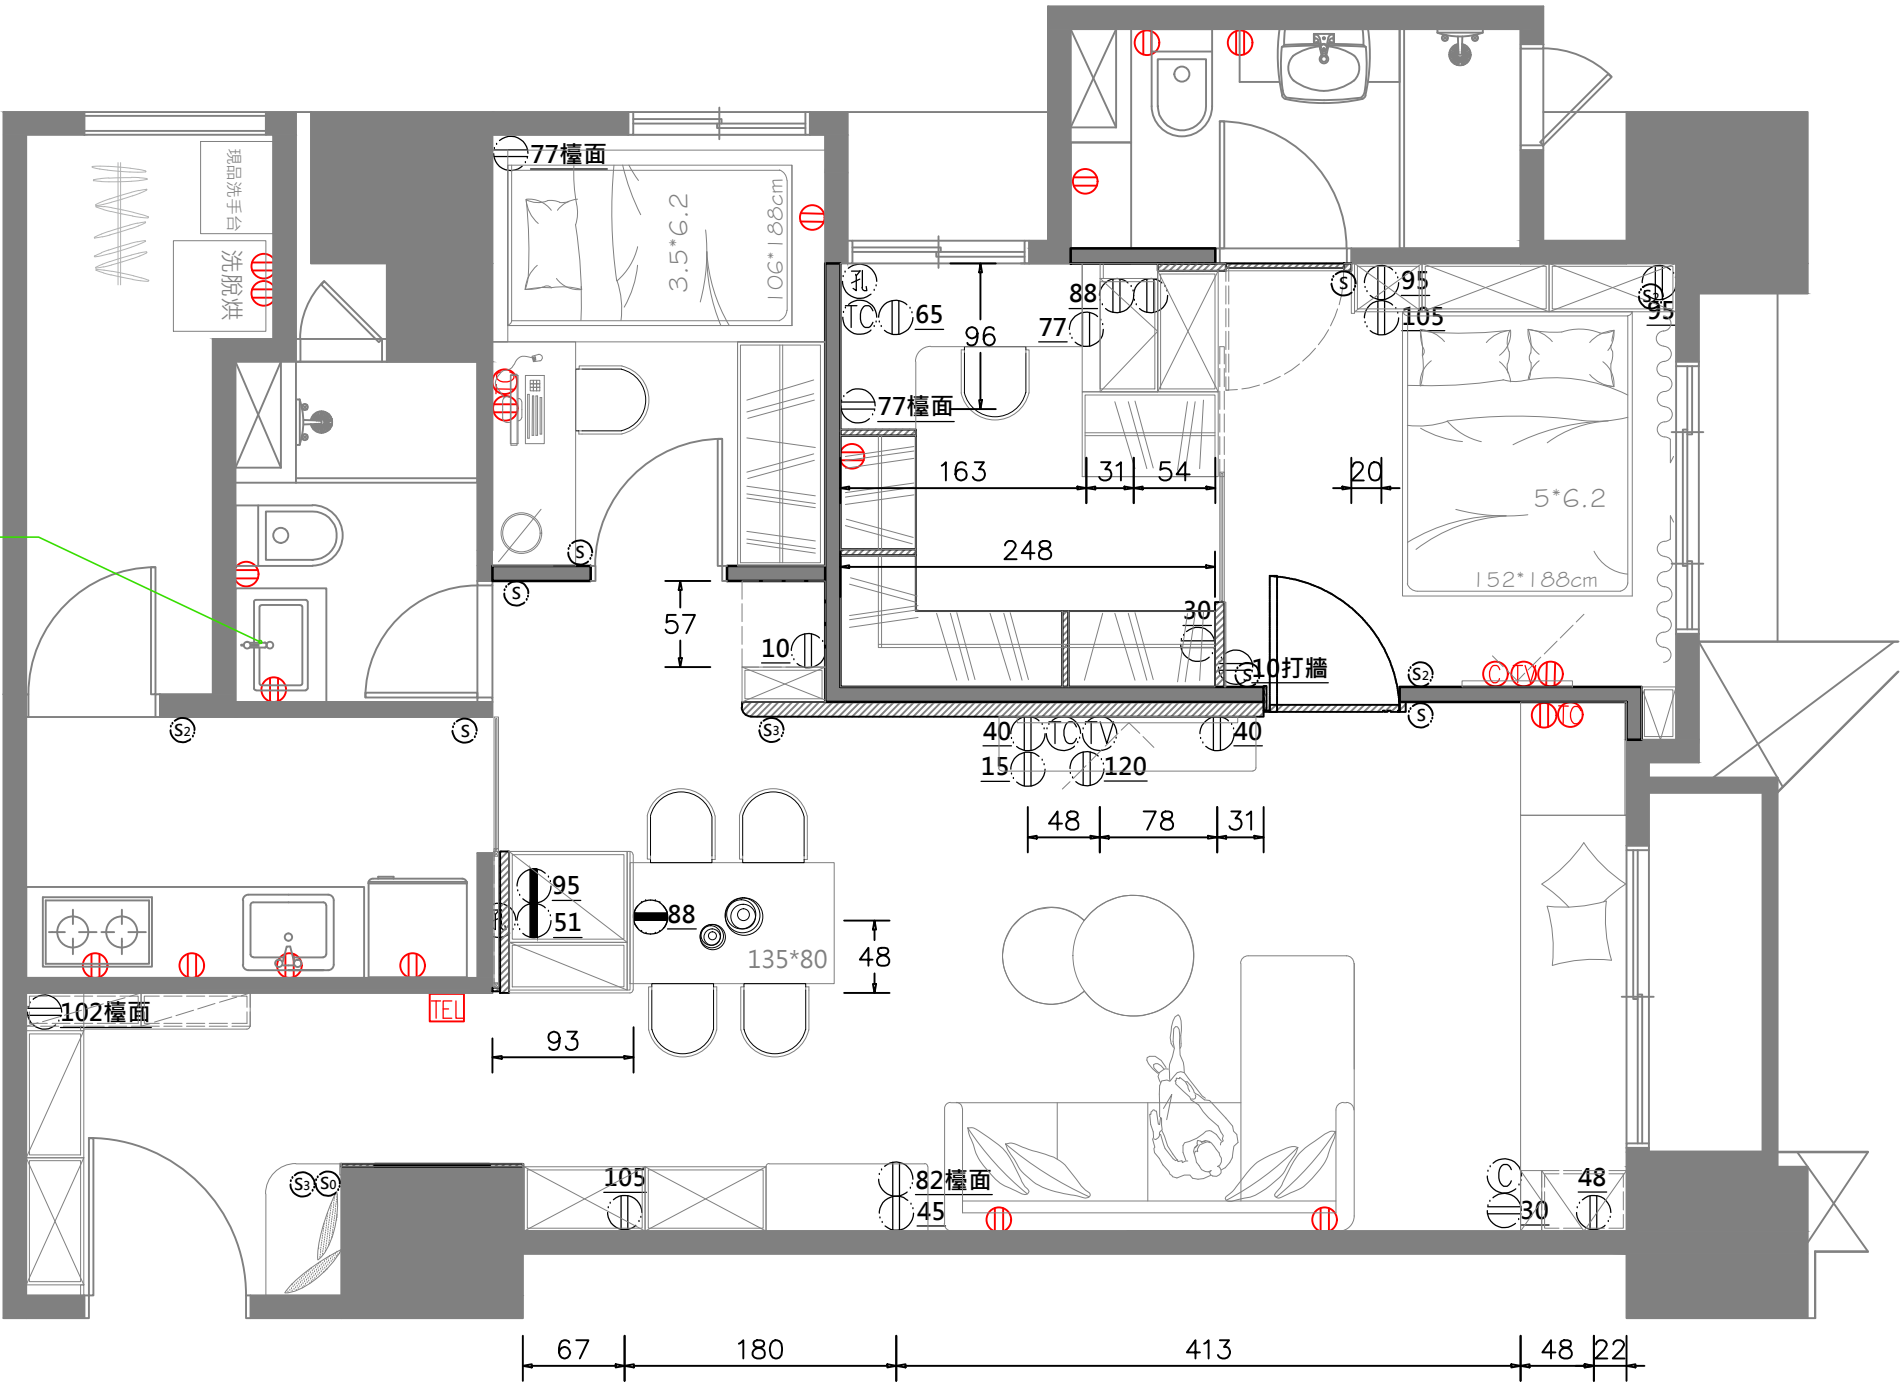

DRAW INTERIOR DESIGN

琢越空間設計

台中市臺灣大道二段285號31F

本圖內容

弱電配置圖

設計

Alison

比例

1 / 50

日期

圖號

案名

大通大美7A6

繪圖

Alison

單位

CM/公分






115.4.23

008

門片、抽頭、櫃體 W928 ST8
枱面、穿鞋椅全 H3165 ST12

系統櫃鉸鍊：TAI KE 油壓緩衝鉸鍊
抽屜滑軌：HQ 三節式油壓緩衝滑軌

尺寸依現場實際狀況為準

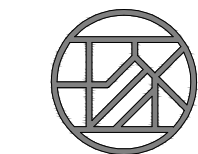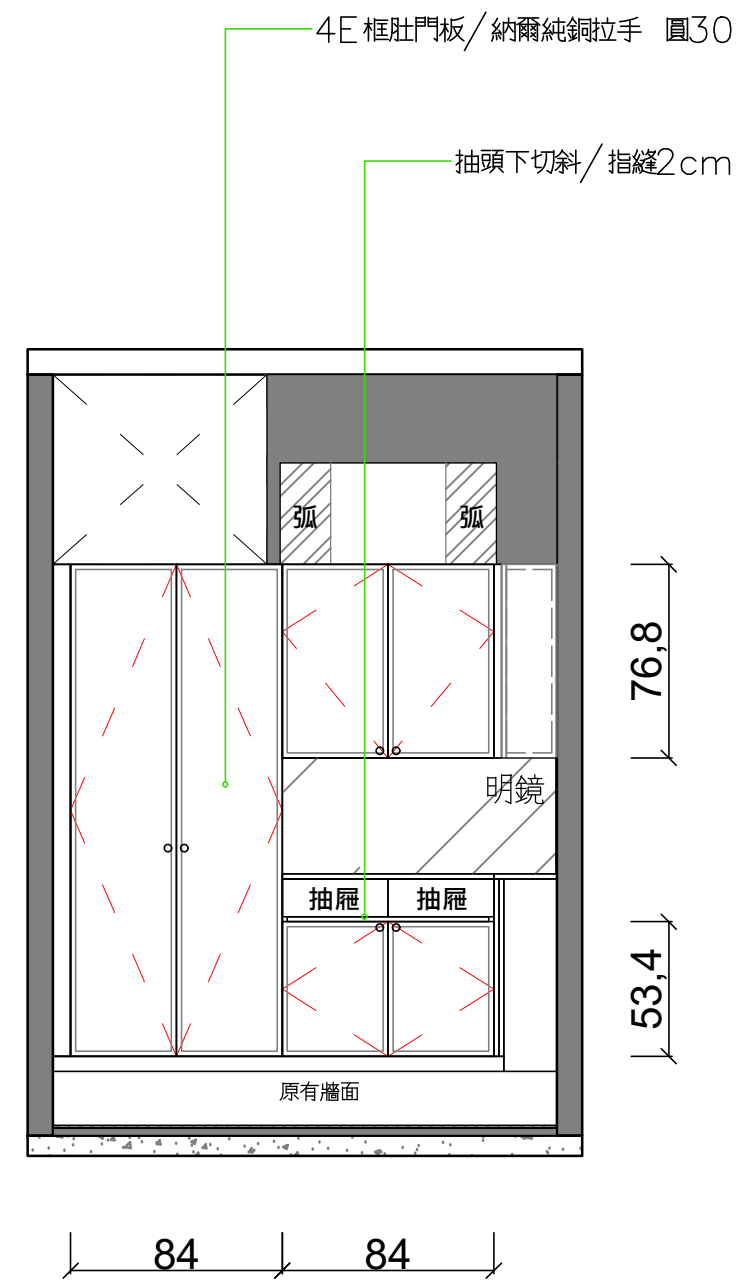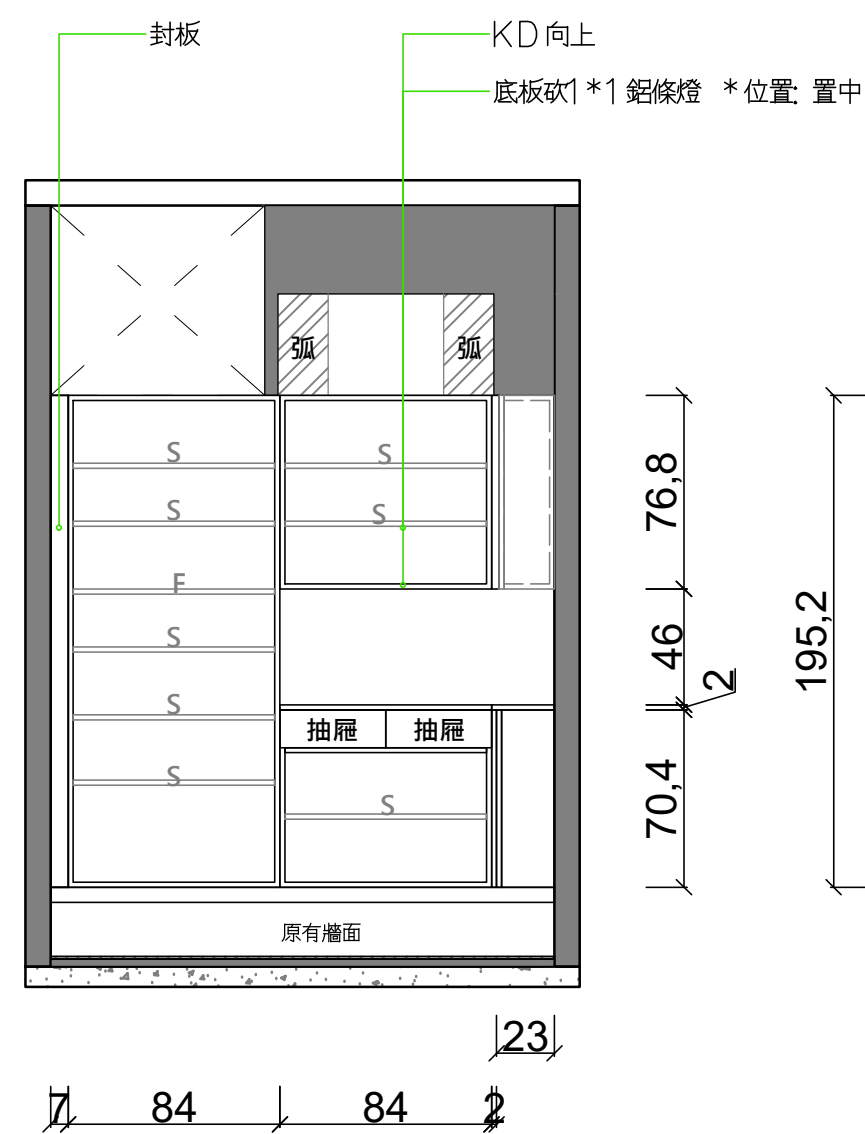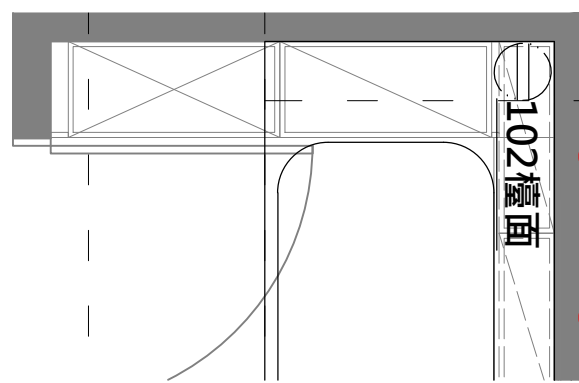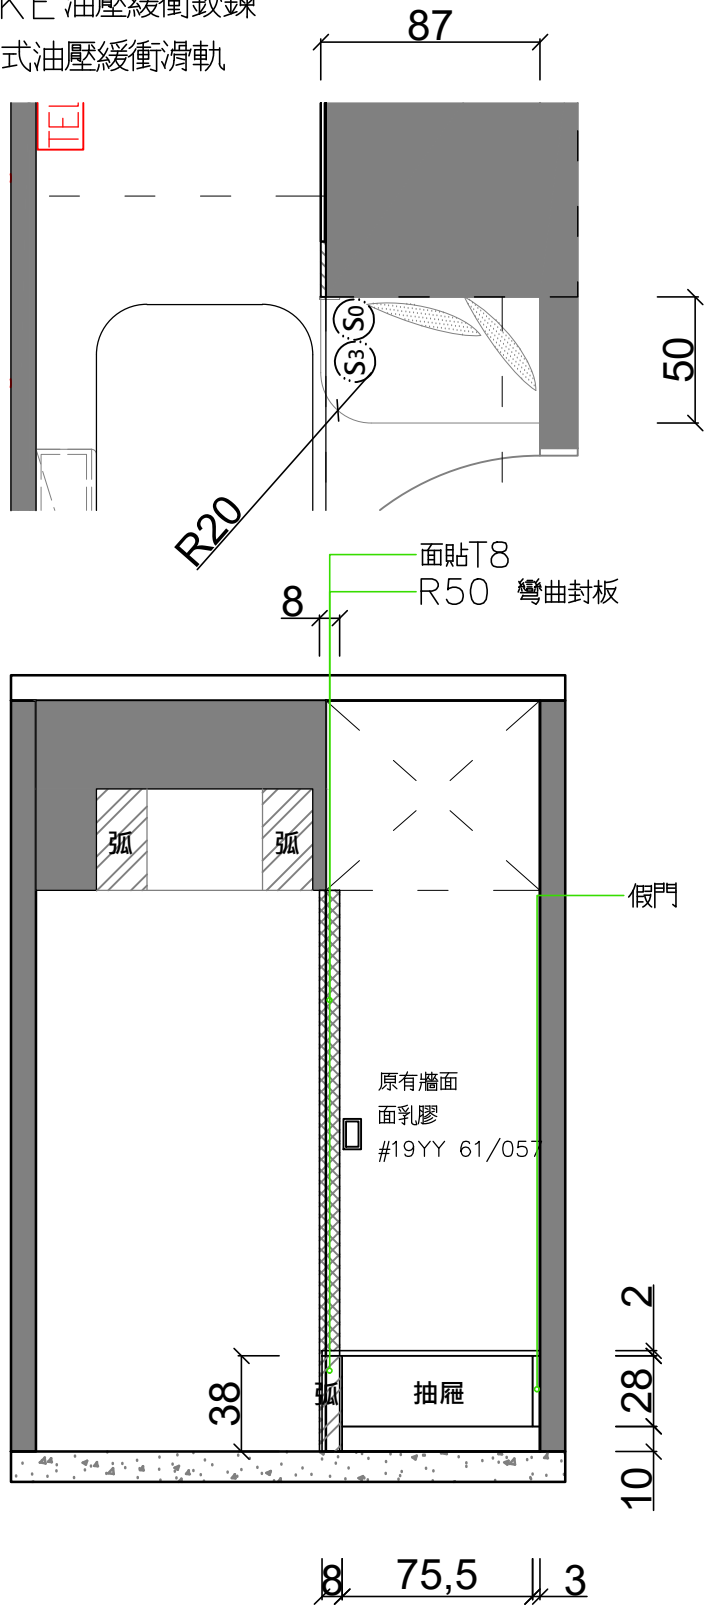

琢越空間設計



DRAW INTERIOR DESIGN 台中市臺灣大道二段285號31F

本圖內容	玄關穿鞋椅/鞋櫃	設計	Alison	比例	1 / 30	日期	
案名	大通大美7A6	繪圖	Alison	單位	CM/公分	115.7.1	圖號 01

門片、抽頭、櫃體 W928 ST8
枱面 H3165 ST12

系統櫃鉸鍊：TAI KE 油壓緩衝鉸鍊
抽屜滑軌：HQ 三節式油壓緩衝滑軌

尺寸依現場實際狀況為準

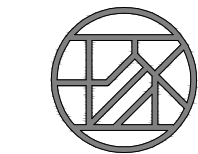
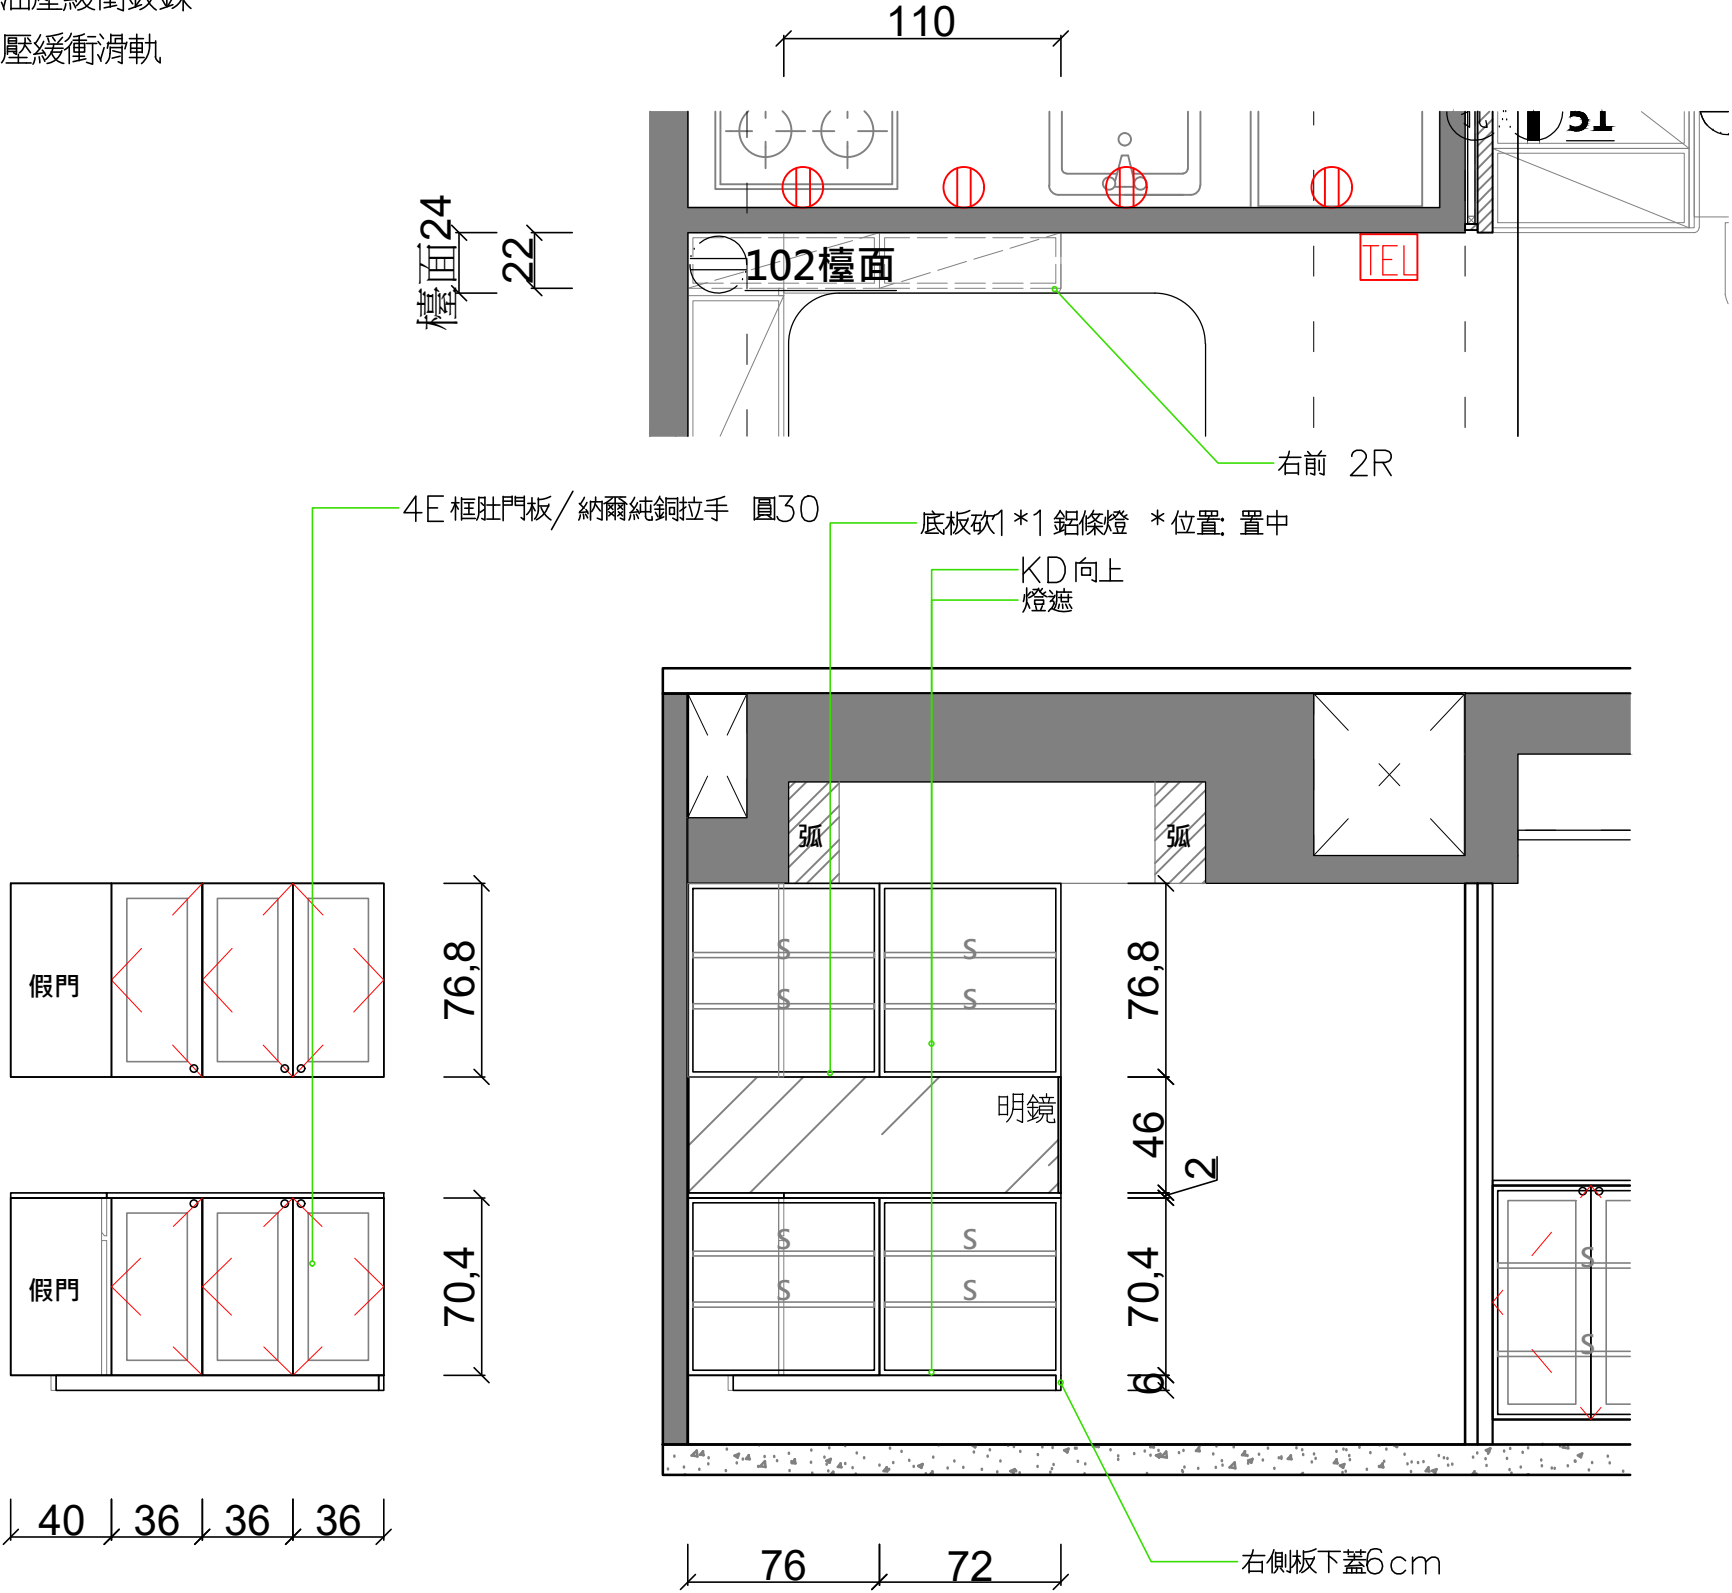


DRAW INTERIOR DESIGN 台中市臺灣大道二段285號31F

琢越空間設計

本圖內容	玄關正面鞋櫃	設計	Alison	比例	1 / 30	日期		圖號	
案名	大通大美7A6	繪圖	Alison	單位	CM/公分	115.7.1		02	

尺寸依現場實際狀況為準

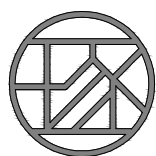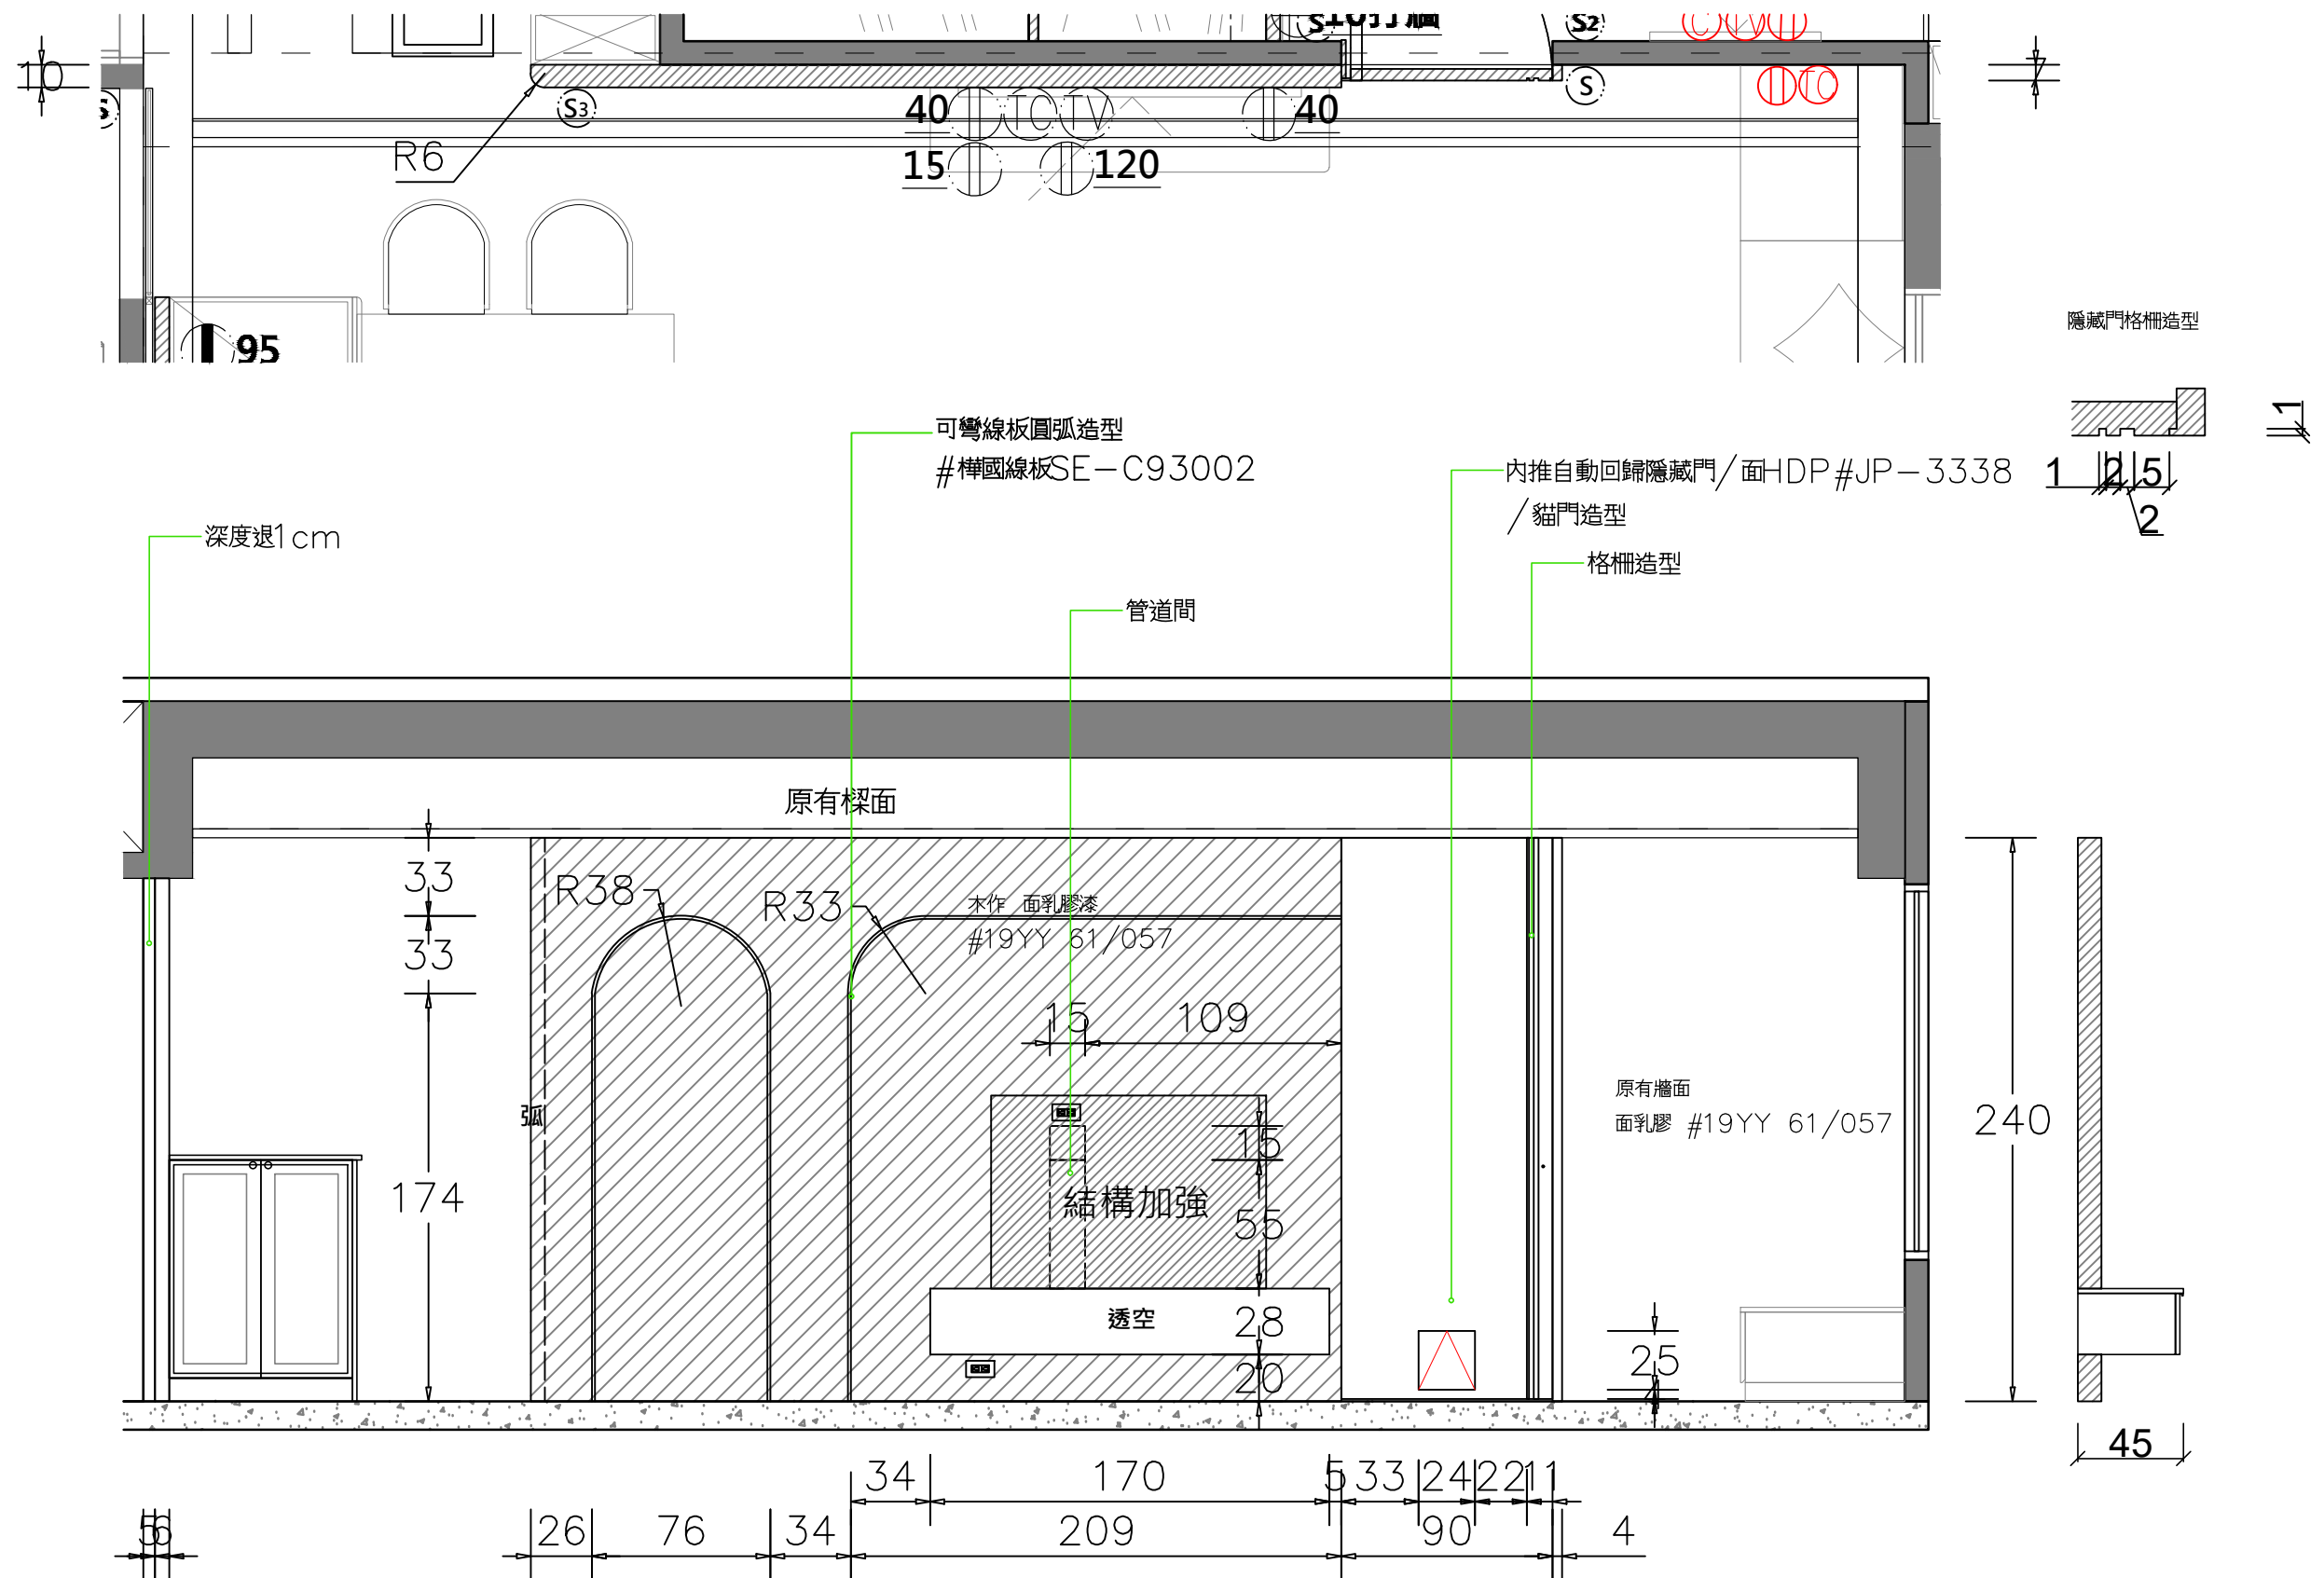



琢越空間設計

DRAW INTERIOR DESIGN 台中市臺灣大道二段285號31F

本圖內容	電視牆木作	設計	Alison	比例	1 / 30	日期		圖號	
案名	大通大美7A6	繪圖	Alison	單位	CM/公分	115.7.1		1	

櫃體 W928 ST9
櫃體 H3165 ST12

系統櫃鉸鍊：TAI KE 油壓緩衝鉸鍊
抽屜滑軌：HQ 三節式油壓緩衝滑軌

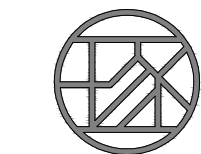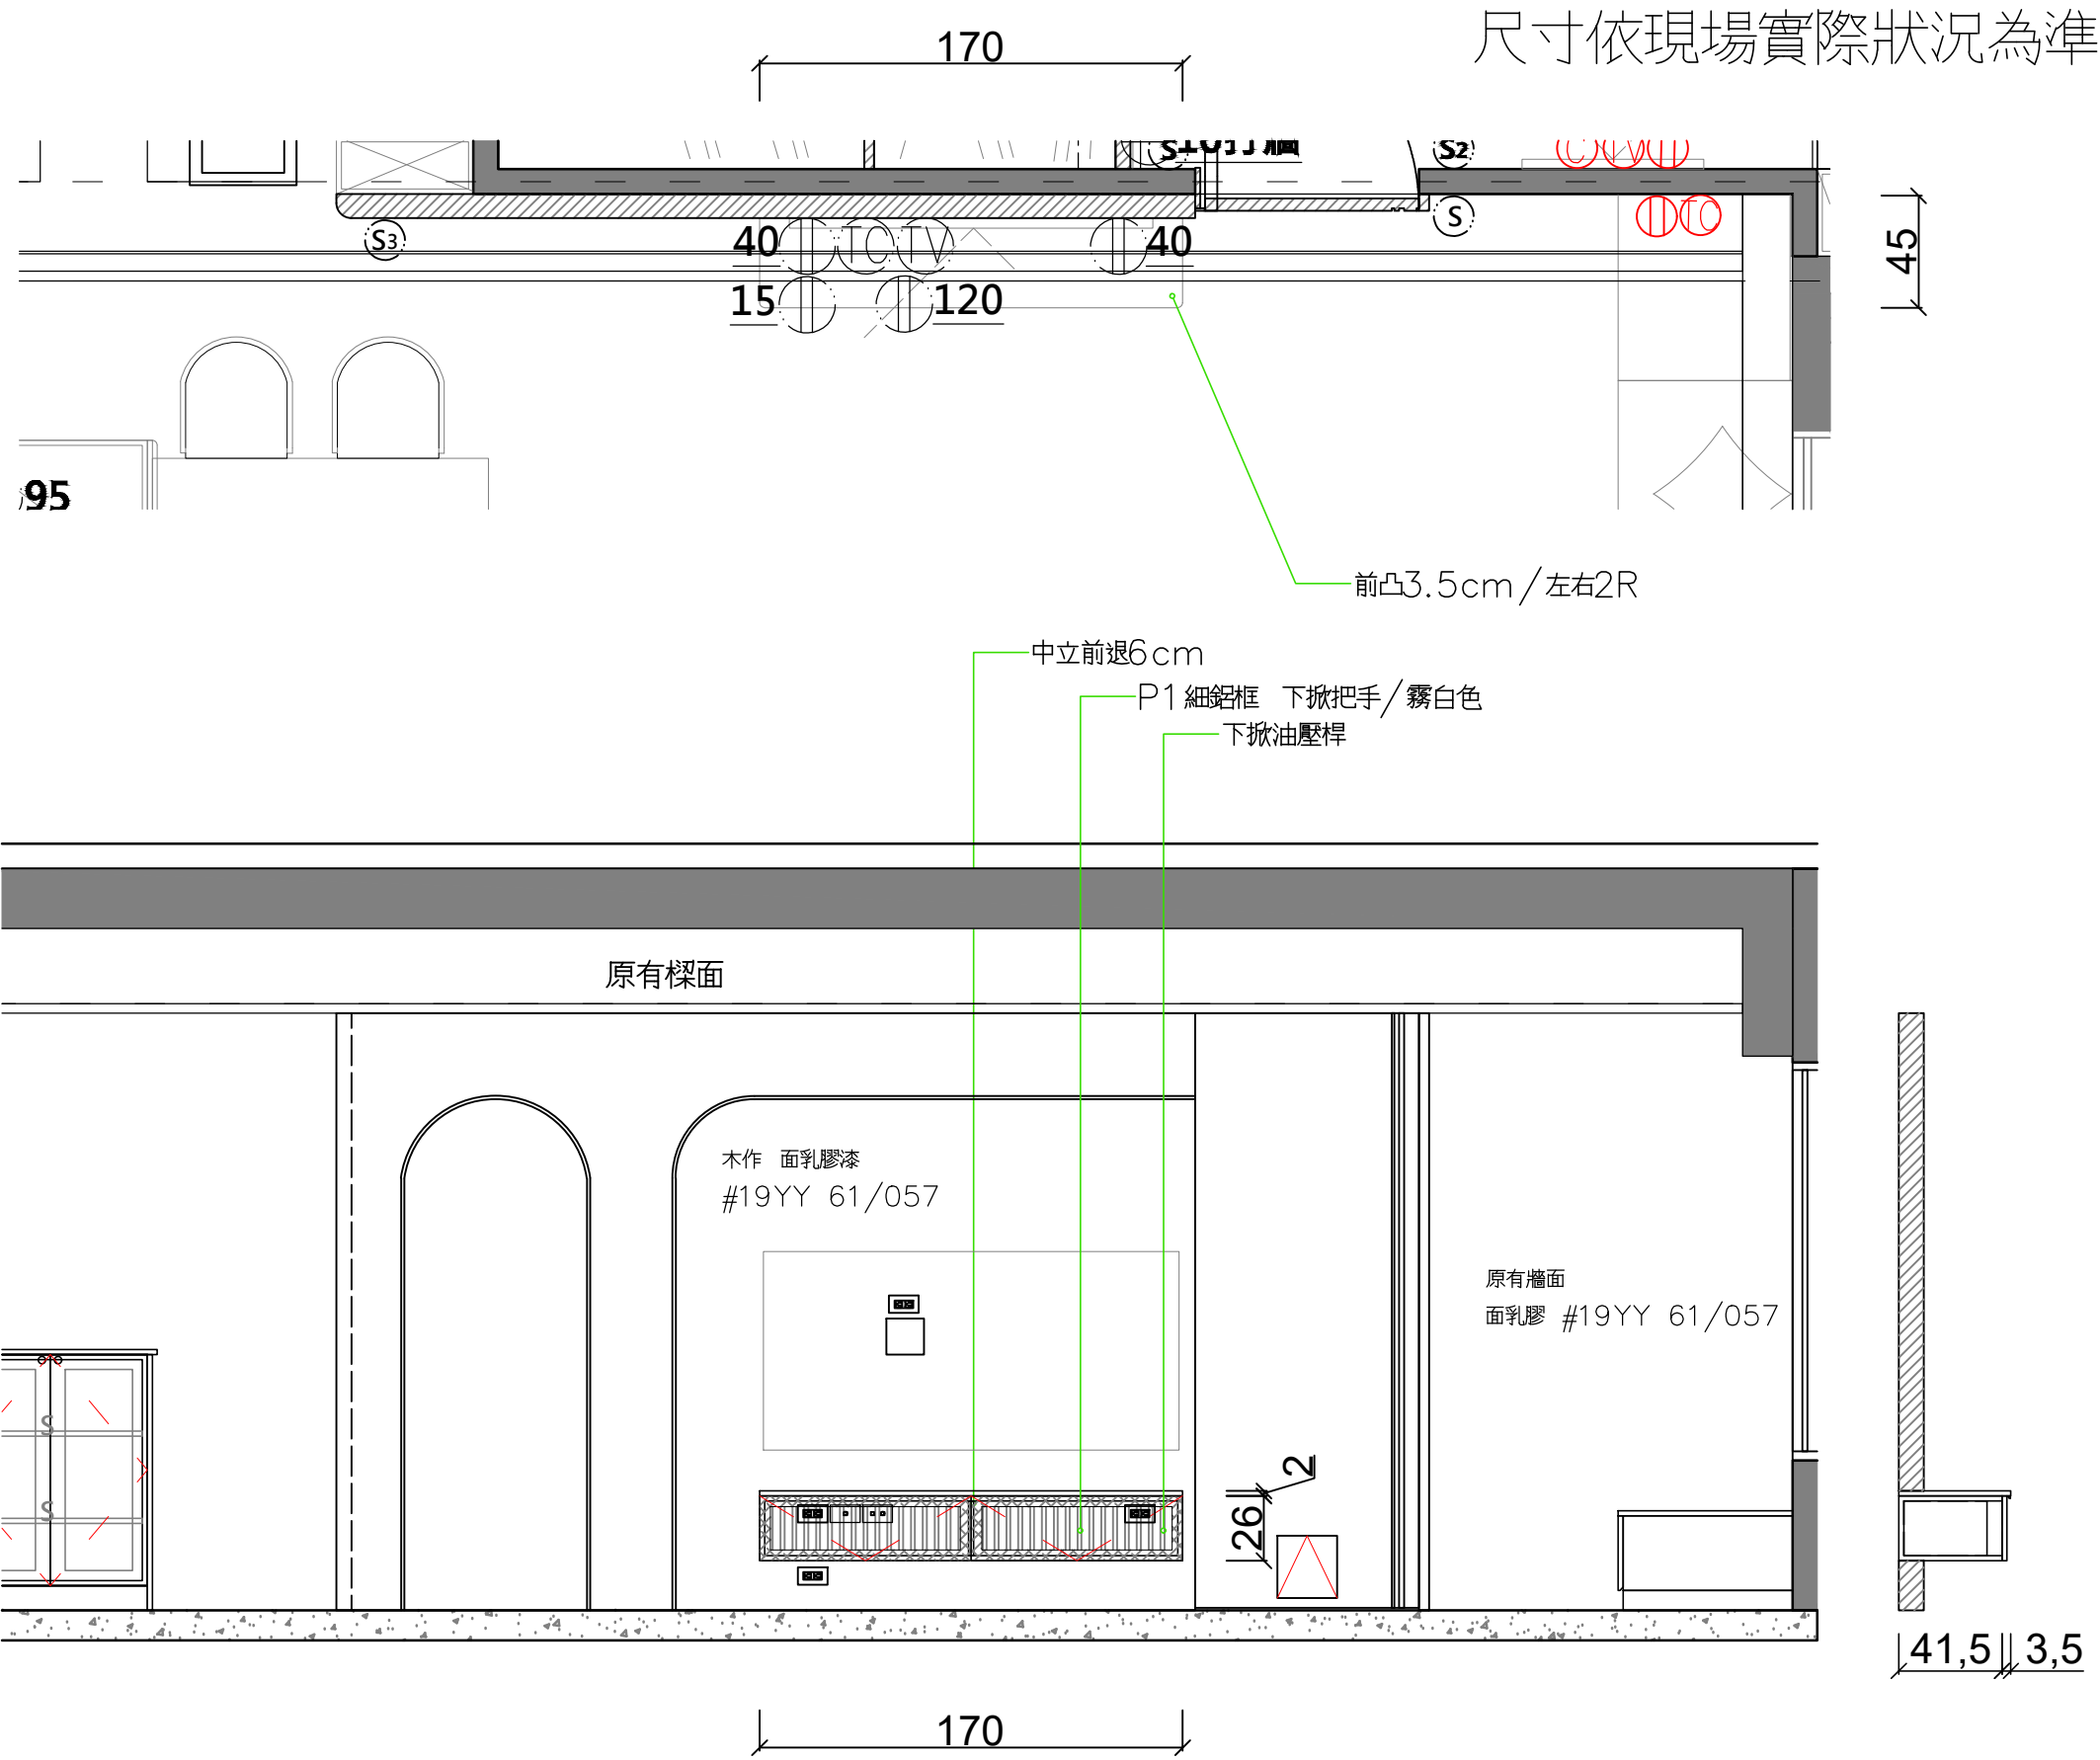

琢越空間設計

DRAW INTERIOR DESIGN 台中市臺灣大道二段285號31F

本圖內容	電視牆	設計	Alison	比例	1 / 30	日期	
案名	大通大美7A6	繪圖	Alison	單位	CM/公分	115.7.1	圖號 03

系統櫃鉸鍊：TAI KE 油壓緩衝鉸鍊
抽屜滑軌：HQ 三節式油壓緩衝滑軌

Technical drawing of a sliding door system. The drawing shows a top-down view of the door assembly. Key dimensions include a total width of 275 and a segment width of 75. The door height is 70, with a 14 offset at the bottom. A 30 offset is shown on the right side. A 48 offset is also indicated. A red circle with 'S' is located on the left side. A label '冷氣空調機' (Air Conditioning Unit) is positioned in the center. The bottom right corner specifies '8mm 清玻門片 / 緩衝玻璃鉸鍊' (8mm Clear Glass Door Panel / Buffer Glass Hinge).




DRAW INTERIOR DESIGN 台中市臺灣大道二段285號31F

本圖內容	客廳臥榻區	設計	Alison	比例	1 / 30	日期	圖號
案名	大通大美7A6	繪圖	Alison	單位	CM/公分	115.7.1	04

門片、抽頭、美背 U705 ST9
櫃體、枱面、電視櫃全 H3165 ST12
電視櫃枱面跳色 U705 ST9

系統櫃鉸鍊：TAI KE 油壓緩衝鉸鍊
抽屜滑軌：HQ 三節式油壓緩衝滑軌

尺寸依現場實際狀況為準

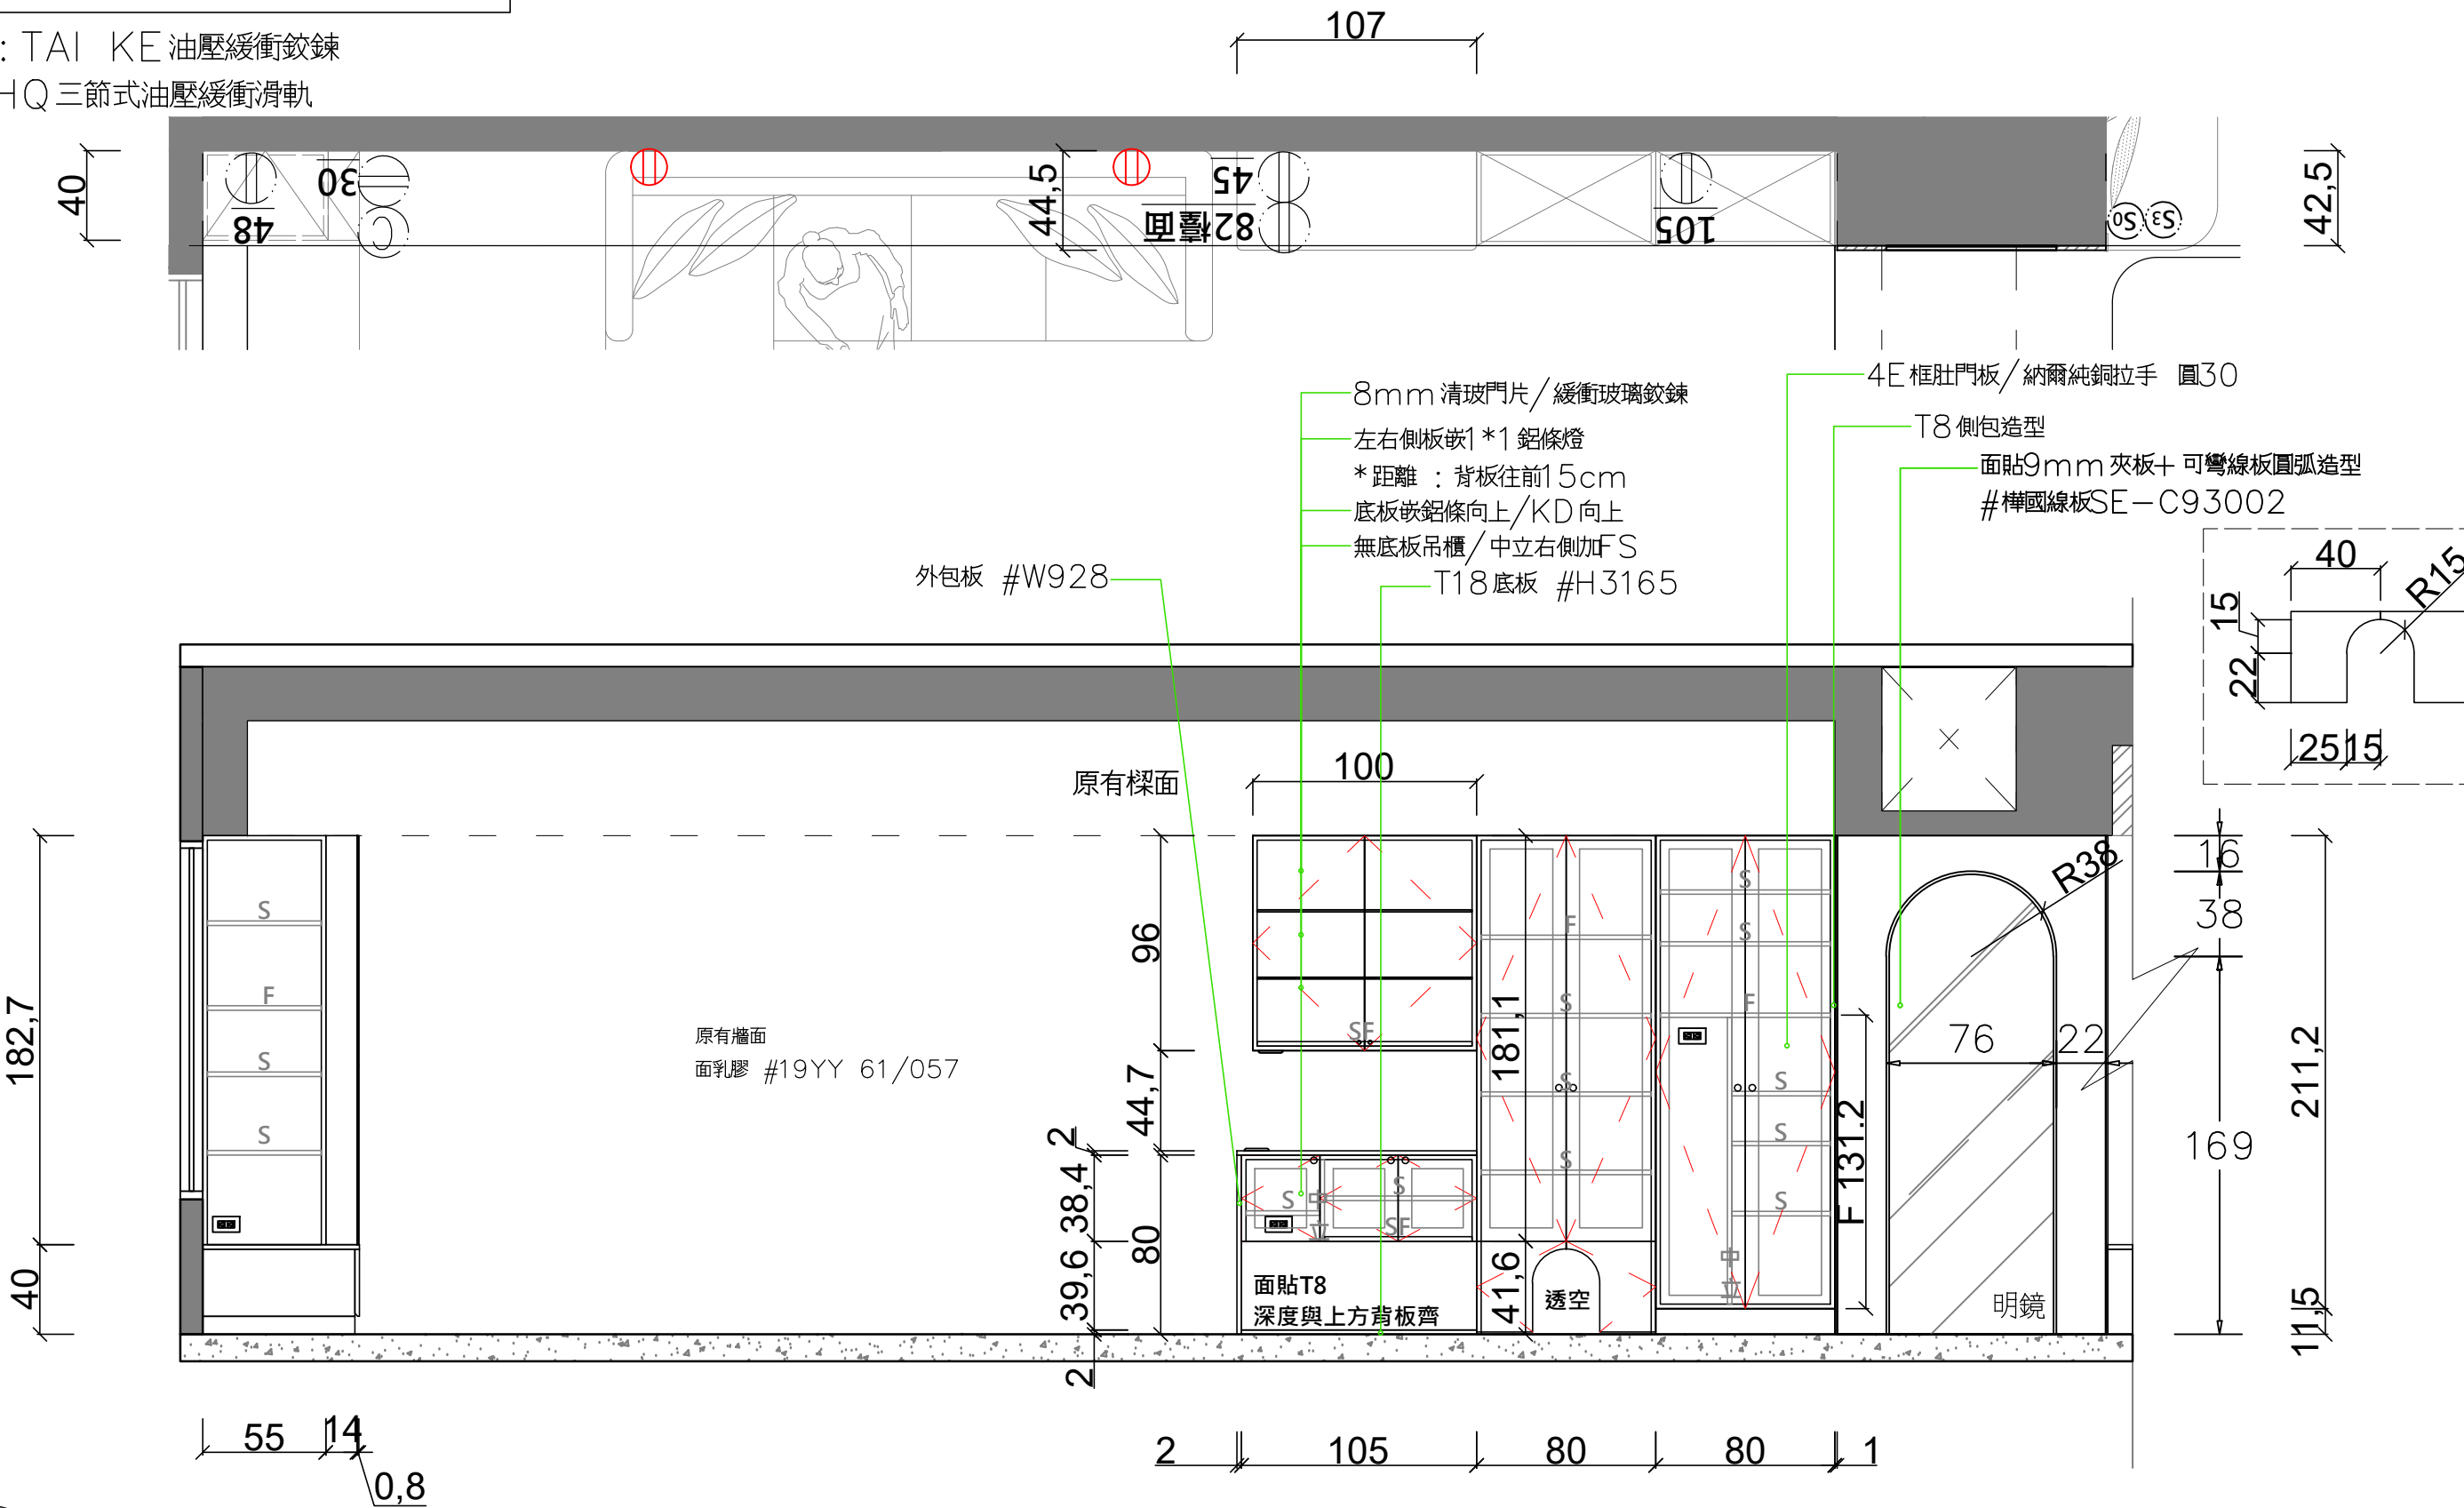








琢越空間設計

DRAW INTERIOR DESIGN 台中市臺灣大道二段285號31F

本圖內容	客廳背牆收納櫃	設計	Alison	比例	1 / 30	日期		圖號	
案名	大通大美7A6	繪圖	Alison	單位	CM/公分	115.7.1		05	

枱面 U705 ST9
櫃體，電器櫃全，美背 H3165 ST12
4E 框門板 W928 ST9

系統櫃鉸鍊：TAI KE 油壓緩衝鉸鍊
抽屜滑軌：HQ 三節式油壓緩衝滑軌

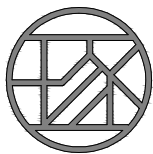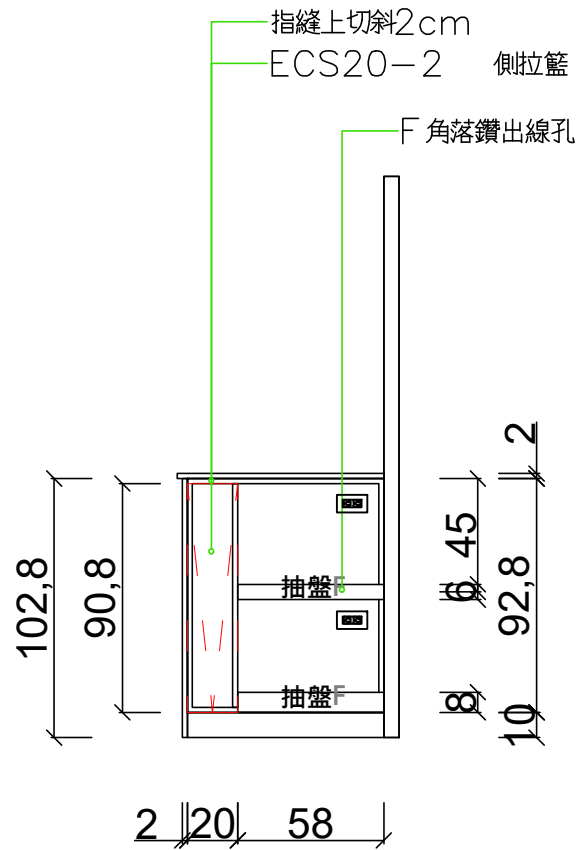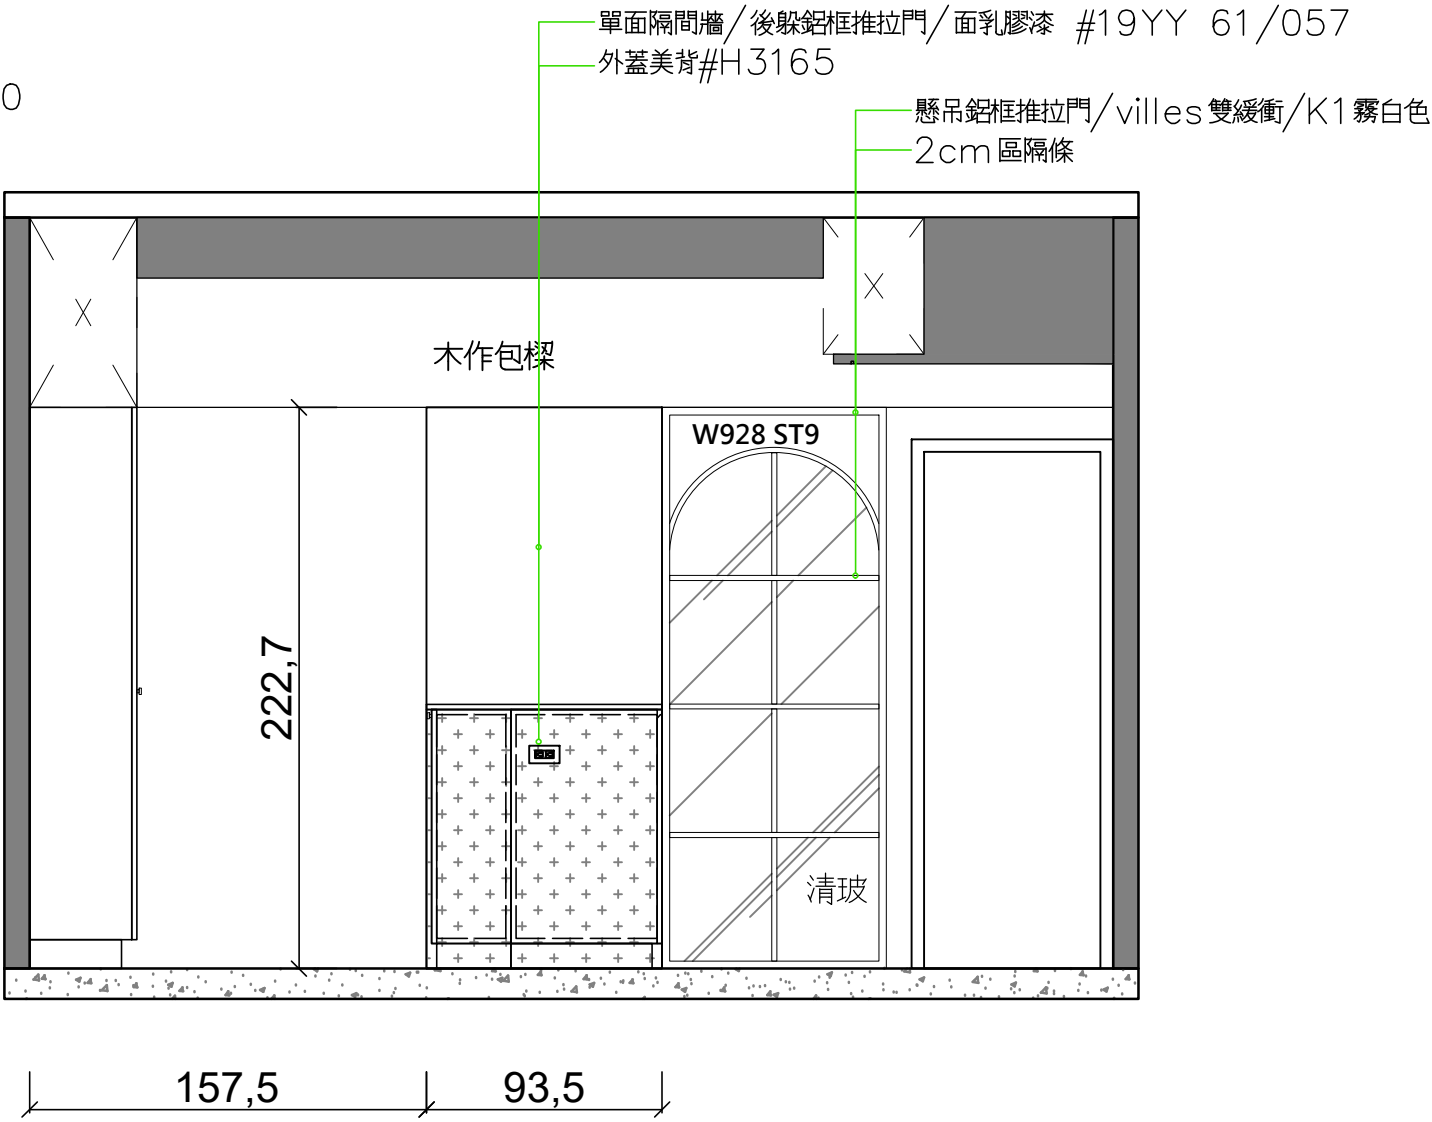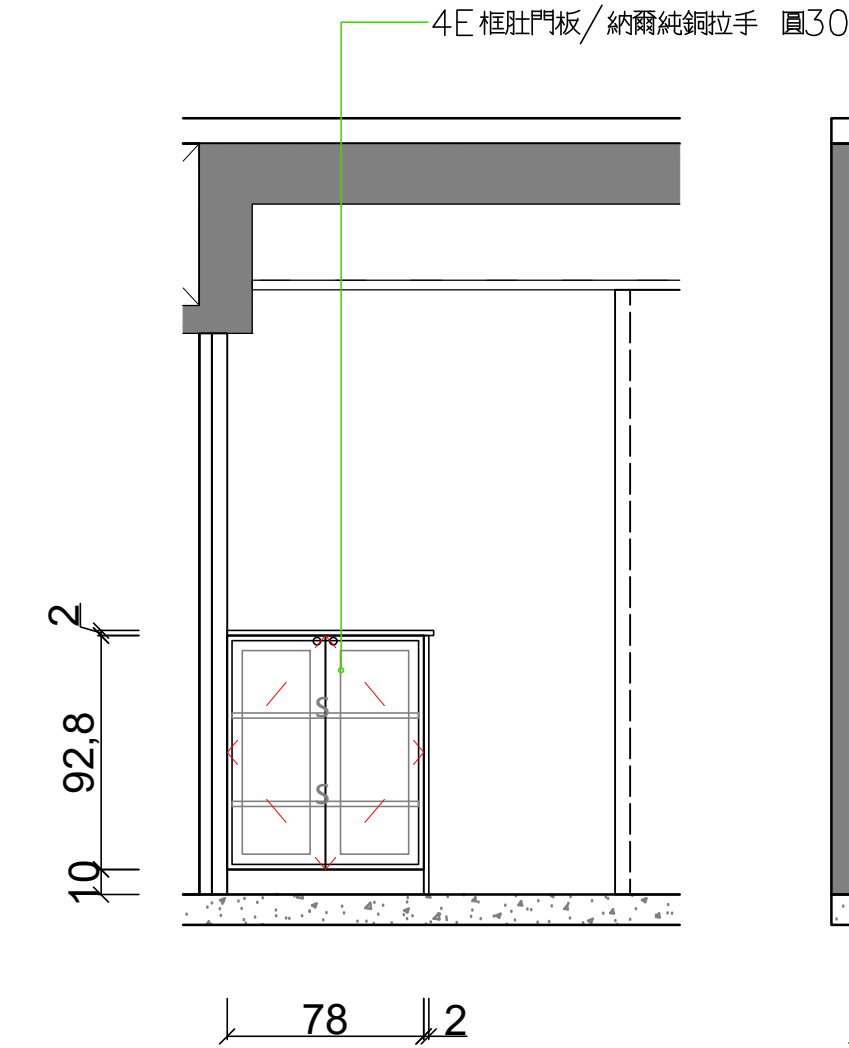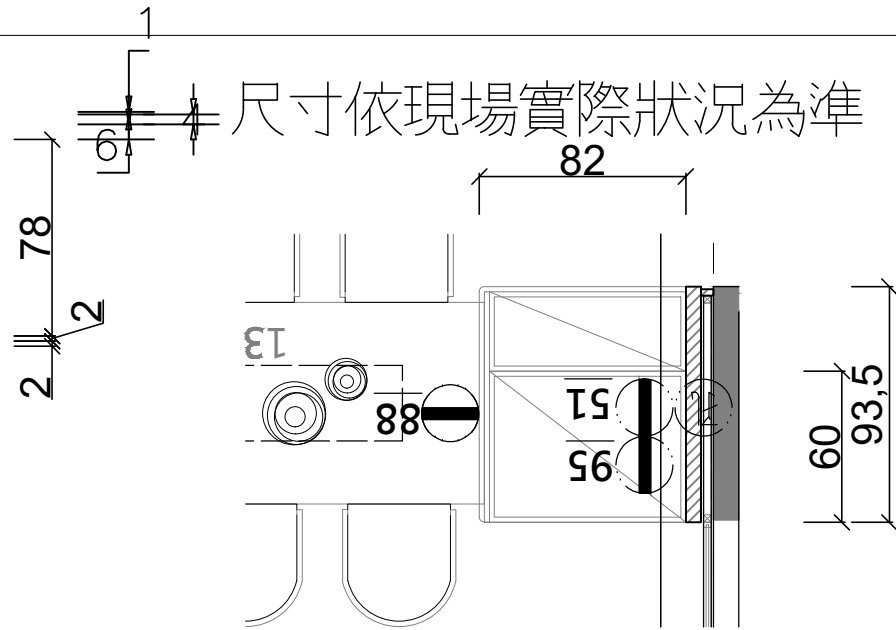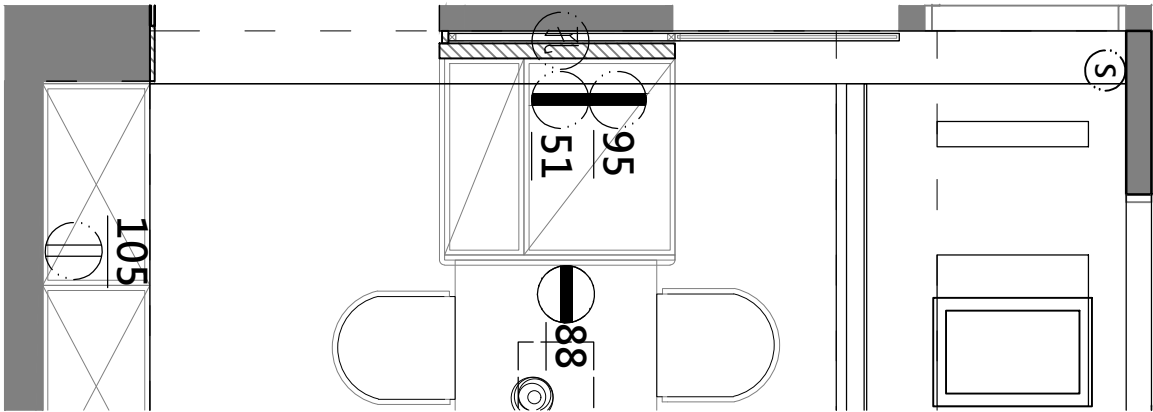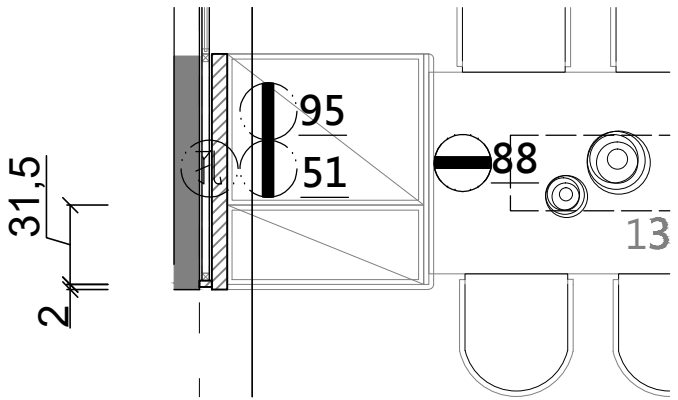

琢越空間設計




DRAW INTERIOR DESIGN 台中市臺灣大道二段285號31F

本圖內容	餐邊櫃	設計	Alison	比例	1 / 30	日期		圖號	
案名	大通大美7A6	繪圖	Alison	單位	CM/公分	115.7.1		06	

門片 W928 ST9
櫃體 H3165 ST12

系統櫃鉸鍊：TAI KE 油壓緩衝鉸鍊
抽屜滑軌：HQ 三節式油壓緩衝滑軌

尺寸依現場實際狀況為準

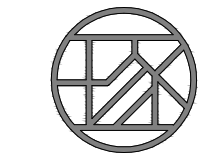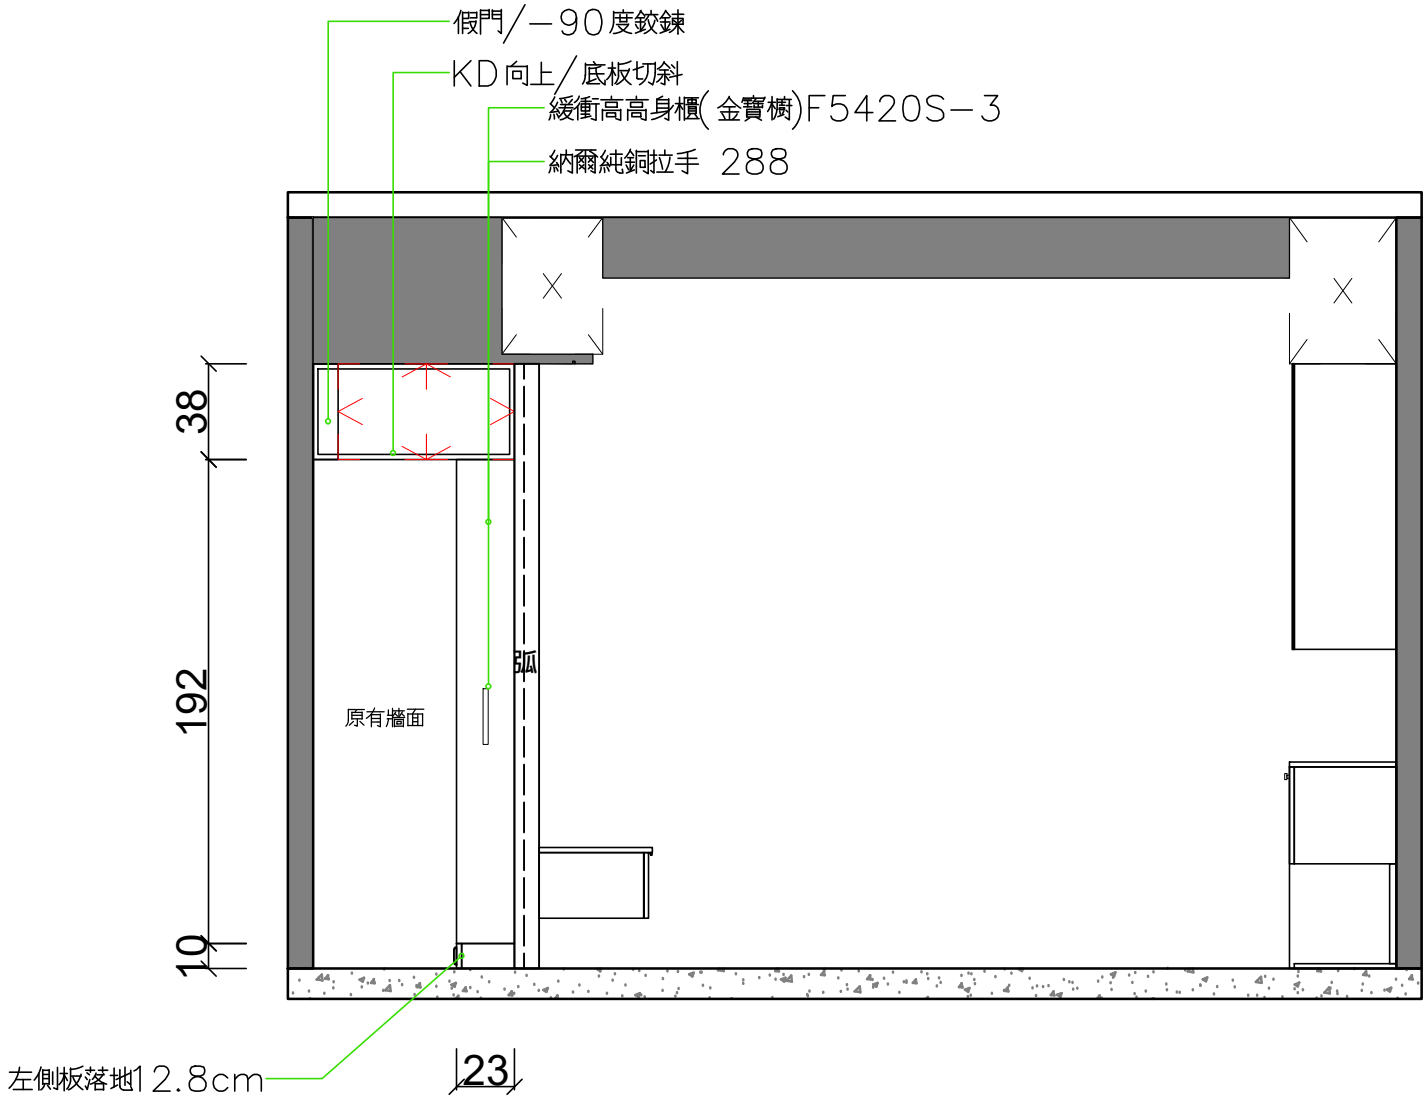
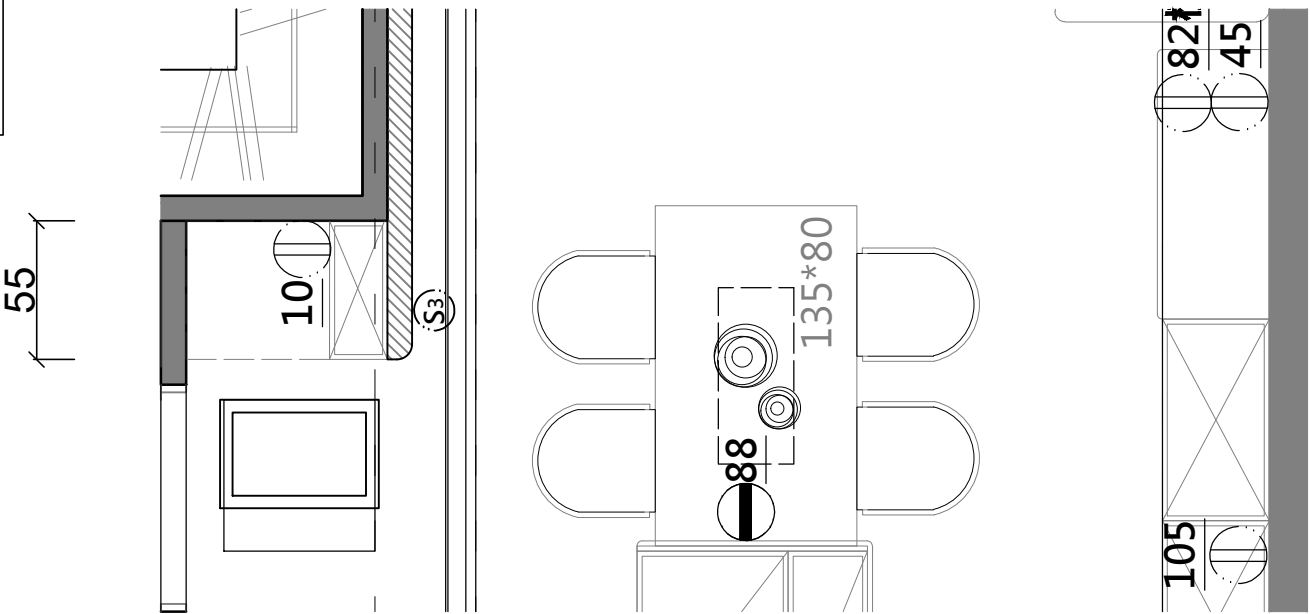


DRAW INTERIOR DESIGN 台中市臺灣大道二段285號31F

琢越空間設計

本圖內容	餐廳高身櫃	設計	Alison	比例	1 / 30	日期	
案名	大通大美7A6	繪圖	Alison	單位	CM/公分	115.7.1	圖號 07

尺寸依現場實際狀況為準

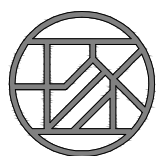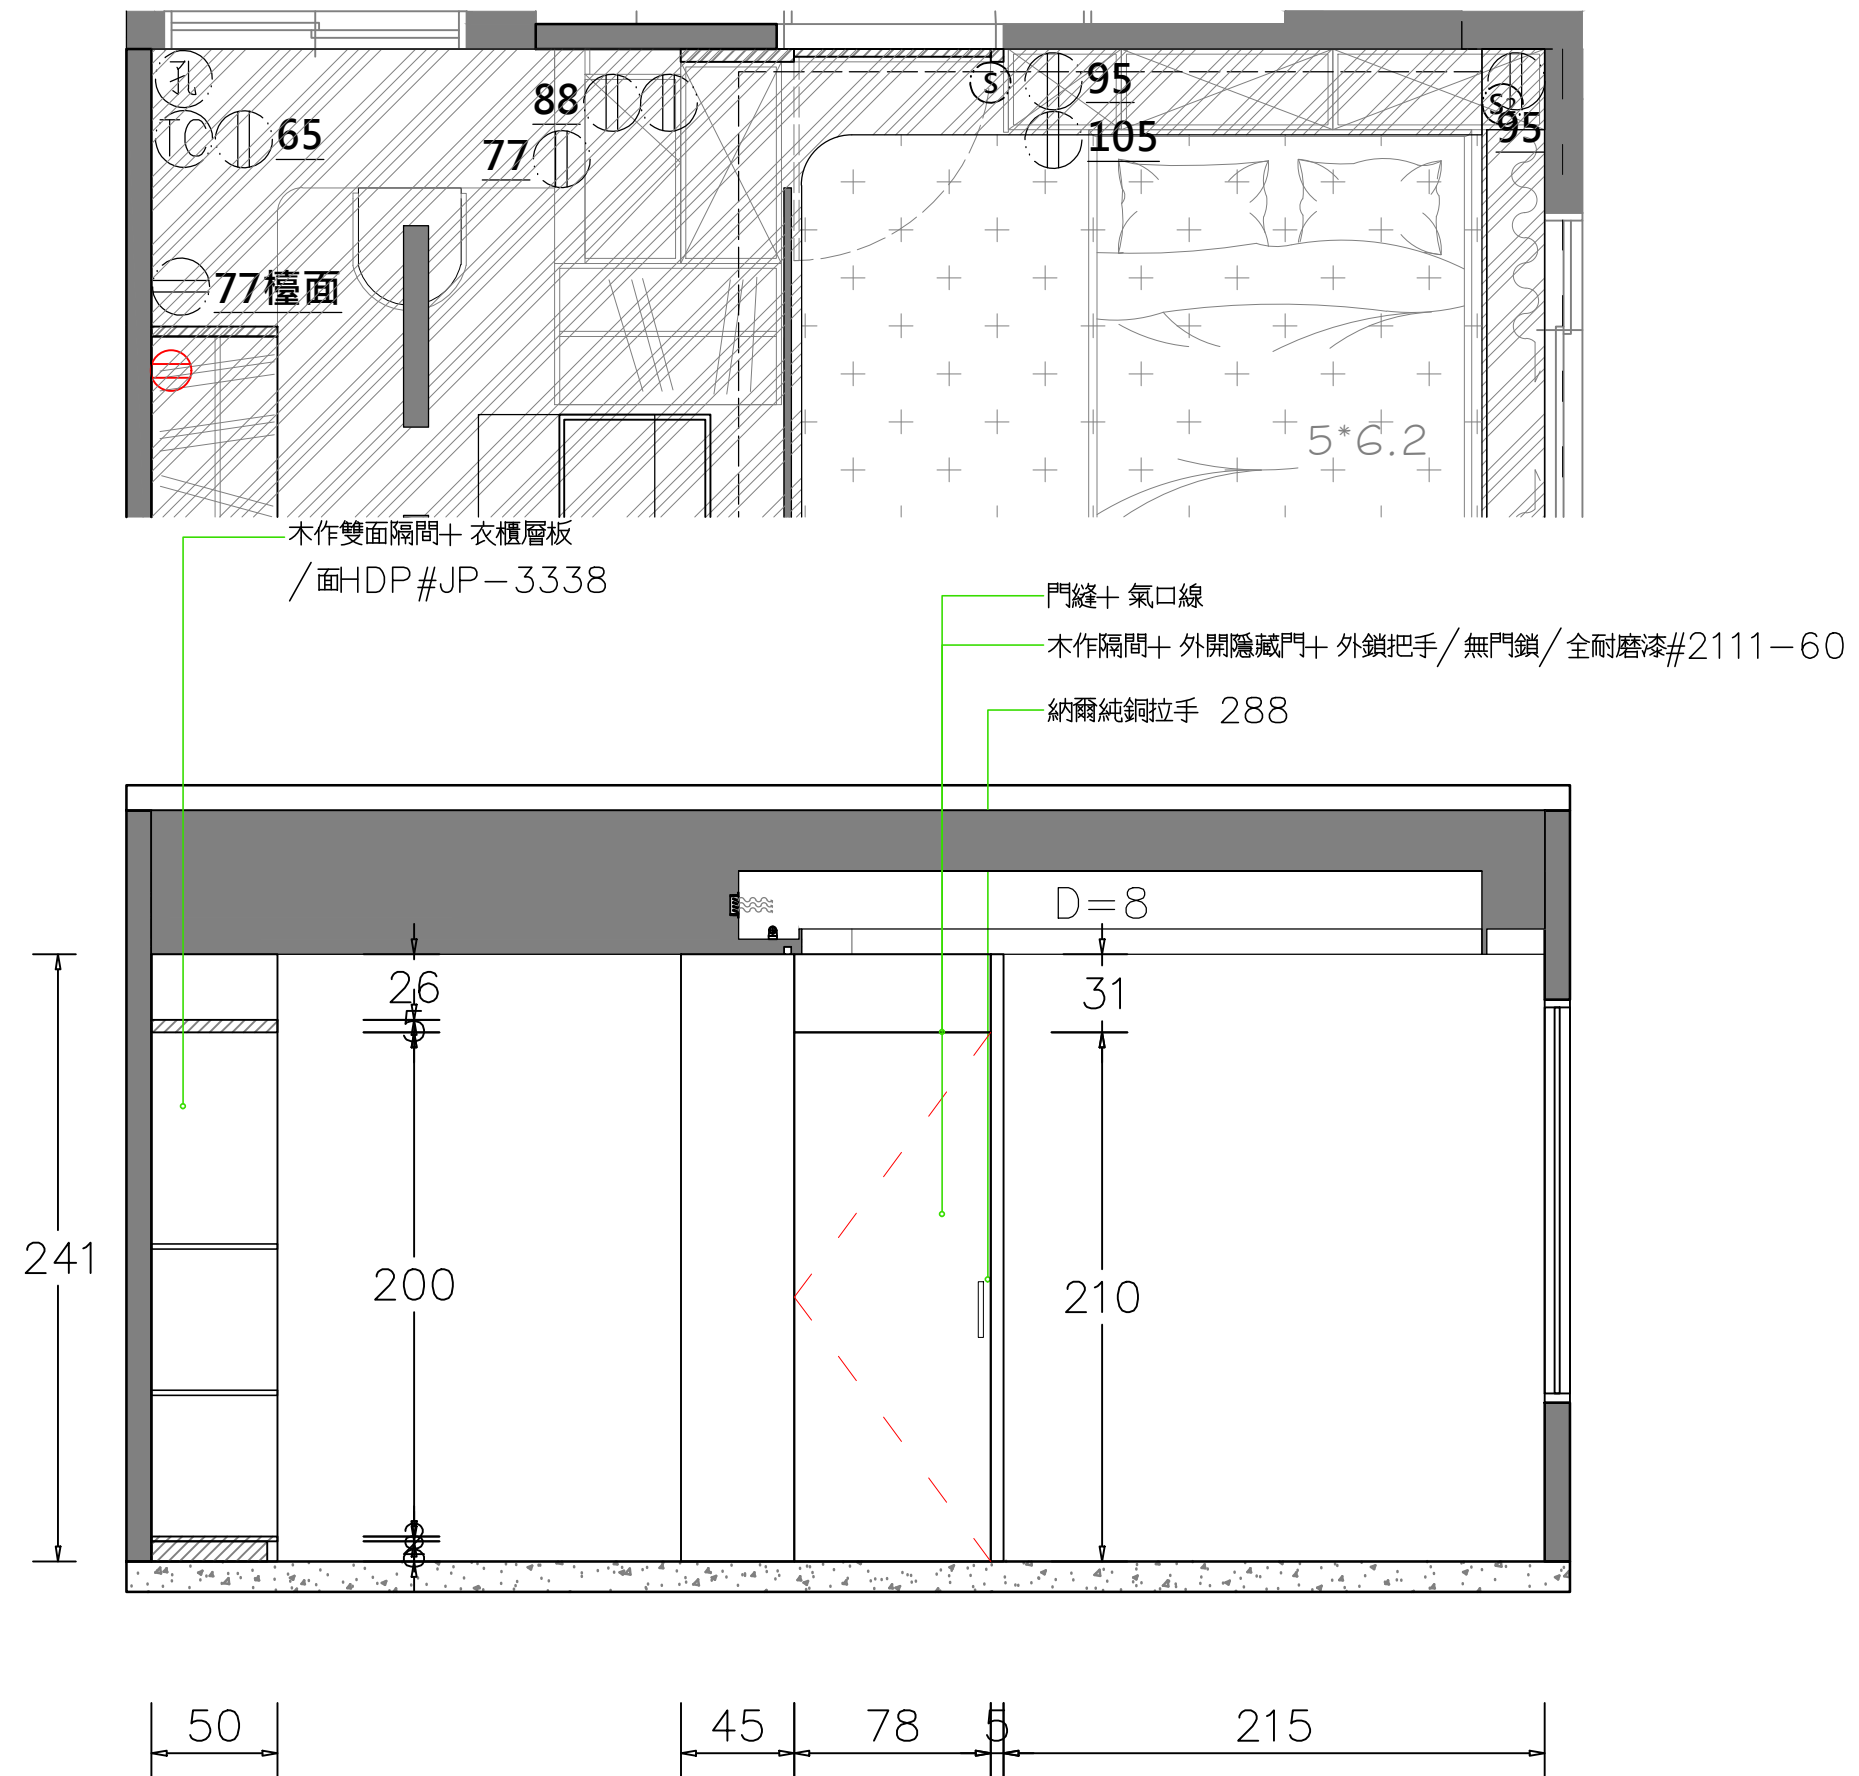

DRAW INTERIOR DESIGN 台中市臺灣大道二段285號31F



琢越空間設計

本圖內容	主臥浴室隱藏門/更衣室木作	設計	Alison	比例	1 / 30	日期		圖號	
案名	大通大美7A6	繪圖	Alison	單位	CM/公分	115.7.1		2	

門片、抽頭、美背 U705 ST9
櫃體、枱面、外包板 H3165 ST12
深度壁板 U705 ST9

系統櫃鉸鍊：TAI KE 油壓緩衝鉸鍊
抽屜滑軌：HQ 三節式油壓緩衝滑軌

尺寸依現場實際狀況為準

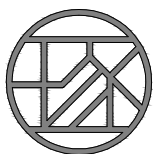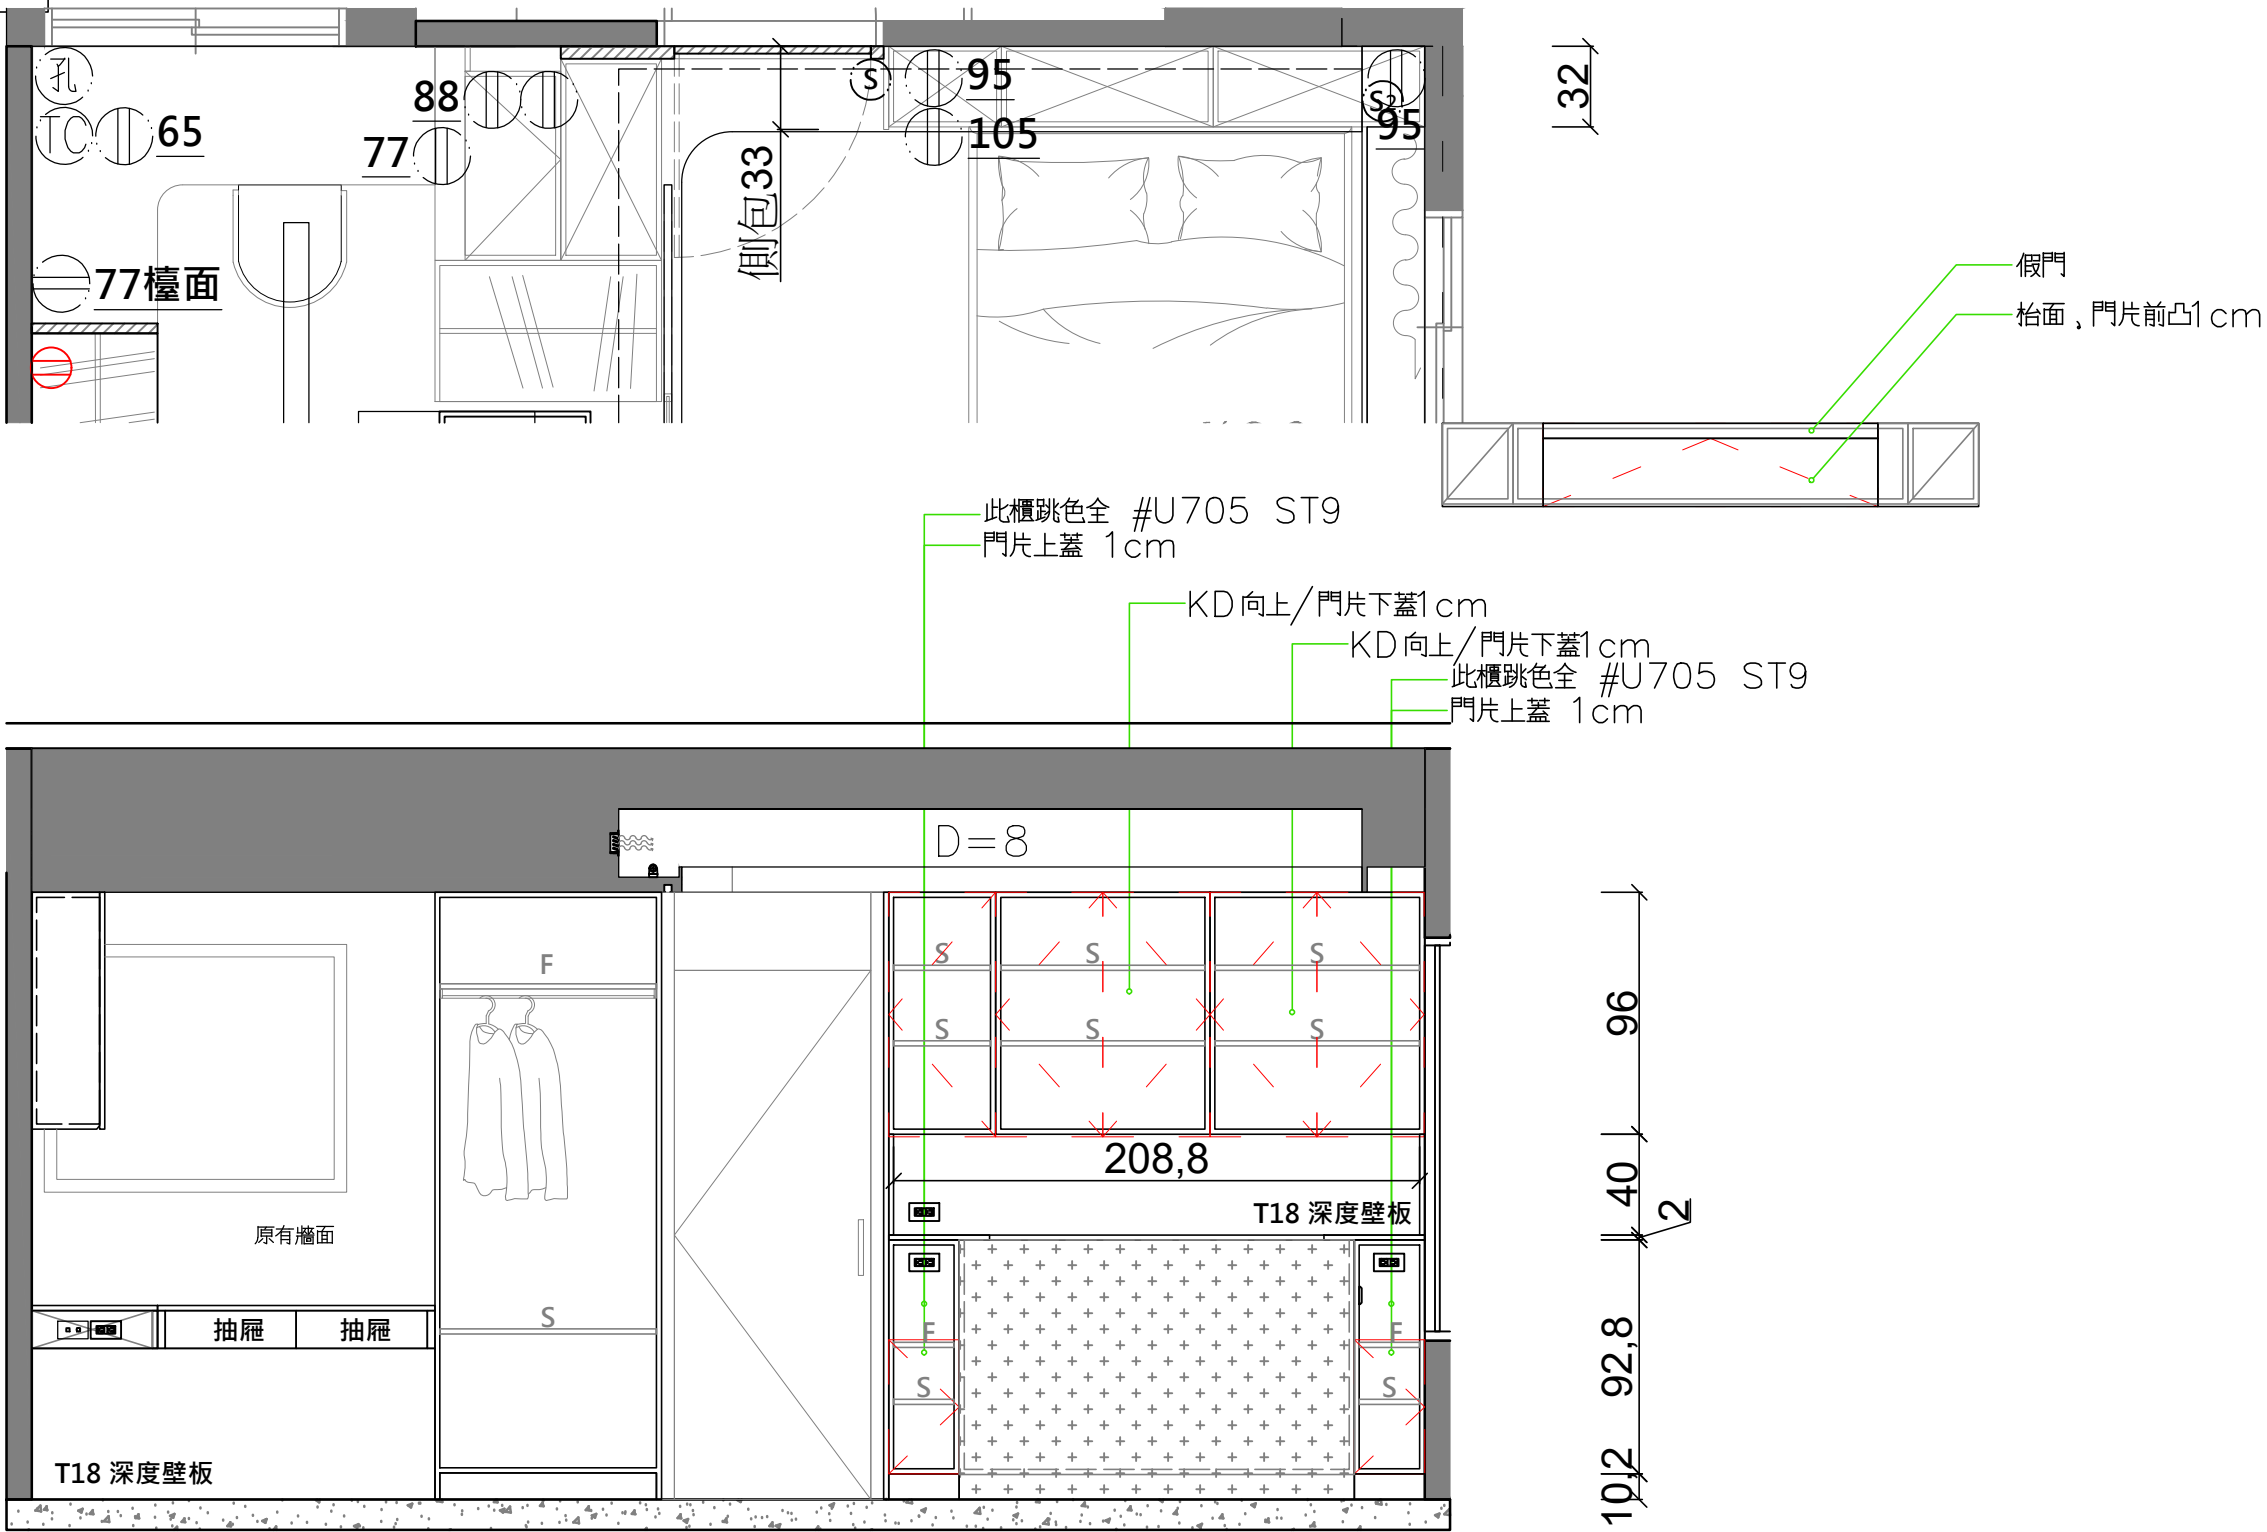


琢越空間設計

DRAW INTERIOR DESIGN 台中市臺灣大道二段285號31F

本圖內容	主臥床頭	設計	Alison	比例	1 / 30	日期	
案名	大通大美7A6	繪圖	Alison	單位	CM/公分	115.7.1	圖號 08

系統櫃鉸鍊：TAI KE 油壓緩衝鉸鍊
抽屜滑軌：HQ 三節式油壓緩衝滑軌

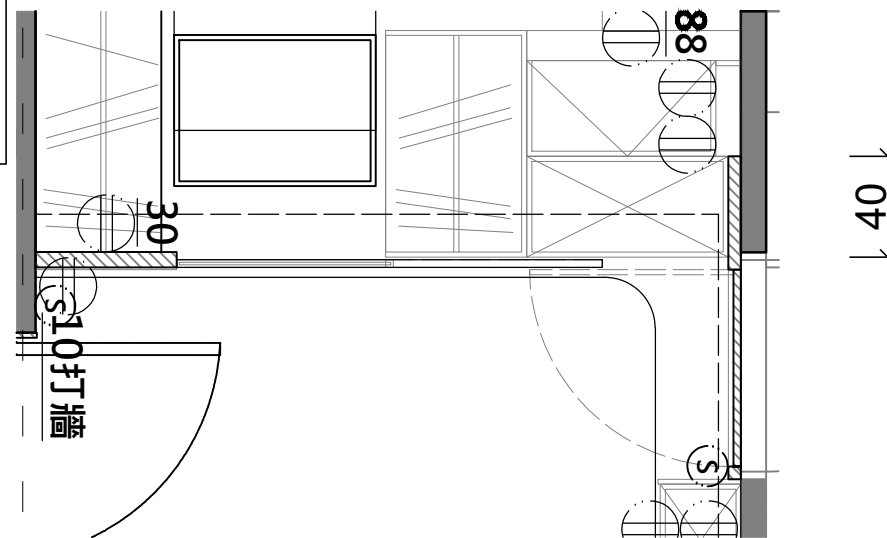




8mm 清玻門片／緩衝玻璃鉸鍊

納爾純銅拉手 192

抽屜以上左右側板嵌1*1 鋁條燈

* 距離：置中



無底板櫃／做人柱玻璃門片，抽屜櫃內退4cm

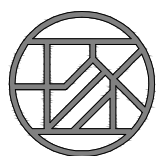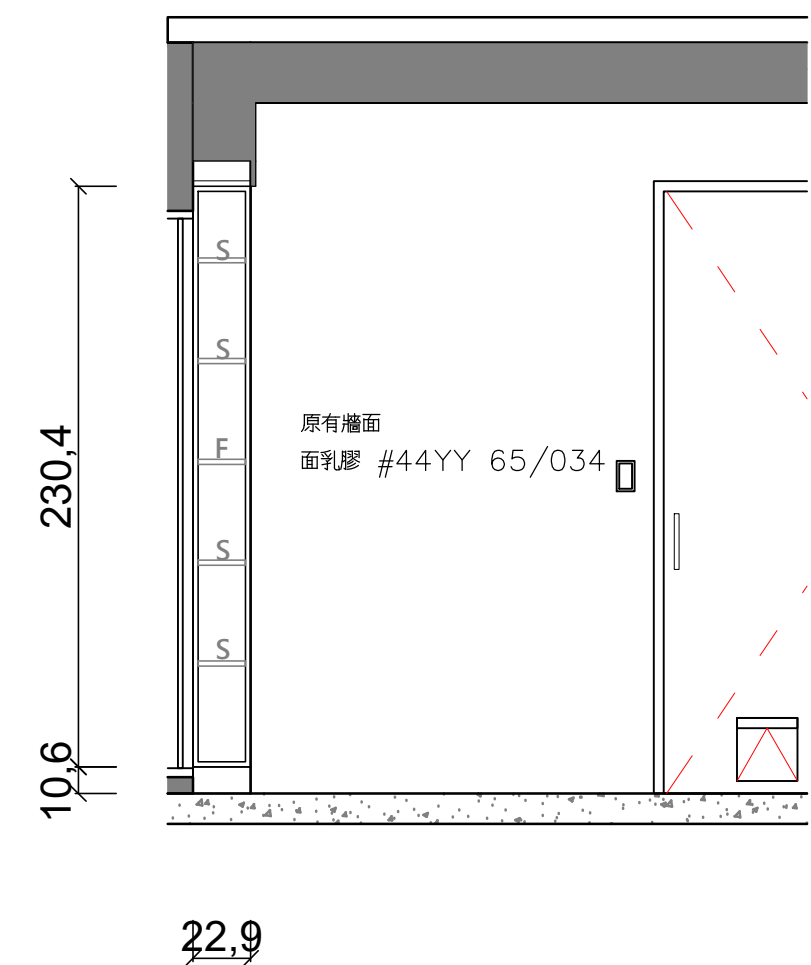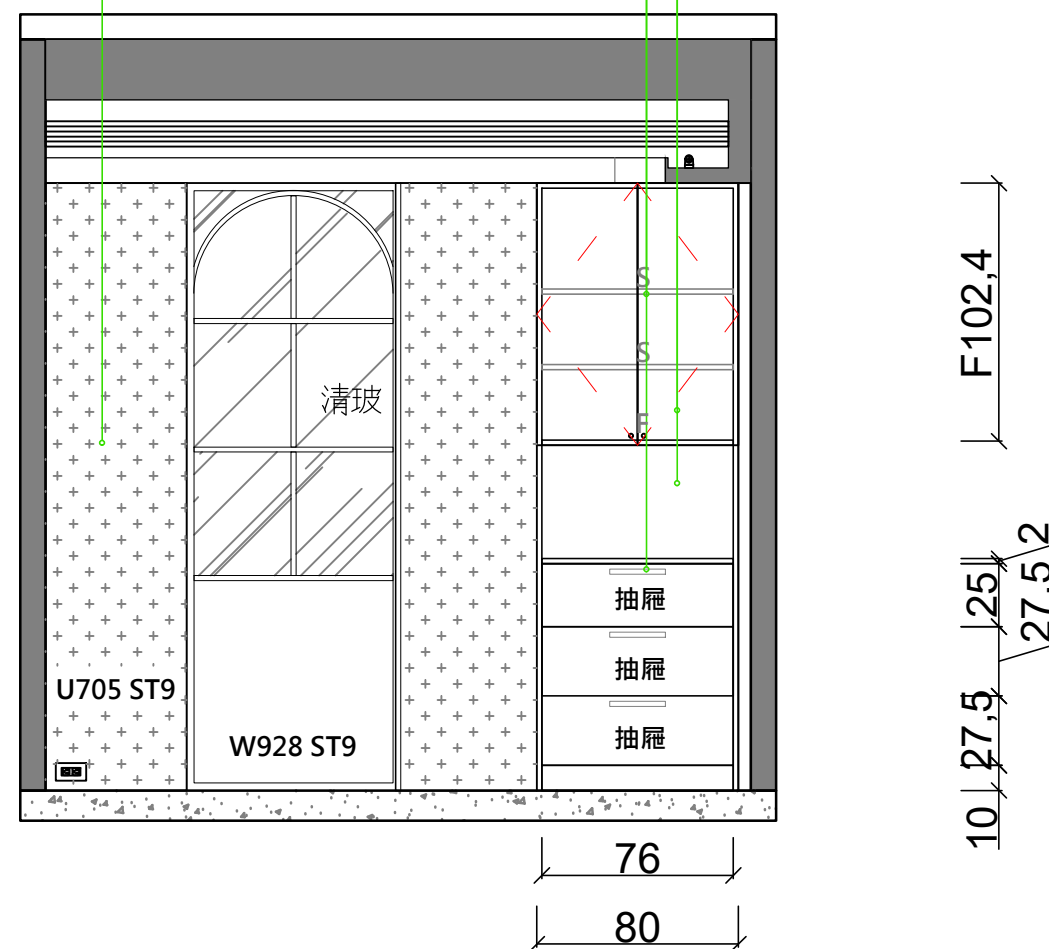

DRAW INTERIOR DESIGN 台中市臺灣大道二段285號31F

本圖內容	主臥展示櫃/凹洞櫃	設計	Alison	比例	1 / 30	日期	圖號
案名	大通大美7A6	繪圖	Alison	單位	CM/公分	115.7.1	09





尺寸依現場實際狀況為準

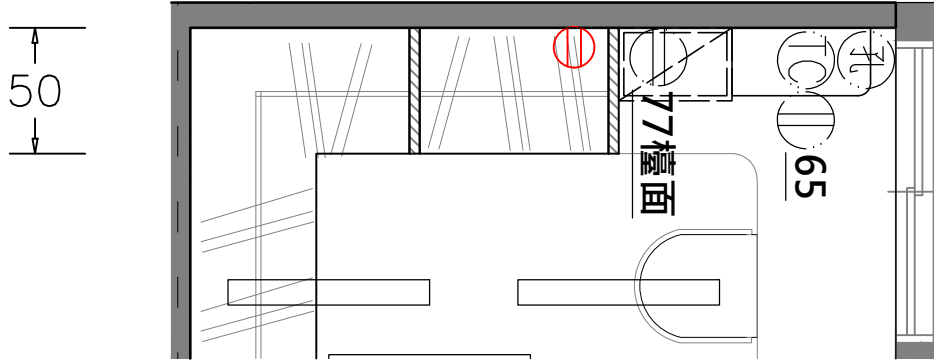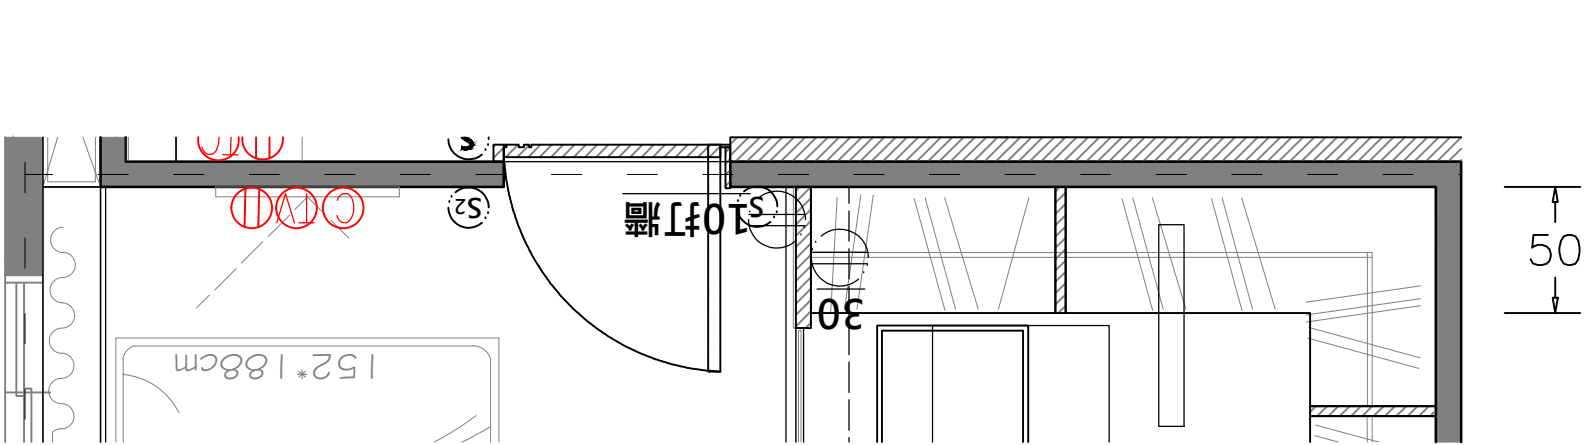

內推自動回歸隱藏門/面HDP#JP-3338
/貓門造型/納爾純銅拉手 288/隱藏鎖



立峰 #RM920 玫瑰金吊衣桿

立峰 #RM920 玫瑰金吊衣桿

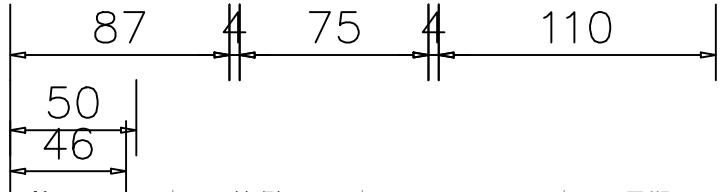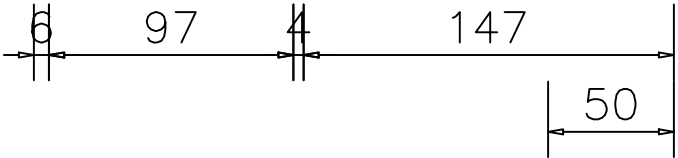
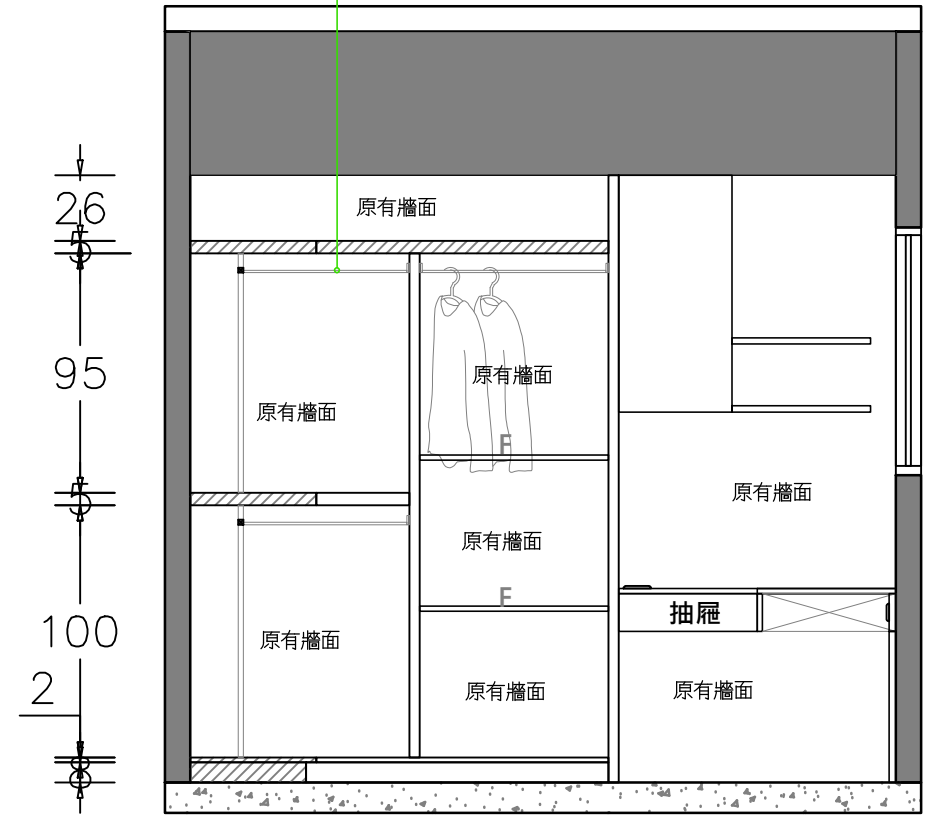
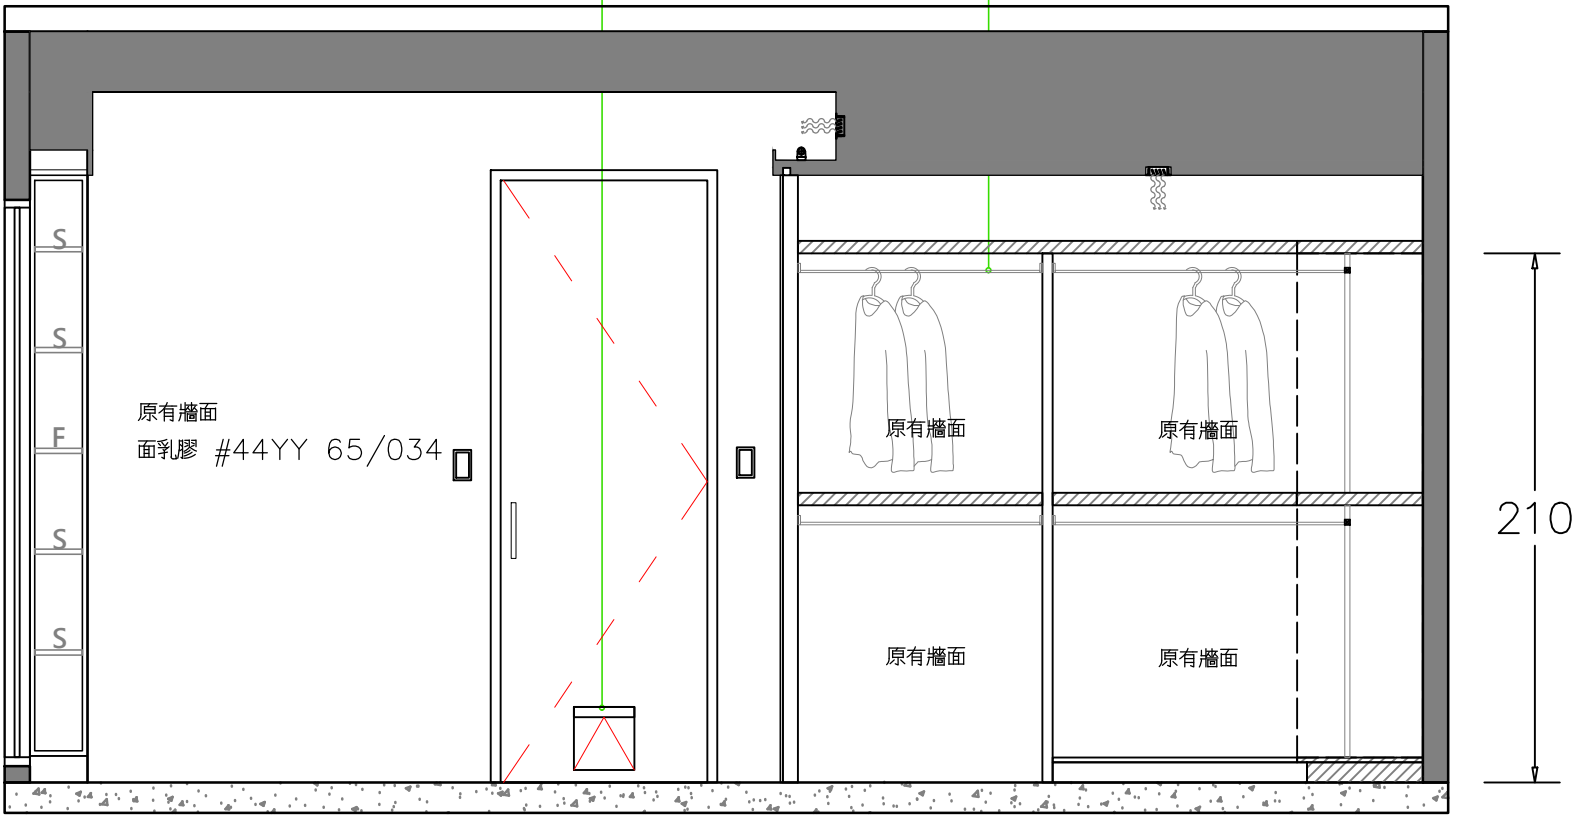


吊櫃桶身, T25, 衣櫃層板 H3165 ST12
門片, 梳妝台全 U705 ST9

系統櫃鉸鍊 : TAI KE 油壓緩衝鉸鍊
抽屜滑軌 : HQ 三節式油壓緩衝滑軌

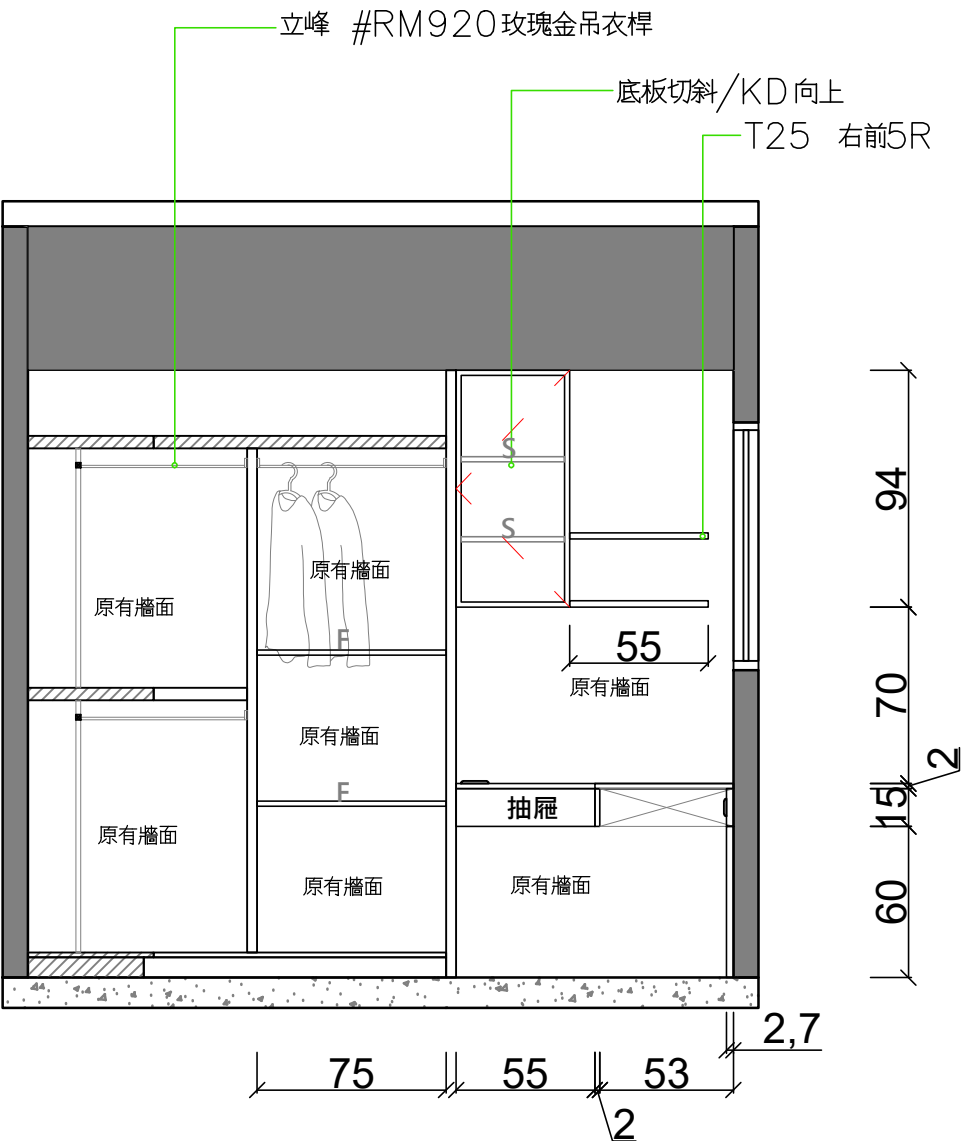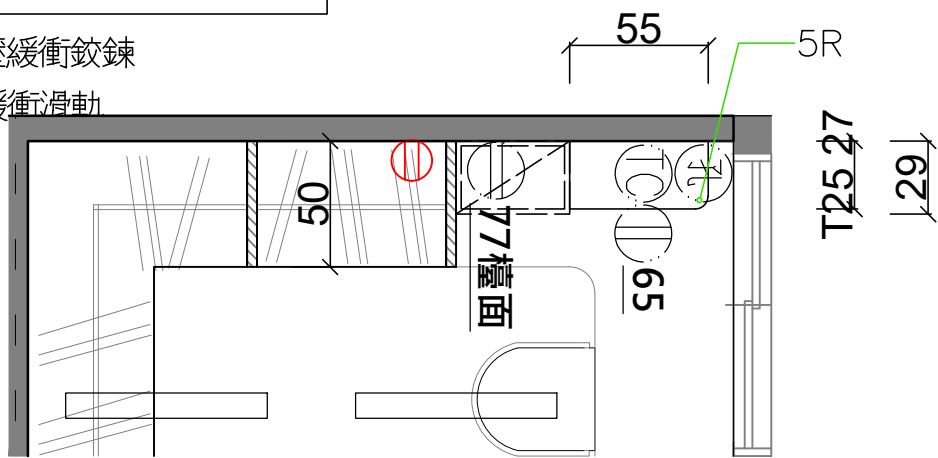

尺寸依現場實際狀況為準

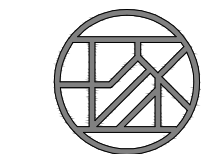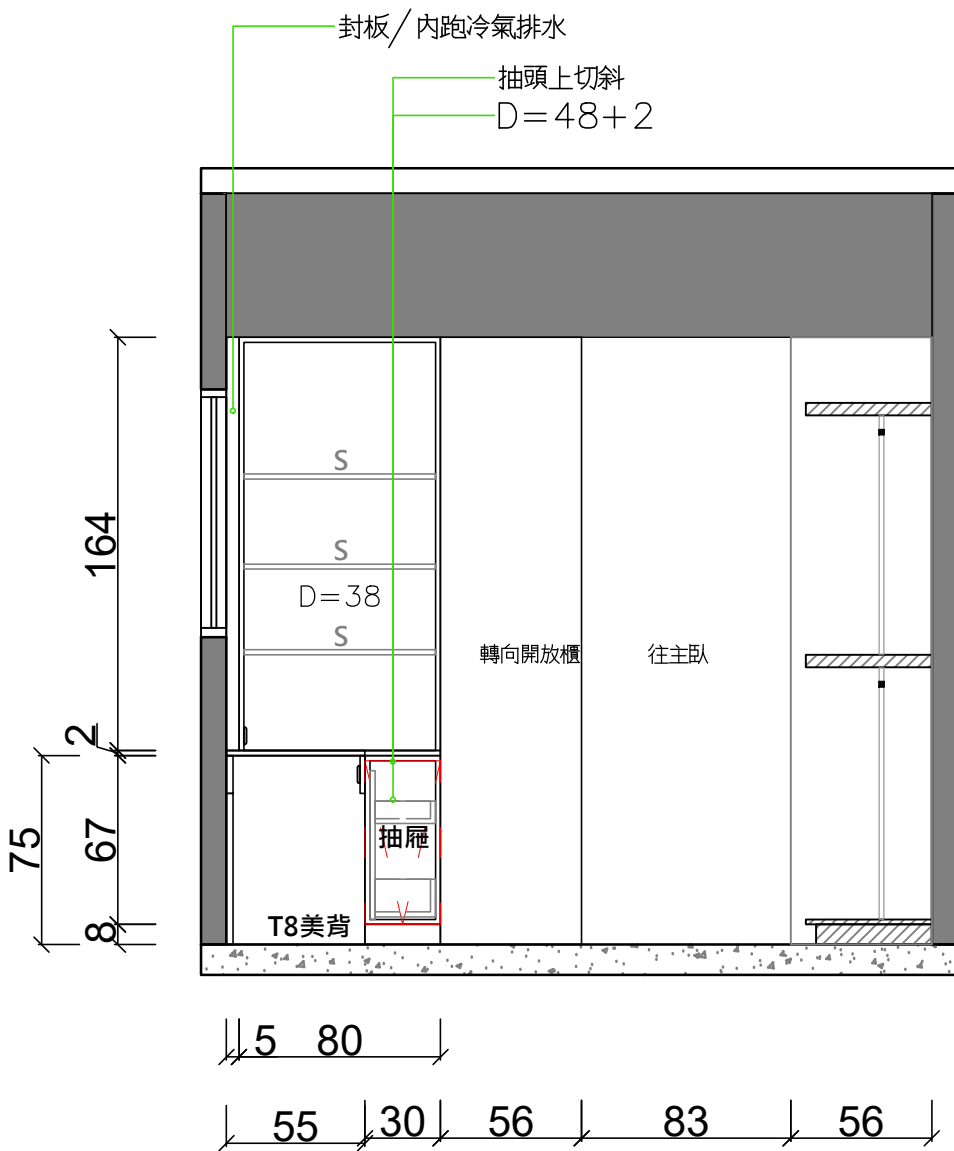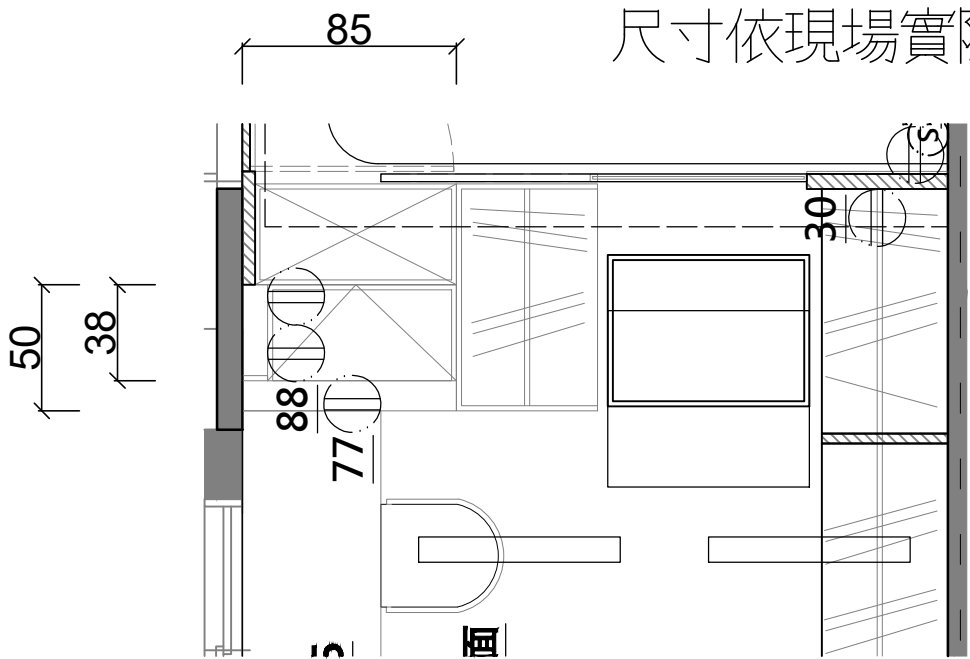

琢越空間設計






DRAW INTERIOR DESIGN 台中市臺灣大道二段285號31F

本圖內容	更衣室系統櫃	設計	Alison	比例	1 / 30	日期		圖號	
案名	大通大美7A6	繪圖	Alison	單位	CM/公分	115.7.1		010	

深度壁板, 衣櫃, 梳妝台全 U705 ST9

尺寸依現場實際狀況為準

系統櫃鉸鍊 : TAI KE 油壓緩衝鉸鍊
抽屜滑軌 : HQ 三節式油壓緩衝滑軌

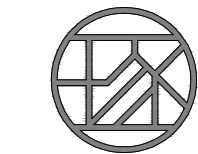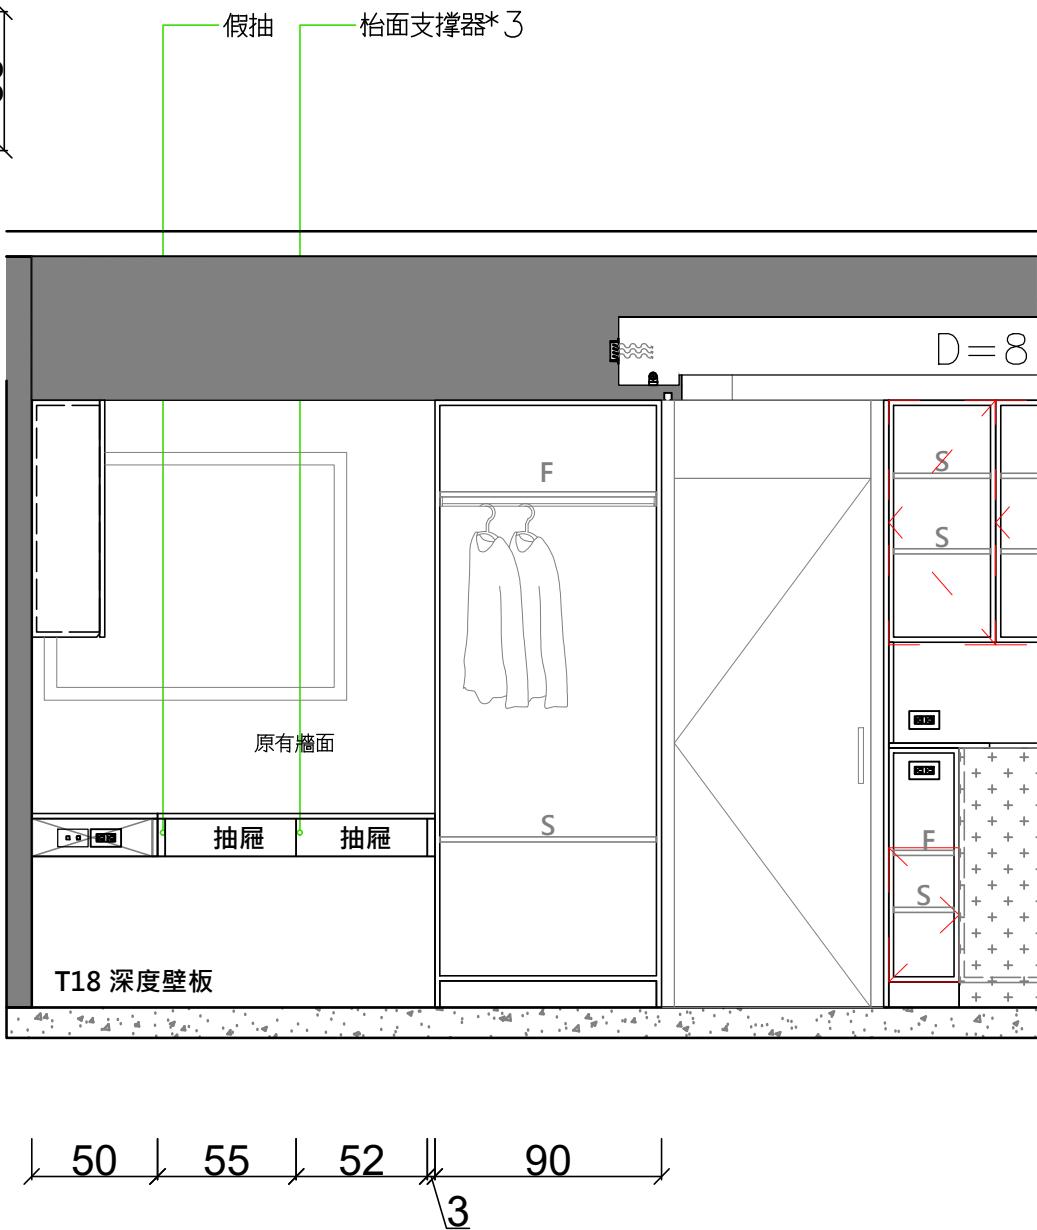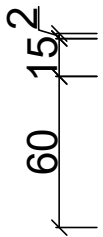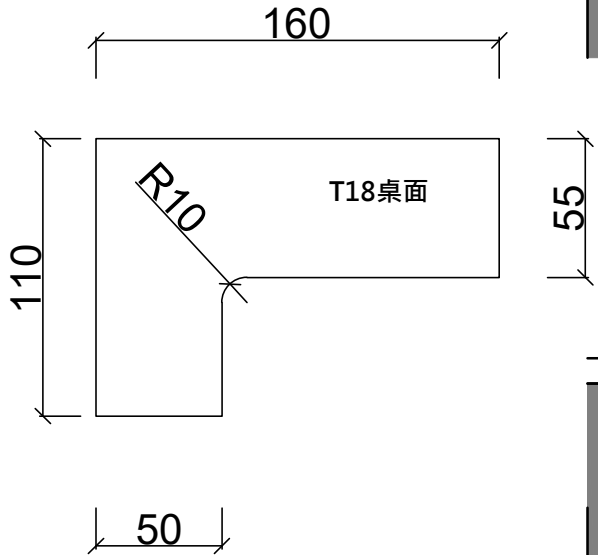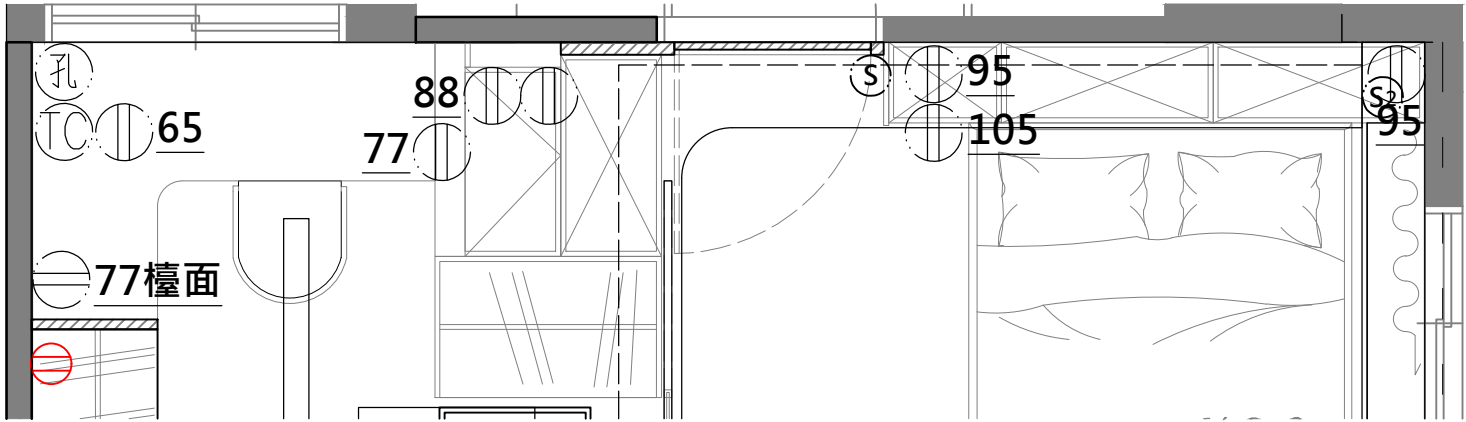

琢越空間設計





DRAW INTERIOR DESIGN 台中市臺灣大道二段285號31F

本圖內容	更衣室梳妝台/系統櫃	設計	Alison	比例	1 / 30	日期	
案名	大通大美7A6	繪圖	Alison	單位	CM/公分	115.7.1	圖號 011

全 H3433 ST22 (待定)

系統櫃鉸鍊：TAI KE 油壓緩衝鉸鍊
抽屜滑軌：HQ 三節式油壓緩衝滑軌

尺寸依現場實際狀況為準

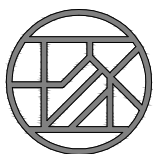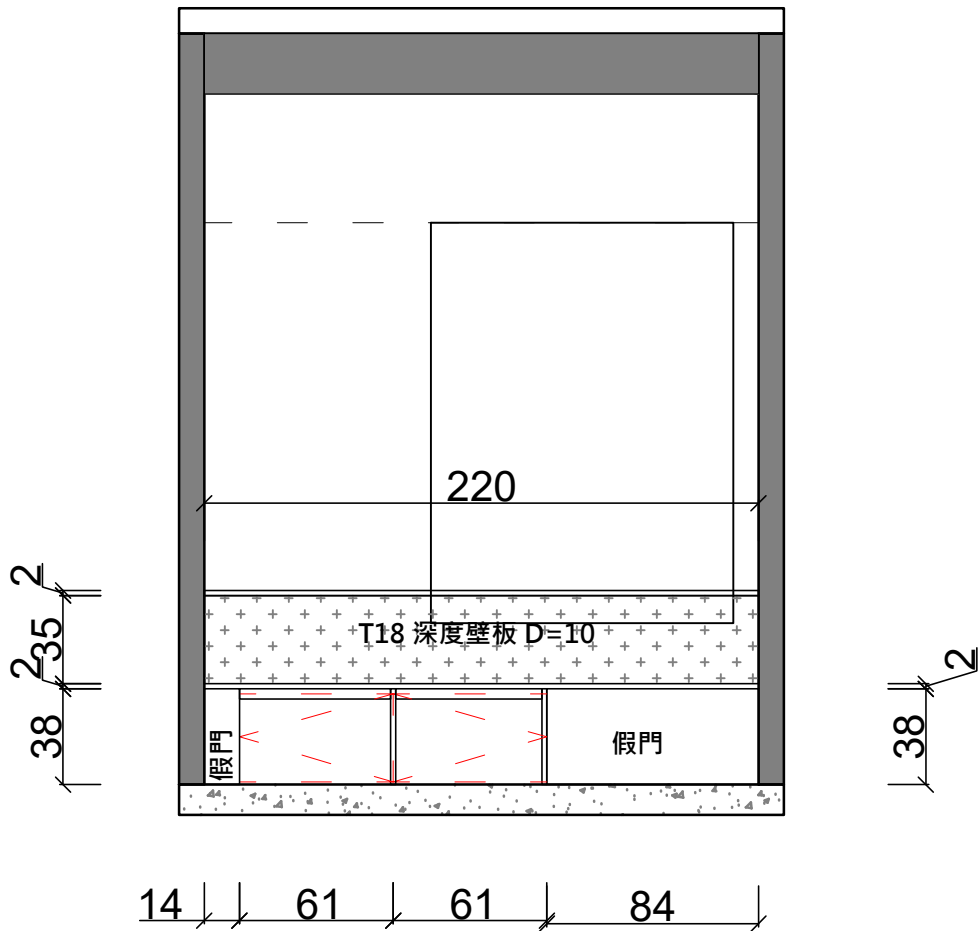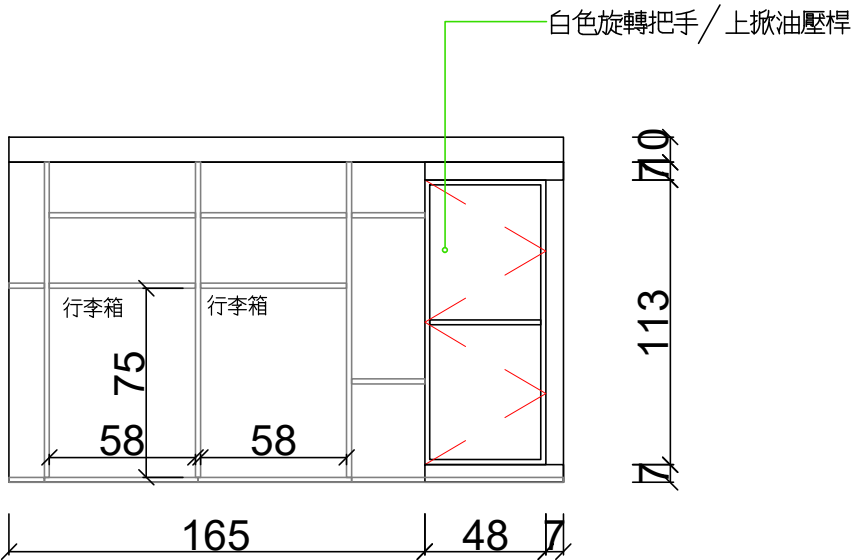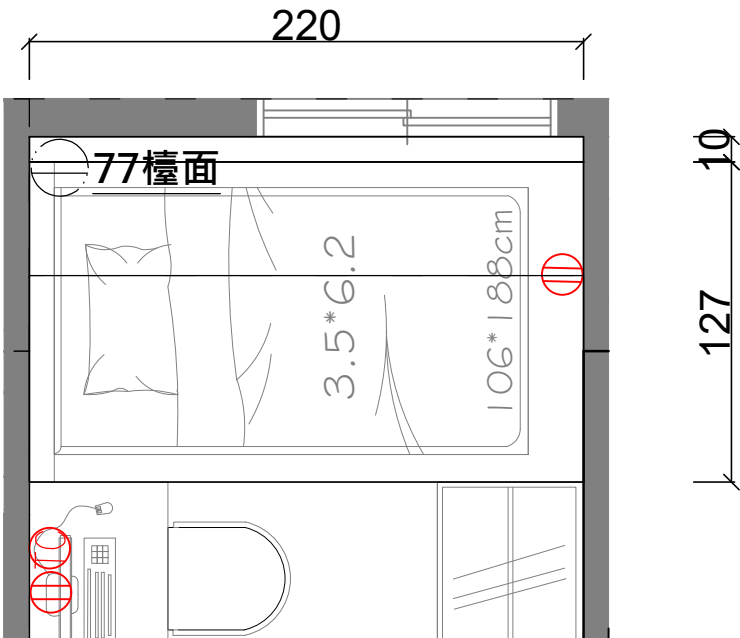

琢越空間設計

DRAW INTERIOR DESIGN 台中市臺灣大道二段285號31F

本圖內容	次臥收納床座	設計	Alison	比例	1 / 30	日期	圖號
案名	大通大美7A6	繪圖	Alison	單位	CM/公分	115.7.1	012



















不用鎖














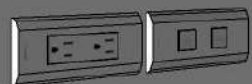

40.0 cm



